
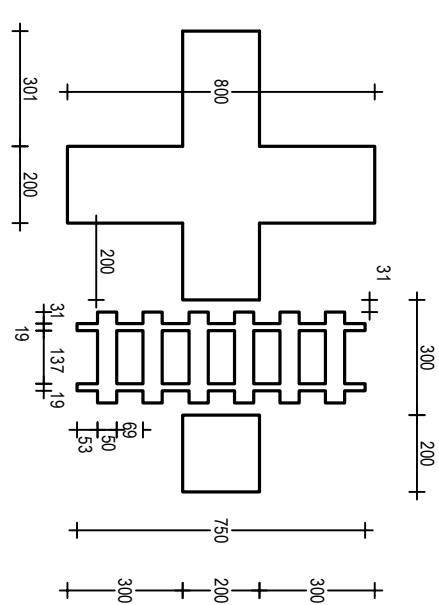
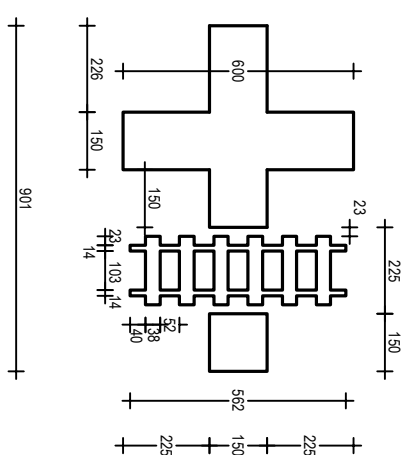
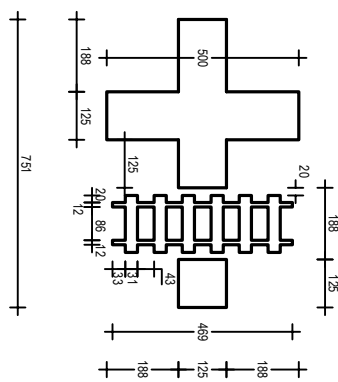
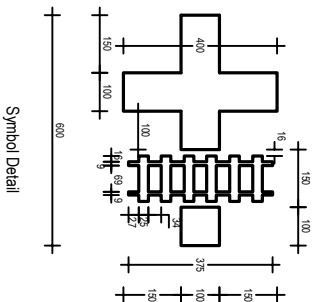
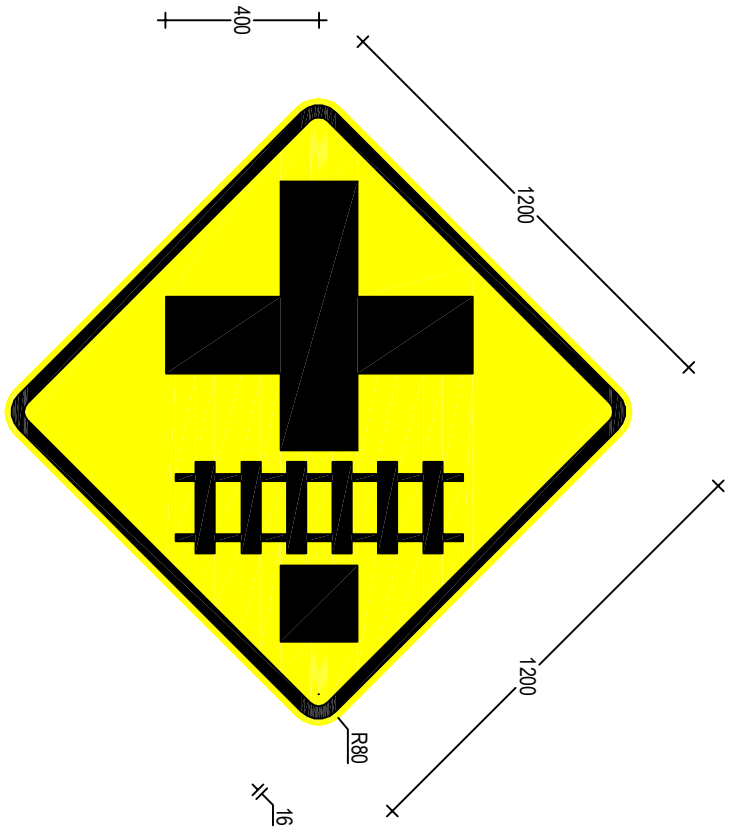
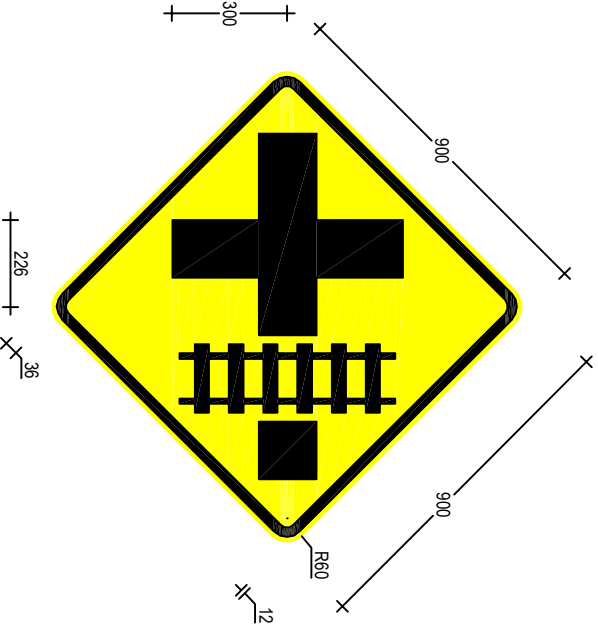
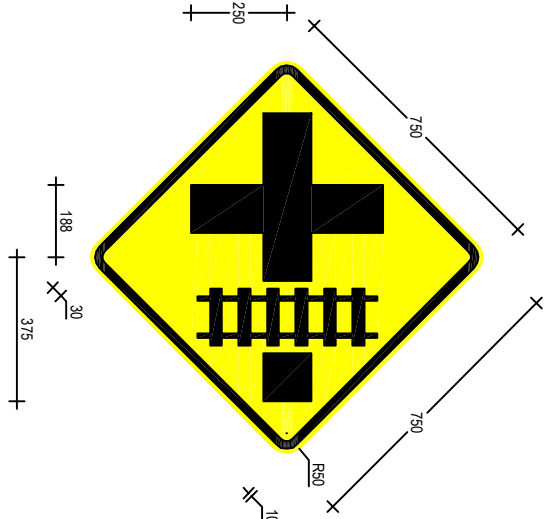


05101520253035404550mm ON A3 SIZE ORIGINAL

QR CODE	Scan to Check Document Version	REV	DATE	AMENDMENT / REVISION DESCRIPTION	APPROVAL	DRAWING FILE LOCATION / NAME: H:\SIGNS\TTP\DRAWINGS\SP\CTW\ARNW7-13.dwg			
		01	23-08-18	AS Fonts & material classification revised	P. Oliver	MATERIALS: ALUMINIUM SIGN BLACK LEGEND AND BORDER ON AS1906.1 CL.400 YELLOW REFLECTORISED GROUND			
ALL DIMENSIONS ARE IN MILLIMETRES UNLESS OTHERWISE SPECIFIED						SIGN TO BE MANUFACTURED IN ACCORDANCE WITH RMS QA SPECIFICATION 3400			
DESIGNED						VERIFIED			
SIGNED: M. Davies DATE: 31-07-19						SIGNED: P. Oliver NAME: P. Oliver TITLE: Manager, Guidance & Delineation DATE: 31-07-19			
REVIEWED						PREPARED BY			
SIGNED: J. Rozdos NAME: J. Rozdos DATE: 31-07-19						GUIDANCE AND DELINEATION UNIT TRAFFIC ENGINEERING SERVICES TECHNICAL AND PROJECT SERVICES			
WARNING SIGN W7-13(R) RAIL CROSSING ON SIDE ROAD (Symbolic Right)						SCALE: 1:20			
EDMS No. XXXXXXXXXX						SHEET No. 1			
ISS 0						SHEET 1 OF 1			

ACCEPTED FOR CONSTRUCTION

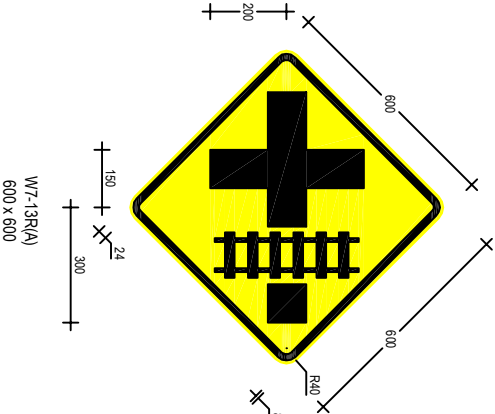

Symbol Detail