
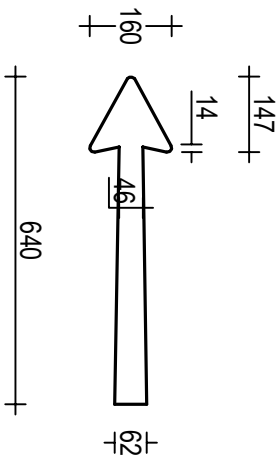
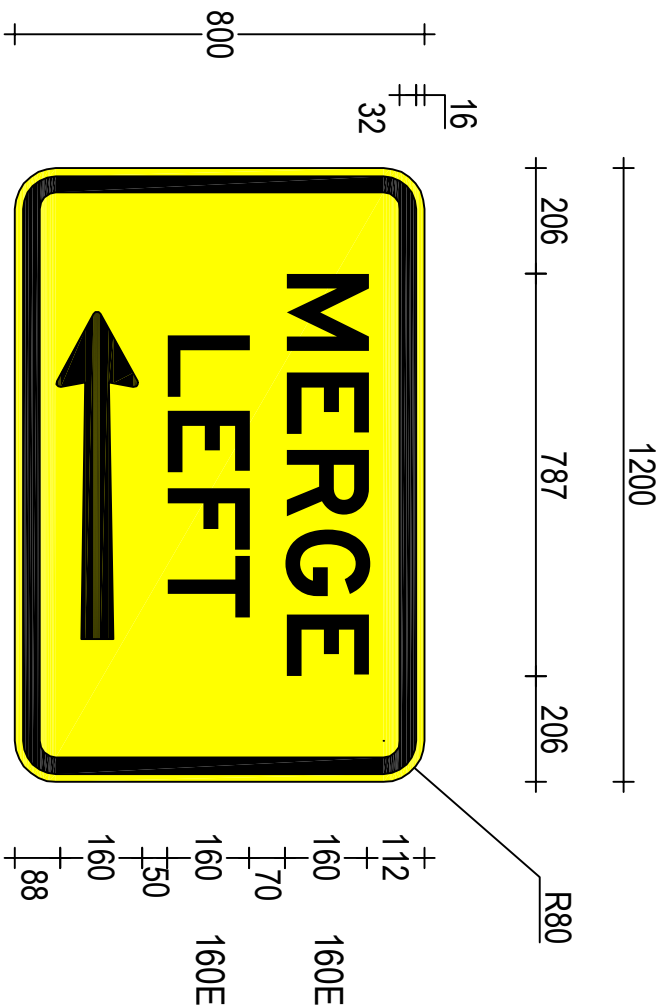
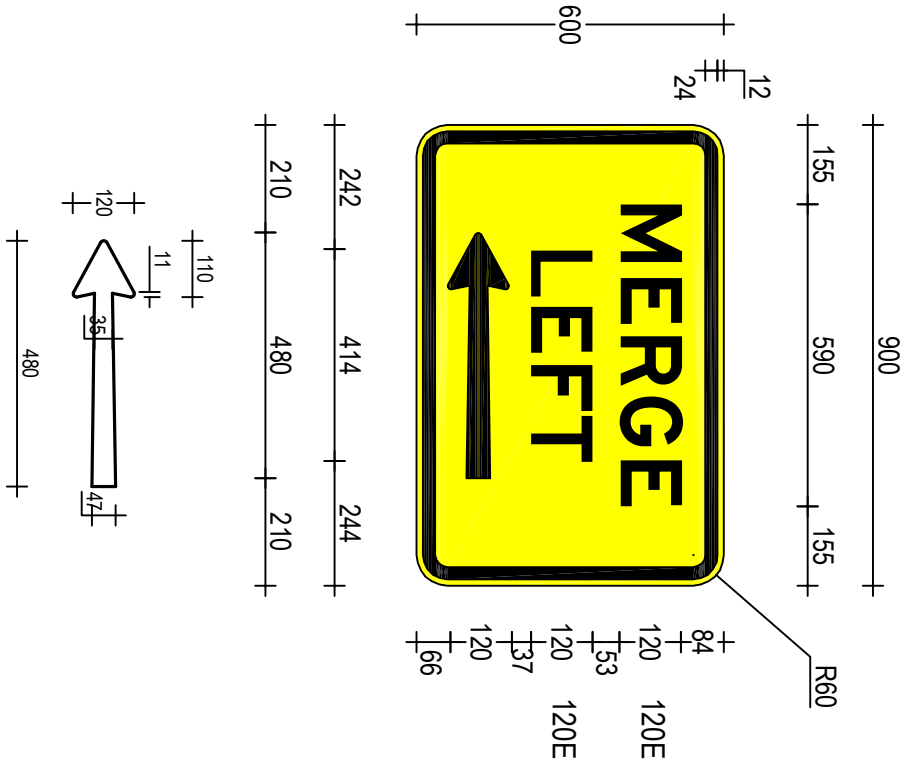


25	OR CODE	BS2400:2015 Document Version	REV	DATE	AMENDMENT / REVISION DESCRIPTION	APPROVAL	DRAWING FILE LOCATION / NAME: H:\SIGN\T\T\DRAWINGS\PL\OTWARRW8-15-1.DWG MATERIALS: ALUMINIUM SIGN BLACK LEGEND SYMBOL AND BORDER ONAS1906.1 CL.400 YELLOW REFLECTORISED GROUND	DESIGNED	SIGNED	VERIFIED	Transport Roads & Maritime Services GOVERNMENT WARNING SIGN W8-15-1 MERGE LEFT (Symbolic) SHEET 1 OF 1					
20			01	23-08-18	AS Form & material classification revised	P Oliver		NAME	M. Davies	SIGNED		P. Oliver				
15								DATE	31-07-19	NAME		Manager Guidance & Delineation				
10								REVIEWED		TITLE		31-07-19				
5								SIGNED	J. Rozos	DATE		31-07-19				
0	ALL DIMENSIONS ARE IN MILLIMETRES UNLESS OTHERWISE SPECIFIED						SIGN TO BE MANUFACTURED IN ACCORDANCE WITH RMS QA SPECIFICATION 3400	PREPARED BY GUIDANCE AND DELINEATION UNIT TRAFFIC ENGINEERING SERVICES TECHNICAL AND PROJECT SERVICES				SCALE: 1:15	EDMS No. XXXXXXXXXX	SHEET No. 1	ISS 0	A

ACCEPTED FOR CONSTRUCTION

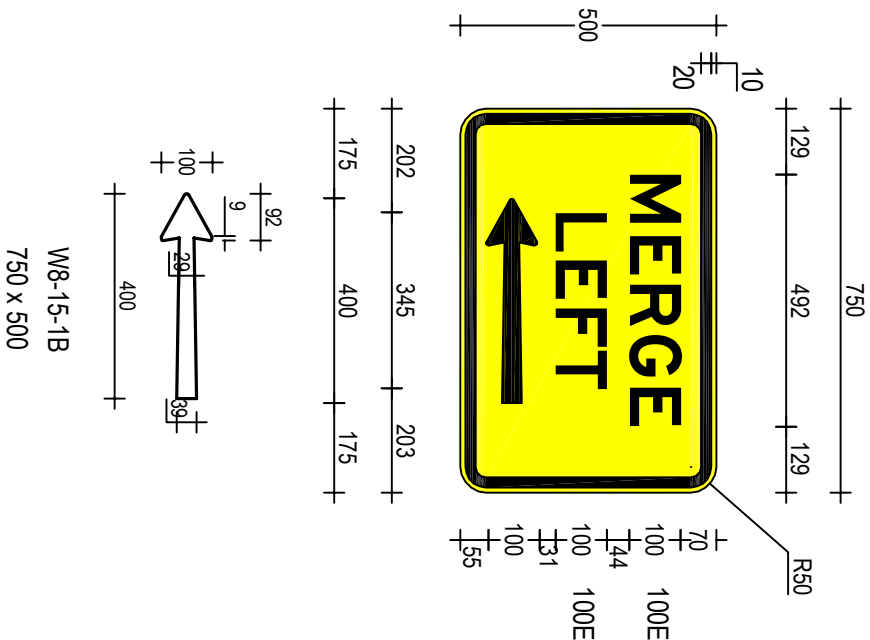

W8-15-1n(D)
1200 x 800