



ACCEPTED FOR CONSTRUCTION

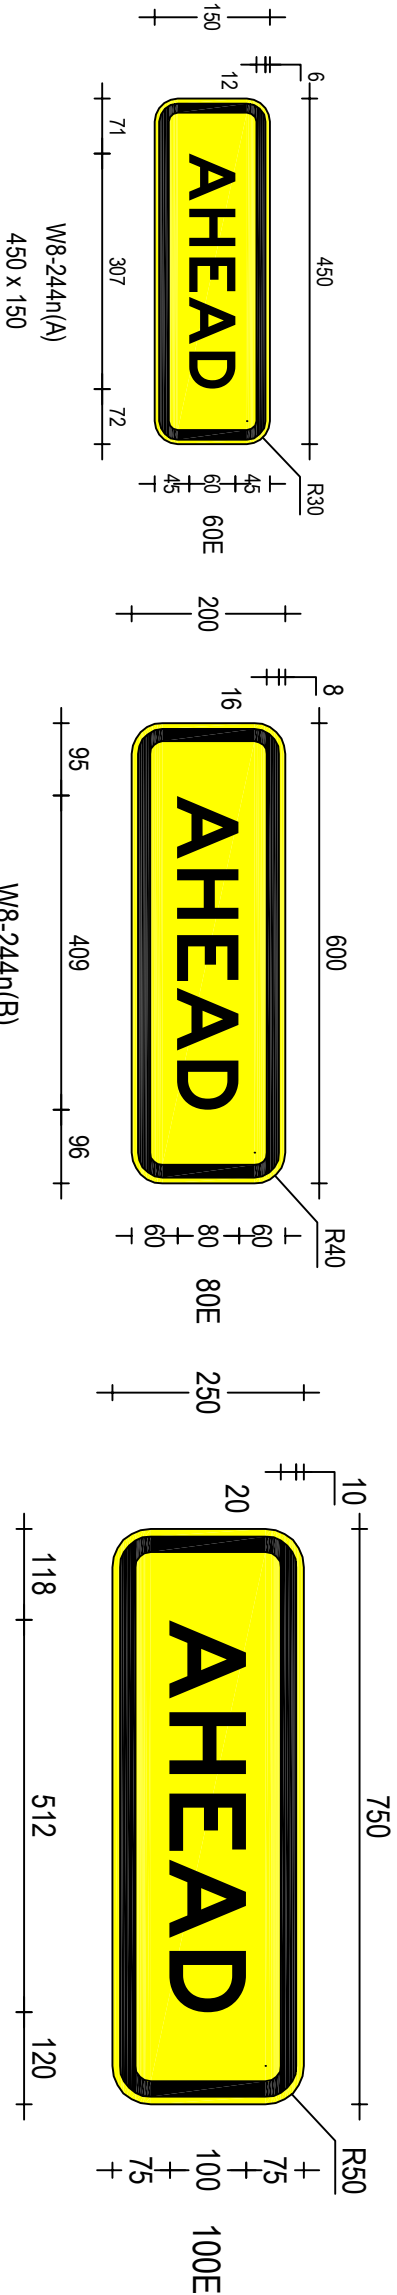

W8-244n(A)
450 x 150

W8-244n(B)
600 x 200

W8-244n(C)
750 x 250

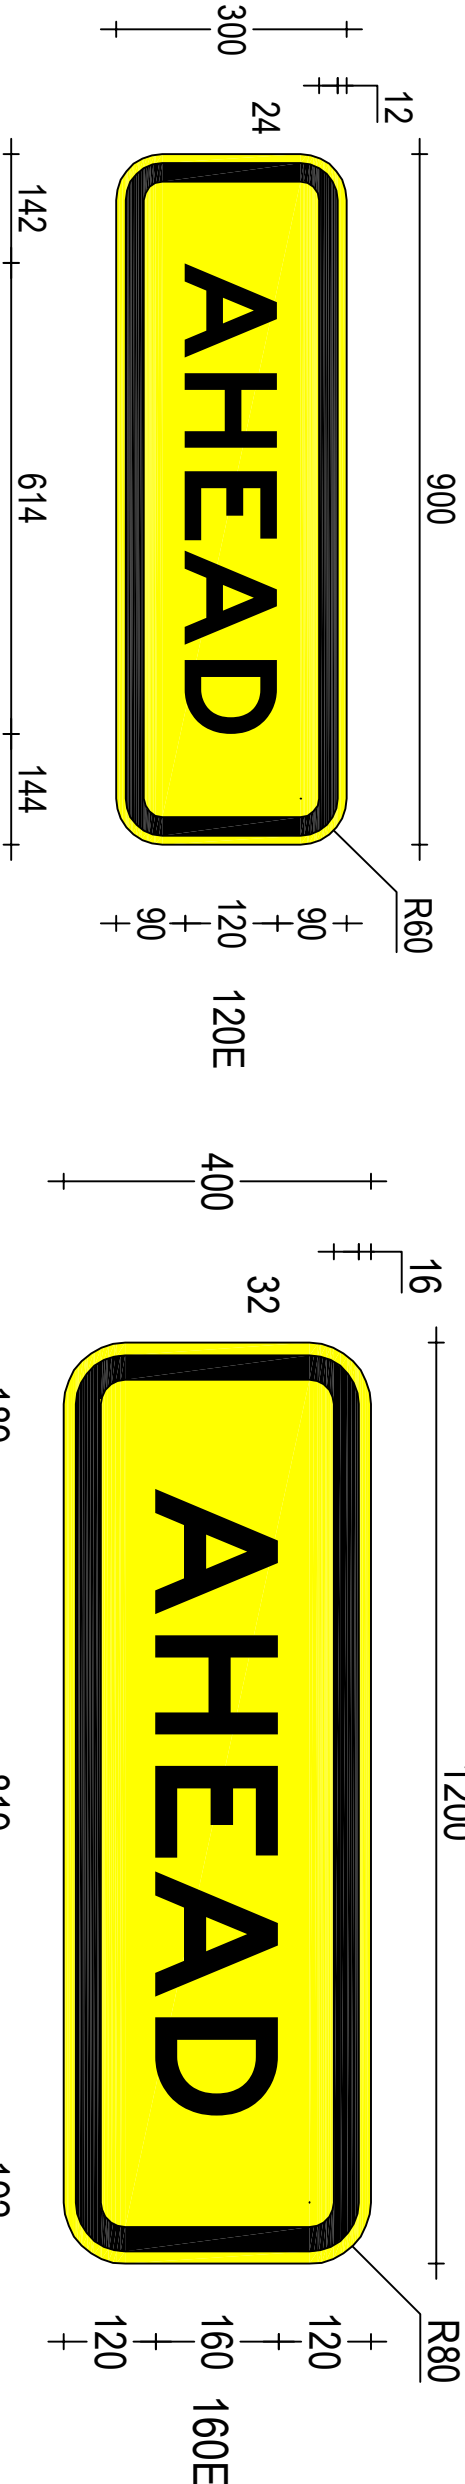

W8-244n(D)
900 x 300

W8-244n(E)
1200 x 400

W8-244n(F)
189 x 192

ALL DIMENSIONS ARE IN MILLIMETRES UNLESS OTHERWISE SPECIFIED

SIGN TO BE MANUFACTURED IN ACCORDANCE WITH RMS QA SPECIFICATION 3400