

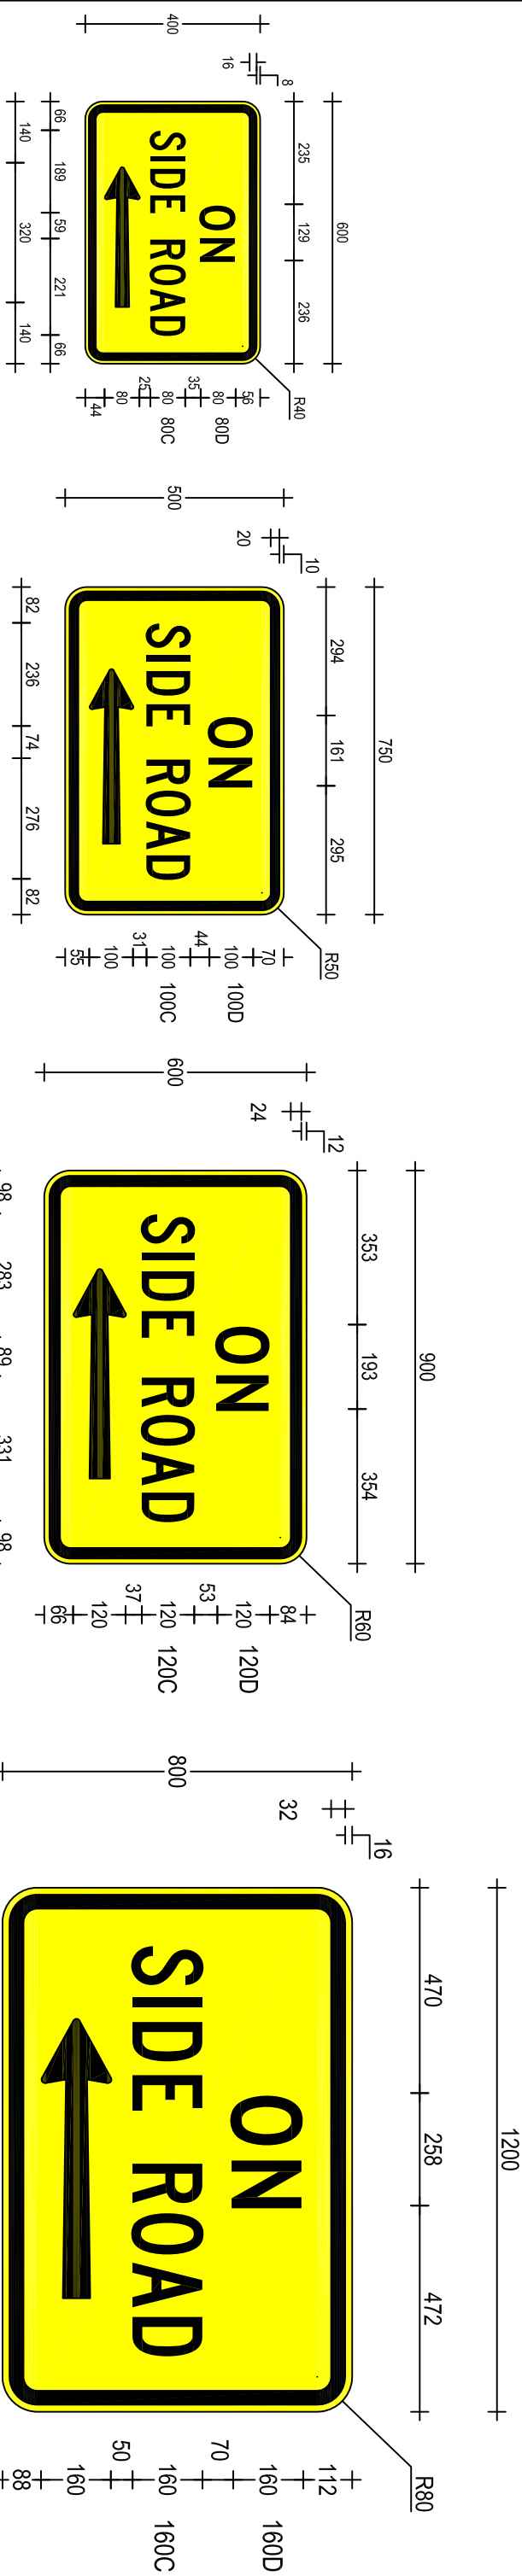


OR CODE	Scan to Check Document Version	REV	DATE	AMENDMENT / REVISION DESCRIPTION	APPROVAL	DRAWING FILE LOCATION / NAME: H:\SIGN\ITTT\DRAWINGS\PLOT\WARRW\W8-3L.DWG
		01	23-03-18	AS Forms & material classification revised	P.Oliver	
ALL DIMENSIONS ARE IN MILLIMETRES UNLESS OTHERWISE SPECIFIED						
SIGN TO BE MANUFACTURED IN ACCORDANCE WITH RMS QA SPECIFICATION 3400						
DESIGNED						
SIGNED: 						
NAME: M. Davies						
DATE: 31-07-19						
REVIEWED						
SIGNED: 						
NAME: J. Rozdos						
DATE: 31-07-19						
VERIFIED						
SIGNED: 						
NAME: P. Oliver						
TITLE: Manager, Guidance & Definition						
DATE: 31-07-19						
PREPARED BY						
GUIDANCE AND DELINEATION UNIT						
TRAFFIC ENGINEERING SERVICES						
TECHNICAL AND PROJECT SERVICES						
WARNING SIGN						
W8-3L(L)						
ON SIDE ROAD (LEFT ARROW)						
SCALE: 1:15						
SHEET 1 OF 1						
EDMS No. XXXXXXXXXX						
SHEET No. 1						
ISSUE 01						
A3						



ACCEPTED FOR CONSTRUCTION

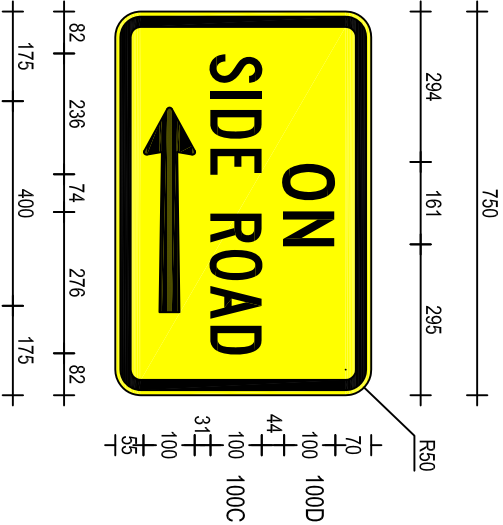



W8-3L(A)
600 x 400

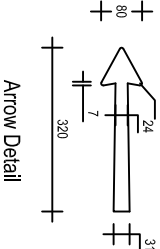


W8-3L(B)
750 x 500

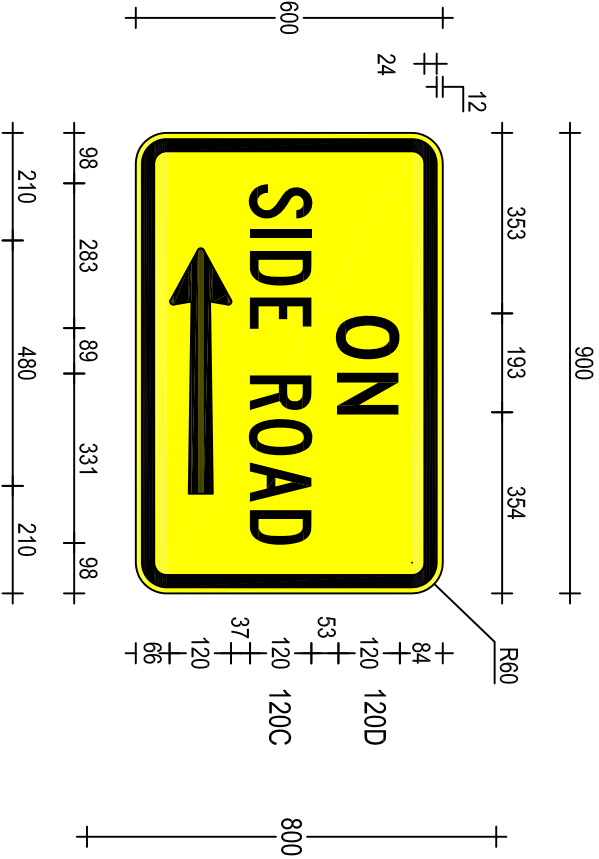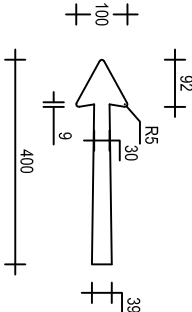

W8-3L(C)
900 x 600

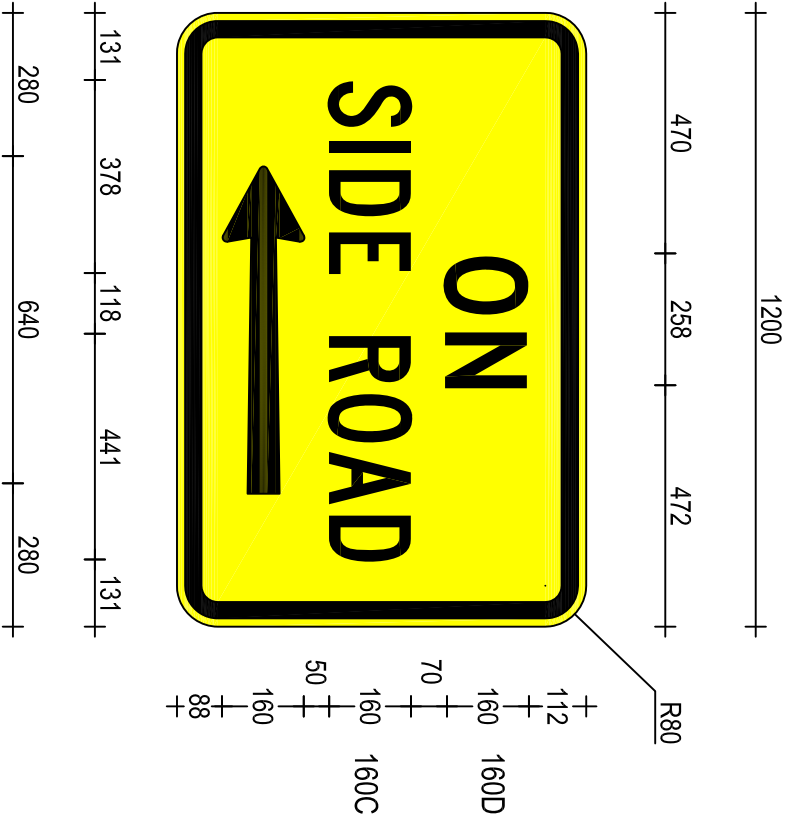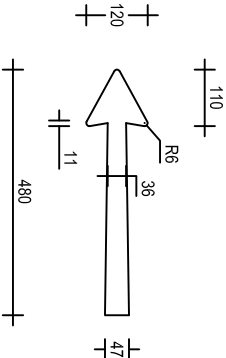

W8-3Ln(D)
1200 x 800

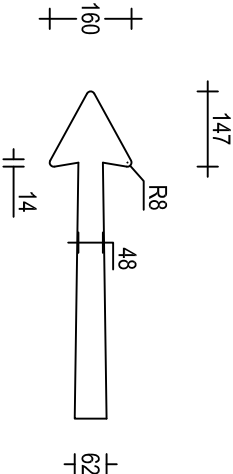

Arrow Detail