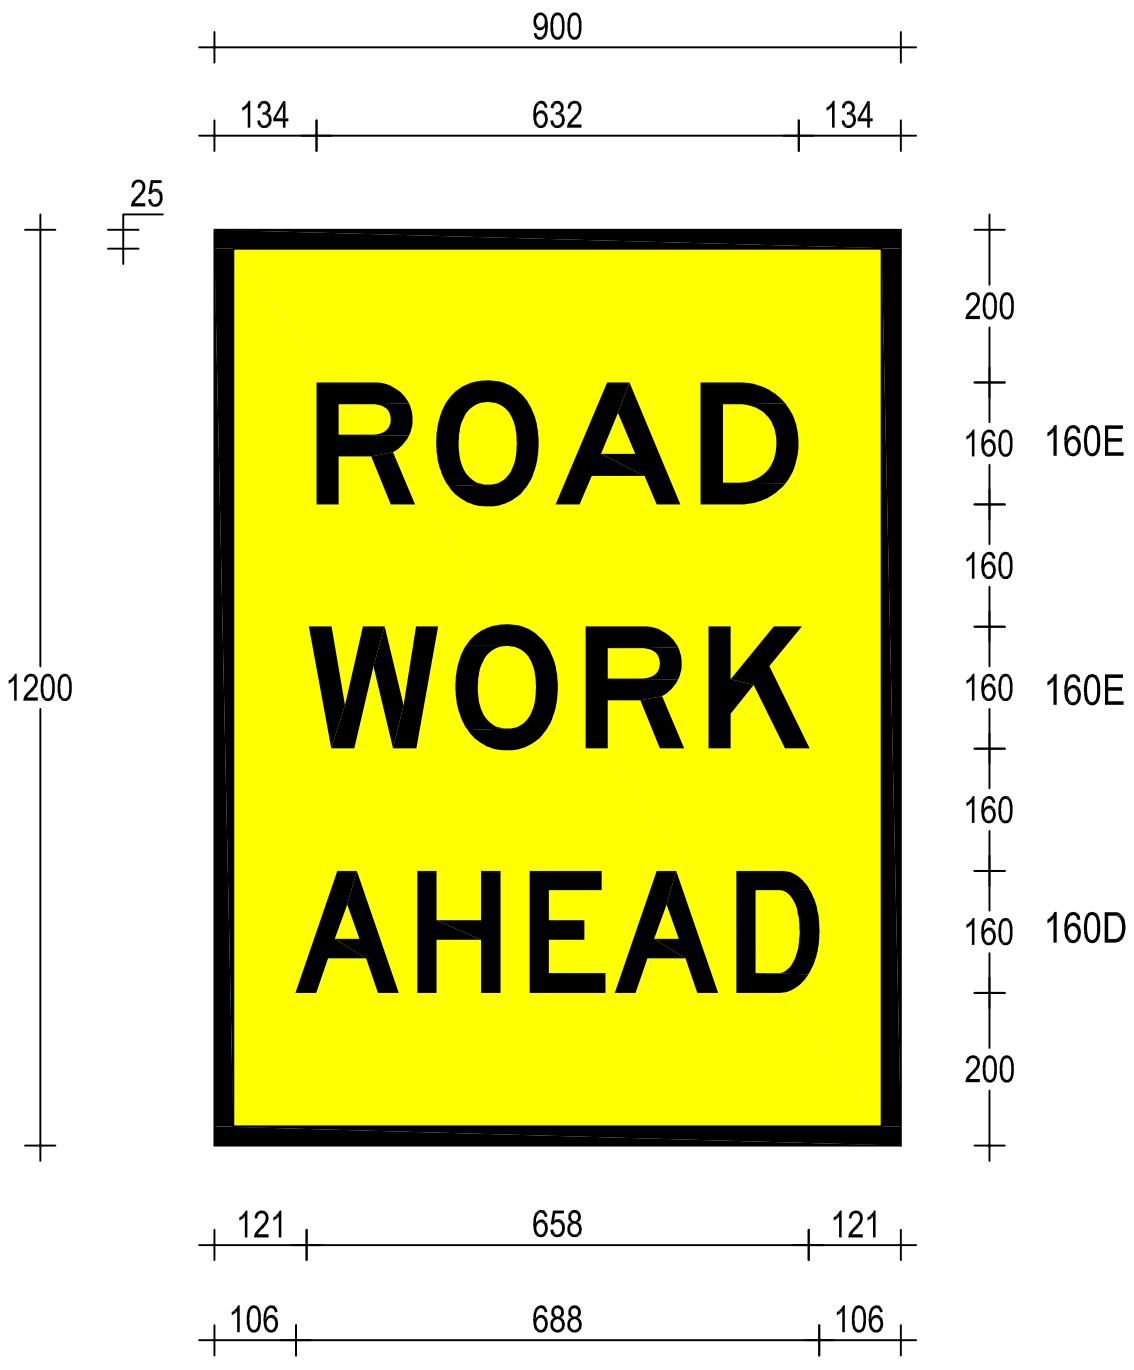


T1-31
900 x 1200

ACCEPTED FOR CONSTRUCTION

QR CODE	Scan to Check Document Version	REV	DATE	AMENDMENT / REVISION DESCRIPTION	APPROVAL
		01	23-08-18	AS Fonts & material classification revised	P.Oliver

DRAWING FILE LOCATION / NAME: H:\SIGNS\TTT\DRAWINGS\PLOT\TEMP\T1-31.DWG

MATERIALS: ALUMINIUM SIGN
BLACK LEGEND AND BORDER
ON AS1906.1 CL.400 YELLOW REFLECTORISED GROUND

ALL DIMENSIONS ARE IN MILLIMETRES UNLESS OTHERWISE SPECIFIED

SIGN TO BE MANUFACTURED IN ACCORDANCE WITH RMS QA SPECIFICATION 3400

DESIGNED
SIGNED
NAME M.Davies
DATE 12-07-19

REVIEWED
SIGNED
NAME J. Rozos
DATE 12-07-19

VERIFIED
SIGNED
NAME P.Oliver
TITLE Manager Guidance & Delineation
DATE 12-07-19

NSW GOVERNMENT Transport Roads & Maritime Services

PREPARED BY
GUIDANCE AND DELINEATION
TRAFFIC ENGINEERING SERVICES
TECHNICAL AND PROJECT SERVICES

TEMPORARY SIGN
T1-31
ROAD WORK AHEAD

A3

SHEET 1 OF 1

SCALE: 1:10	EDMS No. XXXXXXXXXX	SHEET No. 1	ISSUE 01

THIS DRAWING MAY BE PREPARED IN COLOUR AND MAY BE INCOMPLETE IF COPIED
50mm ON A3 SIZE ORIGINAL

© Roads and Maritime Services