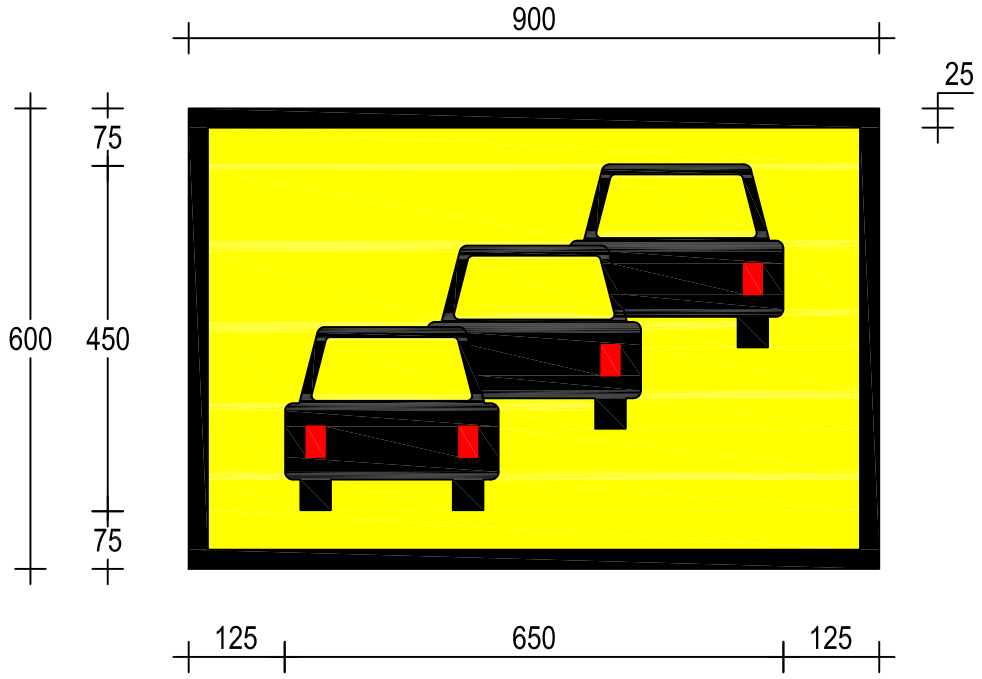
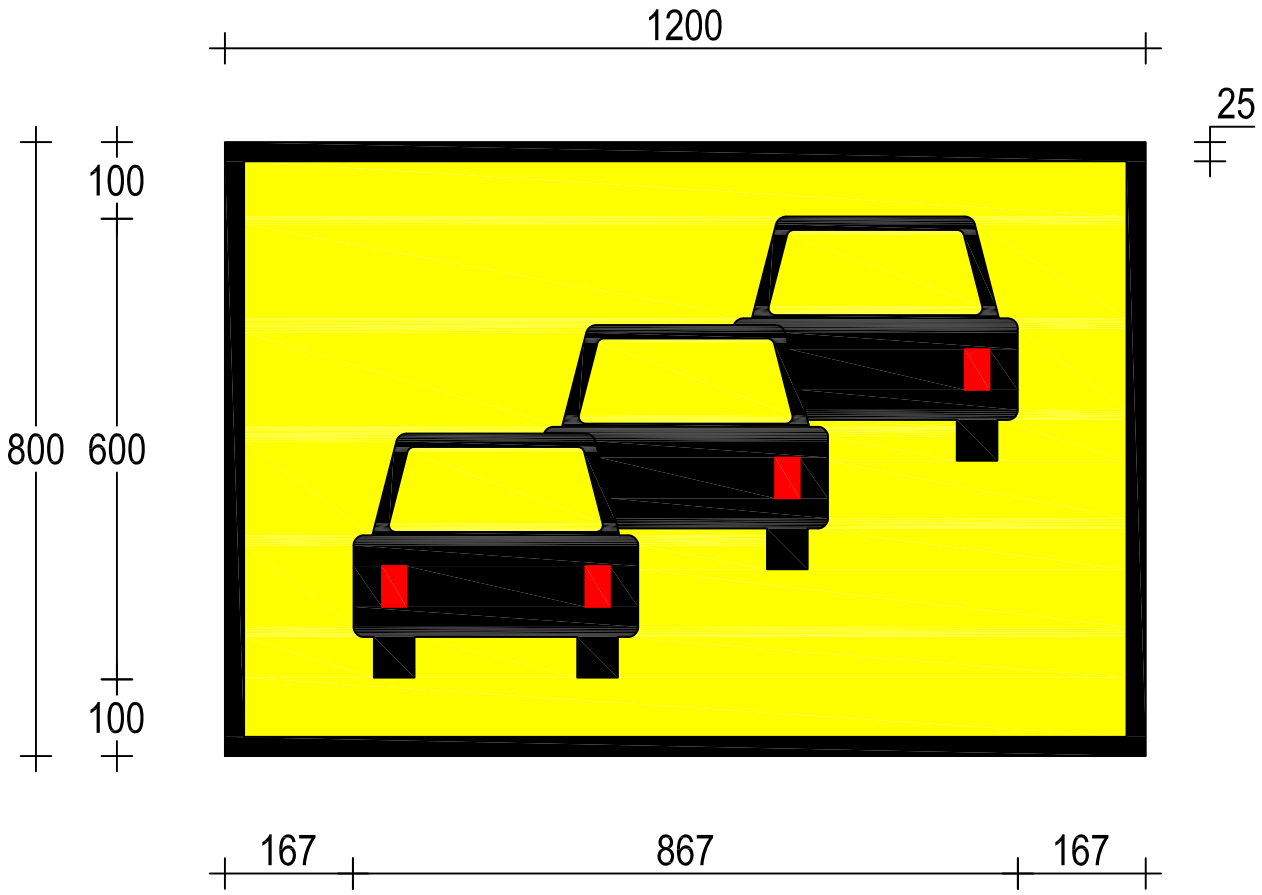
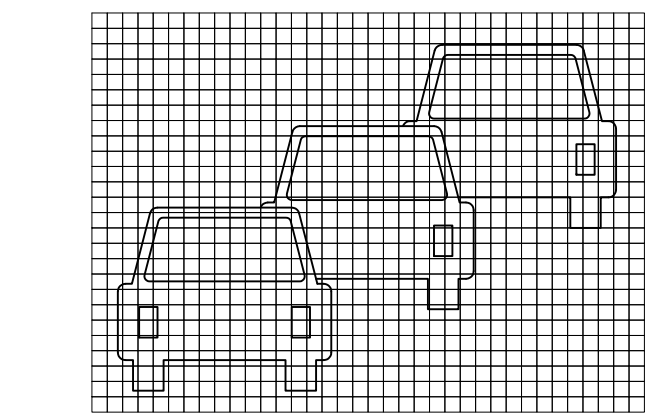


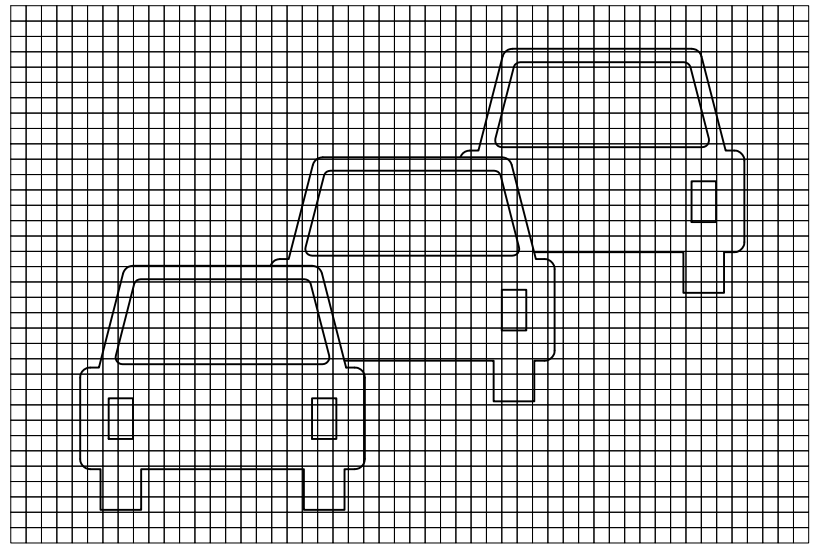

T1-47n(A)
900 x 600




T1-47n(B)
1200 x 800




Symbol Detail




Symbol Detail

ACCEPTED FOR CONSTRUCTION

| QR CODE | Scan to Check Document Version | REV | DATE | AMENDMENT / REVISION DESCRIPTION | APPROVAL |
|---|---|---|---|---|---|
| | | 01 | 23-08-18 | AS Fonts & material classification revised | P.Oliver |

DRAWING FILE LOCATION / NAME: H:\SIGNS\TTT\DRAWINGS\PLOT\TEMPORARY\T1-47nG

MATERIALS: ALUMINIUM SIGN
BLACK LEGEND AND BORDER
ON AS1906.1 CL.400 YELLOW REFLECTORISED GROUND
WITH CL.400 RED REFLECTORISED BACK LIGHTS

ALL DIMENSIONS ARE IN MILLIMETRES UNLESS OTHERWISE SPECIFIED

SIGN TO BE MANUFACTURED IN ACCORDANCE WITH RMS QA SPECIFICATION 3400

DESIGNED
NAME M.Davies
DATE 24-3-21

REVIEWED
NAME J.Rozos
DATE 24-03-21

VERIFIED
NAME P.Oliver
TITLE Manager Guidance & Delineation
DATE 24-03-21

Transport Roads & Maritime Services
NSW GOVERNMENT

PREPARED BY
GUIDANCE AND DELINEATION UNIT
ADVANCED TECHNICAL SERVICES
INFRASTRUCTURE AND PLACE

TEMPORARY SIGN
# T1-47n
QUEUED TRAFFIC

A3

SHEET 1 OF 1

SCALE: 1:10

EDMS No. XXXXXXXXXX

SHEET No. 1

ISSUE 01

THIS DRAWING MAY BE PREPARED IN COLOUR AND MAY BE INCOMPLETE IF COPIED
50mm ON A3 SIZE ORIGINAL
0 5 10 15 20 25 30 35 40 45 50

© Roads and Maritime Services