


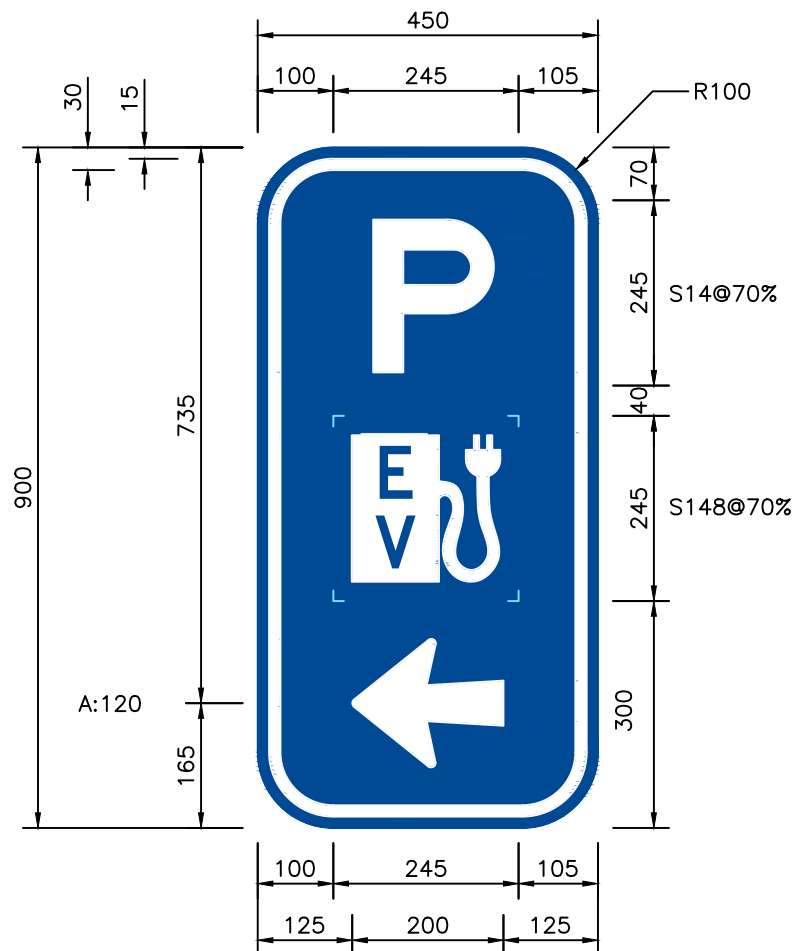

NOTES:

This service sign may be used to direct motorists to a car park space that has an Electric Vehicle recharge facility.

ADDITIONAL REFERENCE NOTES:

TES 14016 – Symbol detail sheet.

TES 12737(A Series) – Arrow detail sheet.



Blue class 400

White class 400

Note: Letters & Numerals AS1744:2015.



Government of South Australia
Department for Infrastructure and Transport

Road and Marine Services
Network Management Services, Traffic Solutions Unit

Drawn: M. Douglas

Scale: 1: 10

Authorisation:

Date: 8 April, 2024

GUIDE SIGN

'EV Electric Vehicle Parking – L or R'

G7-SA131
L or R