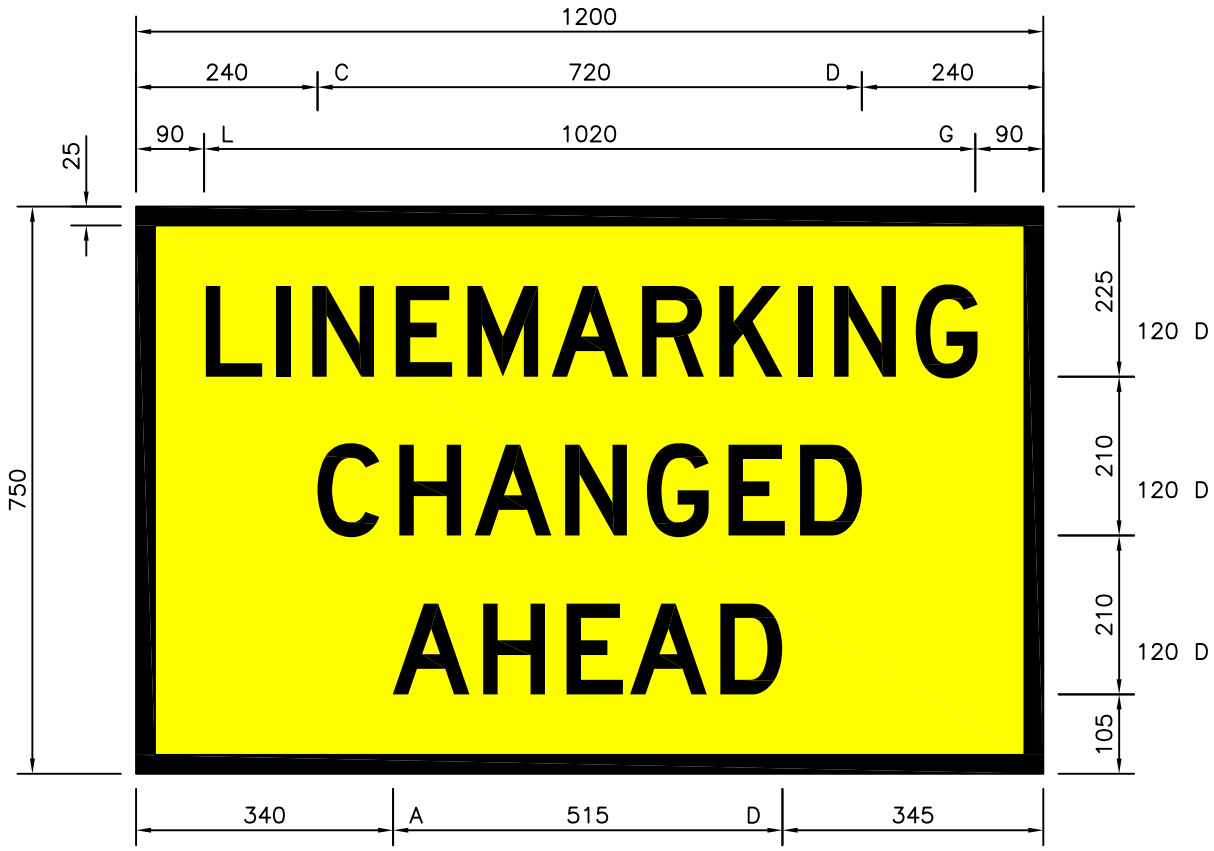

Yellow (retro–reflective)

Black

Note: Letters & Numerals AS1744:2015.

Government of South Australia
Department of Planning, Transport and Infrastructure

TEMPORARY WARNING SIGN
'Linemarking Changed Ahead'

Safety & Service Division
Technical Services Section

Authorisation:

Drawn: A. Simister

Scale: 1:10

Date: 10 May, 2017

T1-SA143