


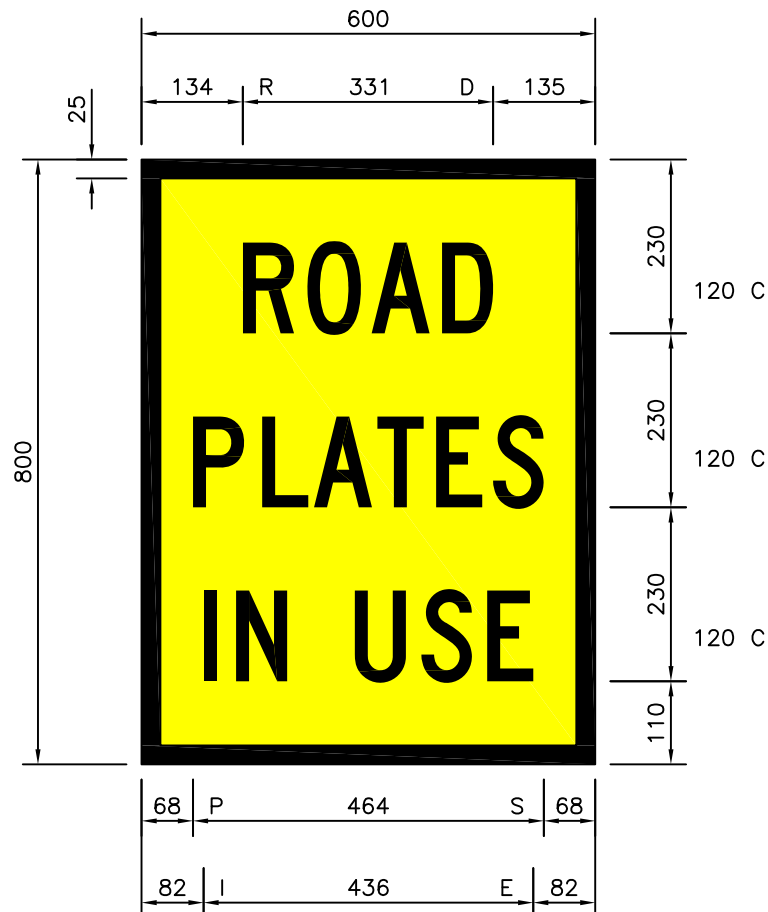

Yellow (retro-reflective)



Black

Note: Letters & Numerals AS1744:2015.



Government of South Australia
Department of Planning,
Transport and Infrastructure

TEMPORARY WARNING SIGN

'Road Plates In Use'

Safety & Service Division
Technical Services Section

Authorisation:

Date: 1 November, 2017

T4-SA108

Drawn: A. Simister

Scale: 1:10