


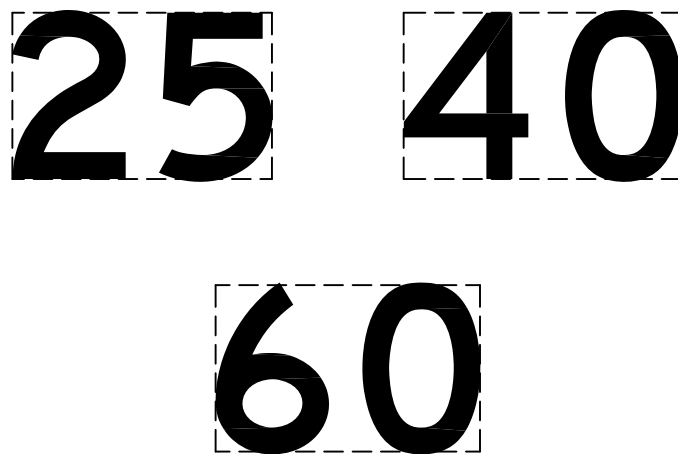

NOTE:
To be used in
multi-message sign frames
only.



Black

White class 1

Note: Letters & Numerals AS1744:2015.



Government of South Australia
Department of Planning,
Transport and Infrastructure

Road and Marine Services
Traffic Services, Traffic Solutions Unit

Drawn: A. Simister


Scale: 1:10

Authorisation:

Date: 8 January, 2020

REGULATORY SIGN
'Speed Limit – Ahead'

GM9-79D

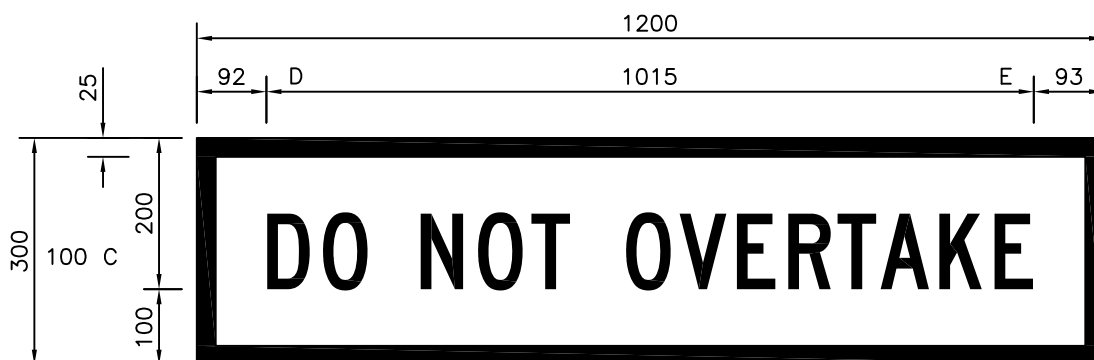

NOTE:

To be used in multi-message sign frames only.



Black

White class 1

Note: Letters & Numerals AS1744:2015.



Government of South Australia
Department of Planning,
Transport and Infrastructure

Road and Marine Services
Traffic Services, Traffic Solutions Unit

Drawn: A. Simister


Scale: 1:10

Authorisation:

Date: 8 January, 2020


GUIDE SIGN
'Do Not Overtake'

GM9-90B

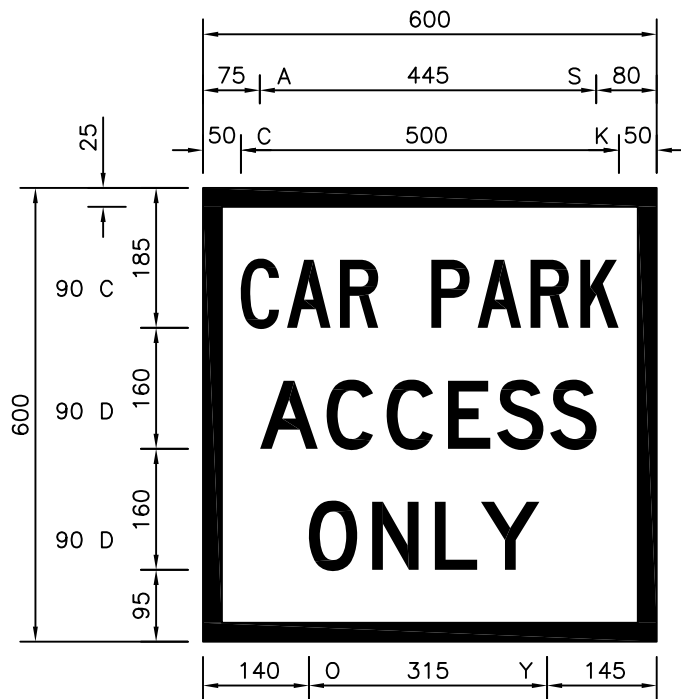

NOTE:

To be used in multi-message sign frames only.

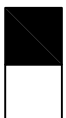

Black

White class 1

Note: Letters & Numerals AS1744:2015.



Government of South Australia
Department of Planning,
Transport and Infrastructure

Road and Marine Services
Traffic Services, Traffic Solutions Unit

Drawn: A. Simister

Scale: 1:10

Authorisation:


Date: 8 January, 2020

GUIDE SIGN

'Car Park Access Only'

GM9-SA130A

GM9-SA18A

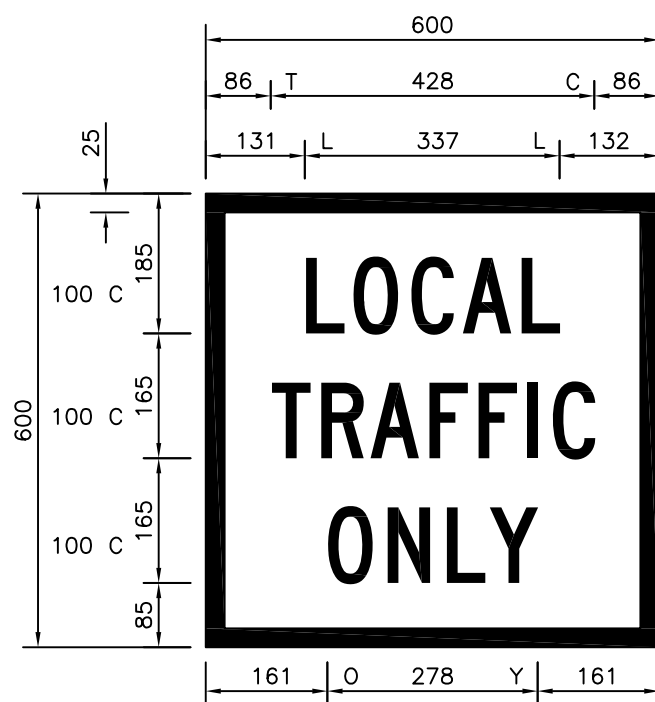

NOTE:

To be used in multi-message sign frames only.



Black

White class 1

Note: Letters & Numerals AS1744:2015.



Government of South Australia
Department of Planning,
Transport and Infrastructure

Road and Marine Services
Traffic Services, Traffic Solutions Unit

Drawn: A. Simister


Scale: 1:10

Authorisation:

Date: 8 January, 2020

GUIDE SIGN
'Local Traffic Only'

GM9-SA40A

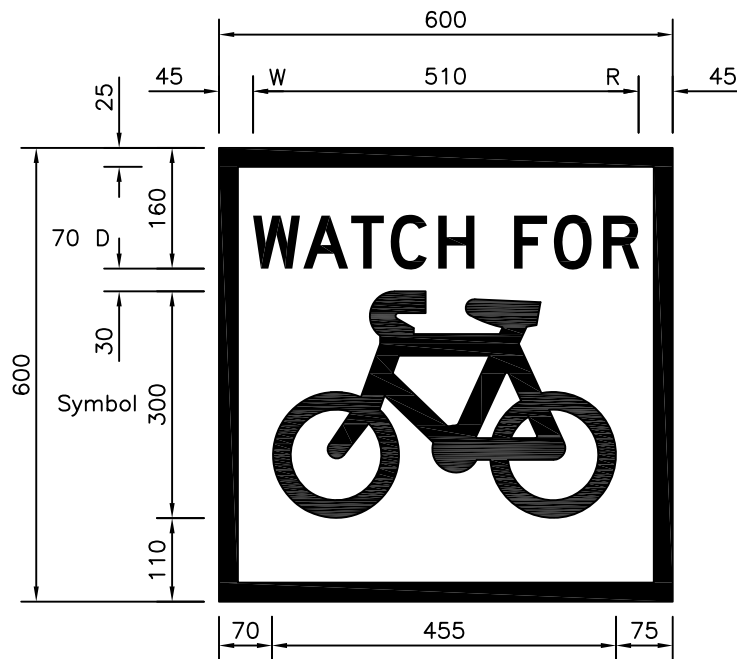

NOTE:

To be used in multi-message sign frames only.



Black

White class 1

Note: Letters & Numerals AS1744:2015.



Government of South Australia
Department of Planning,
Transport and Infrastructure

Road and Marine Services
Traffic Services, Traffic Solutions Unit

Drawn: A. Simister


Scale: 1:10

Authorisation:

Date: 8 January, 2020

GUIDE SIGN
'Watch for Bicycles

GM9-SA57A

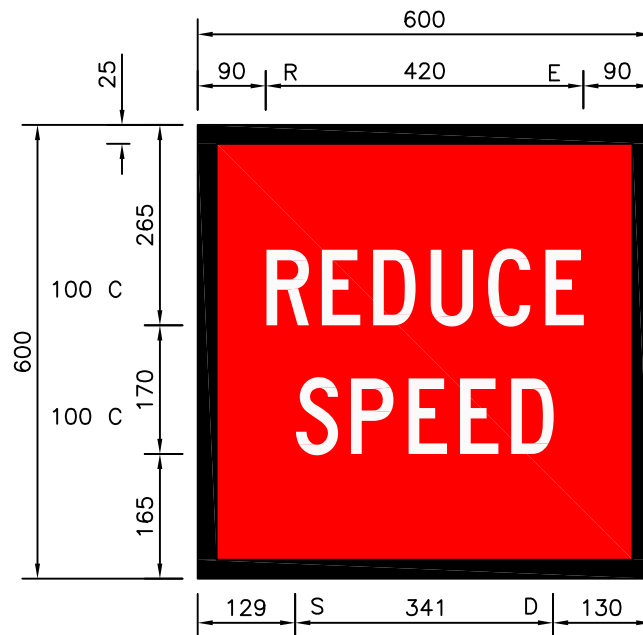

NOTE:

To be used in multi-message sign frames only.



Black

White Class 1

Red Class 1

Note: Letters & Numerals AS1744:2015.



Government of South Australia
Department of Planning,
Transport and Infrastructure

Road and Marine Services
Traffic Services, Traffic Solutions Unit

Drawn: A. Simister


Scale: 1:10

Authorisation:

Date: 8 January, 2020


TEMPORARY WARNING SIGN
'Reduce Speed'

GM9-SA9A

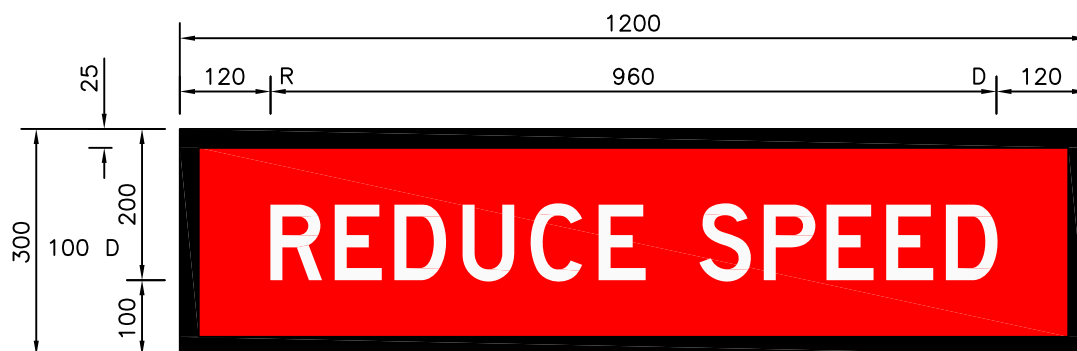

NOTE:

To be used in multi-message sign frames only.

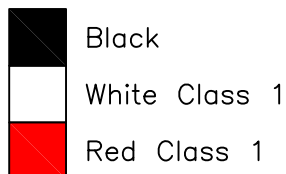

Note: Letters & Numerals AS1744:2015.



Government of South Australia
Department of Planning,
Transport and Infrastructure

Road and Marine Services
Traffic Services, Traffic Solutions Unit

Drawn: A. Simister


Scale: 1:10

Authorisation:


Date: 8 January, 2020

TEMPORARY WARNING SIGN
'Reduce Speed'

GM9-SA9B

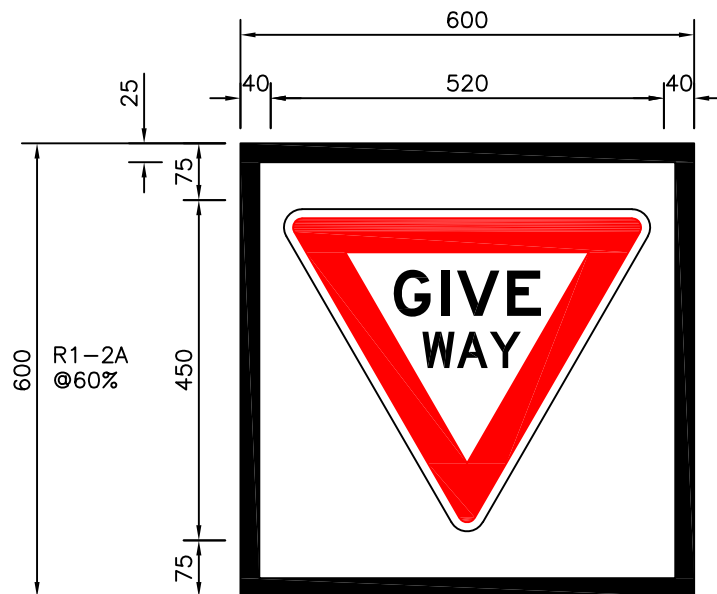


NOTE:
To be used in multi-message sign frames only.

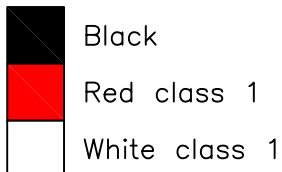

Note: Letters & Numerals AS1744:2015.

 Government of South Australia Department of Planning, Transport and Infrastructure	REGULATORY SIGN 'Give Way'		
Road and Marine Services Traffic Services, Traffic Solutions Unit		Authorisation: 	RM1-2A
Drawn: A. Simister	Scale: 1:10	Date: 8 January, 2020	

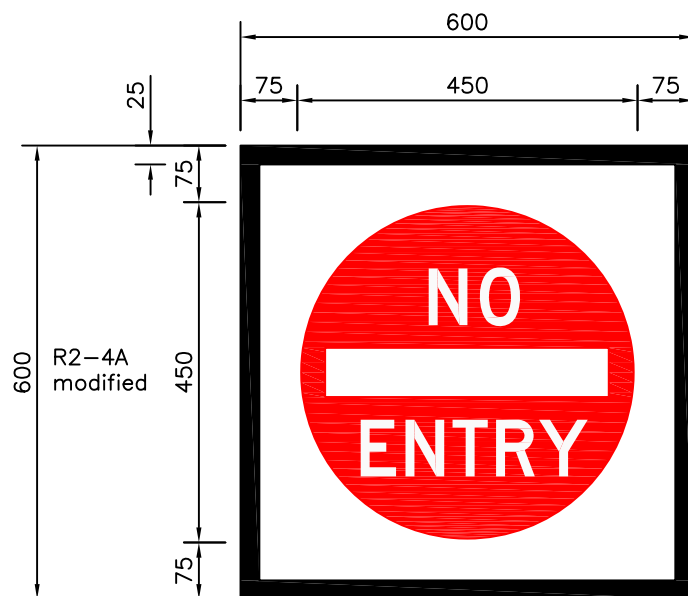

NOTE:

To be used in multi-message sign frames only.



Black

Red class 1

White class 1

Note: Letters & Numerals AS1744:2015.



Government of South Australia

Department of Planning,
Transport and Infrastructure

Road and Marine Services
Traffic Services, Traffic Solutions Unit

Drawn: A. Simister

Scale: 1:10


Authorisation:

Date: 8 January, 2020

REGULATORY SIGN

'No Entry'

RM2-4A

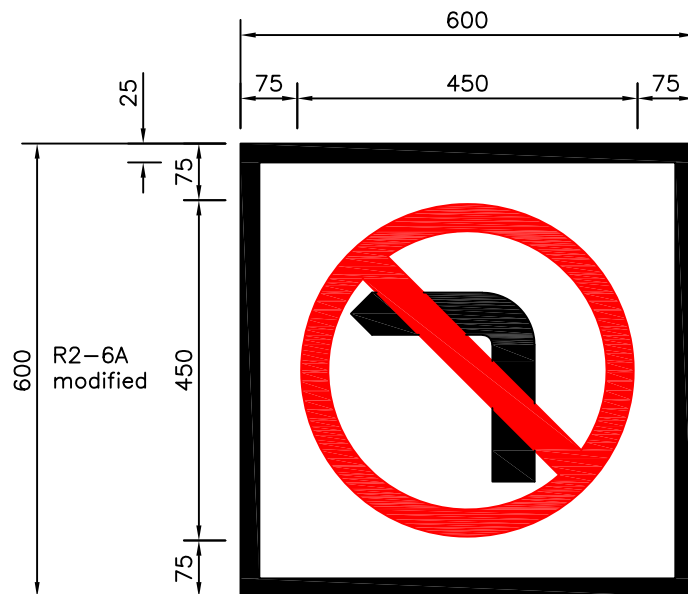

Dimensions apply for left or right construction.

NOTE:

To be used in multi-message sign frames only.



Black

Red class 1

White class 1

Note: Letters & Numerals AS1744:2015.



Government of South Australia
Department of Planning,
Transport and Infrastructure

Road and Marine Services
Traffic Services, Traffic Solutions Unit

Drawn: A. Simister


Scale: 1:10

Authorisation:

Date: 8 January, 2020

REGULATORY SIGN
'No Left Turn / No Right Turn'

RM2-6A

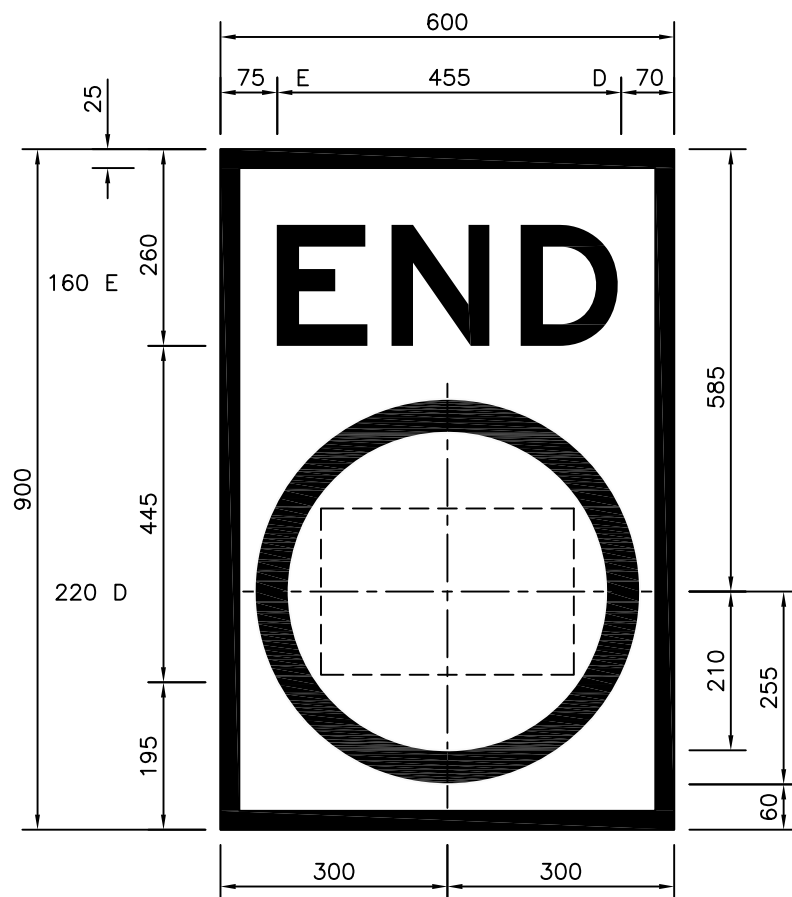

25 40

60



Black

White class 1

NOTE:

To be used in multi-message sign frames only.

Note: Letters & Numerals AS1744:2015.



Government of South Australia
Department of Planning,
Transport and Infrastructure

Road and Marine Services
Traffic Services, Traffic Solutions Unit

Drawn: A. Simister


Scale: 1:10

Authorisation:

Date: 20 December, 2019

REGULATORY SIGN
'End Speed Limit'

RM4-12D

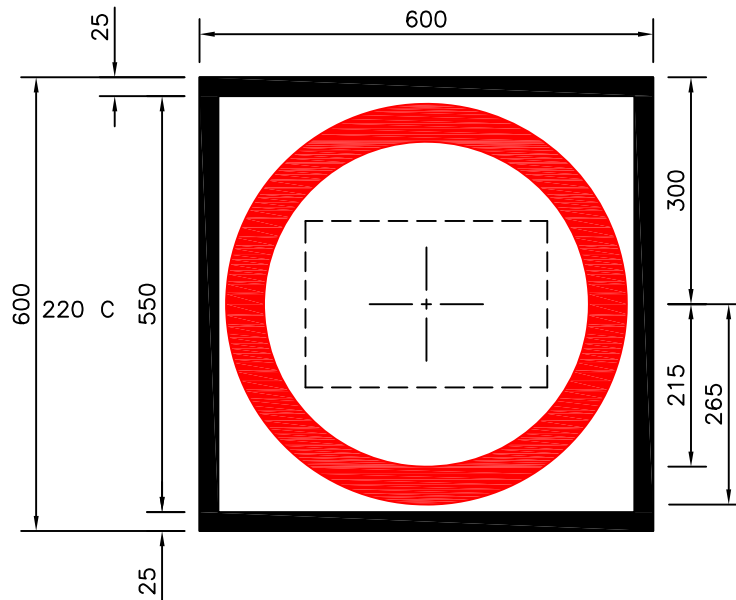

25

40

50

60

70

80

90

110

100

220 B



Black

Red class 1

White class 1

NOTE:

To be used in multi-message sign frames only.

Note: Letters & Numerals AS1744:2015.



Government of South Australia
Department of Planning,
Transport and Infrastructure

Road and Marine Services
Traffic Services, Traffic Solutions Unit

Drawn: A. Simister


Scale: 1:10

Authorisation:

Date: 9 January, 2020

REGULATORY SIGN
'Speed Restriction'

RM4-1A

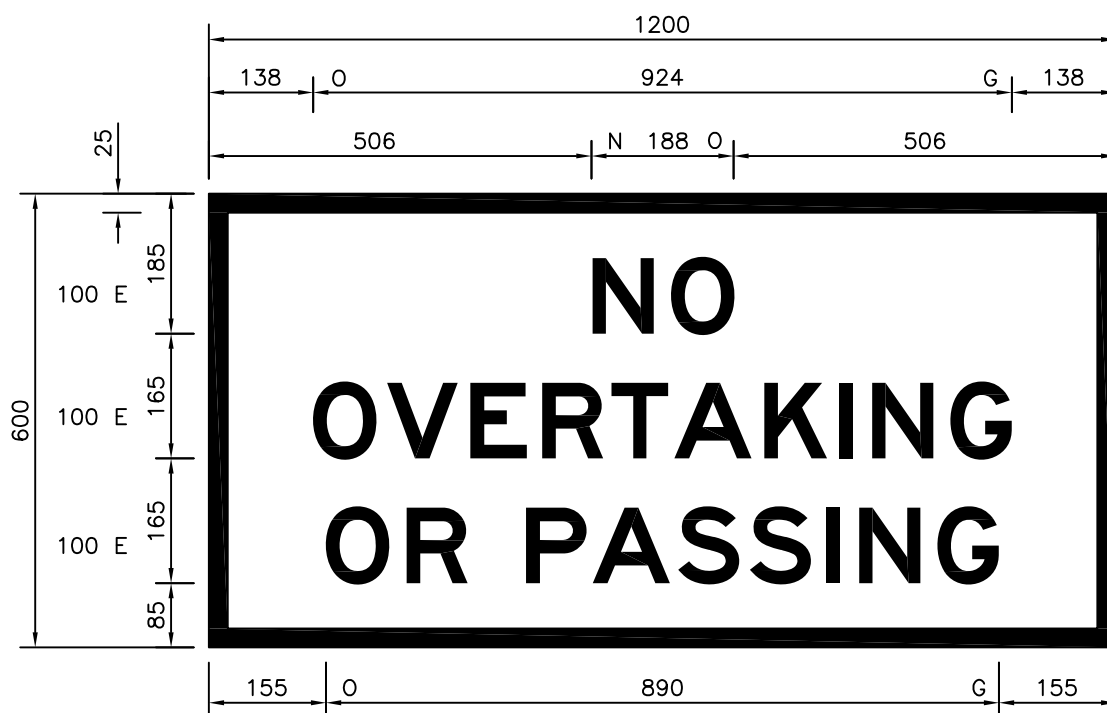

NOTE:

To be used in multi-message sign frames only.



Black

White class 1

Note: Letters & Numerals AS1744:2015.



Government of South Australia
Department of Planning,
Transport and Infrastructure

Road and Marine Services
Traffic Services, Traffic Solutions Unit

Drawn: A. Simister


Scale: 1:10

Authorisation:

Date: 8 January, 2020

TEMPORARY WARNING SIGN
'No Overtaking Or Passing'

RM6-1C

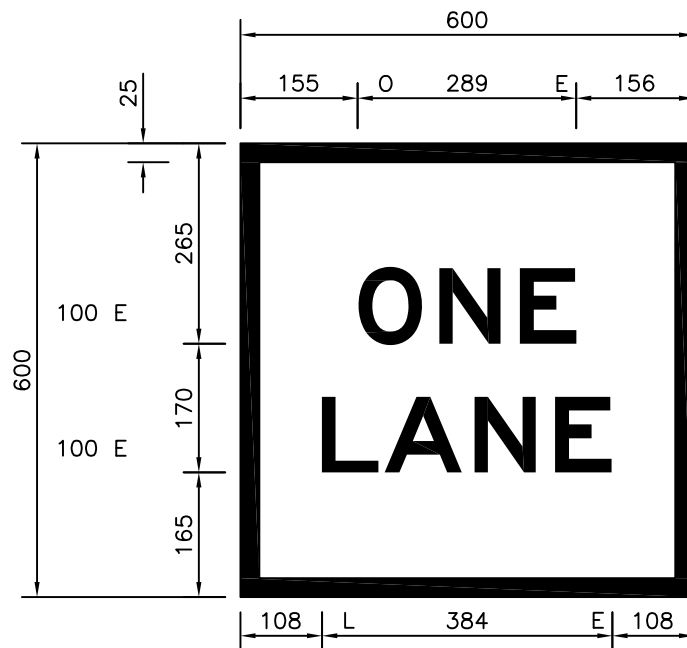

NOTE:

To be used in multi-message sign frames only.



Black

White class 1

Note: Letters & Numerals AS1744:2015.



Government of South Australia
Department of Planning,
Transport and Infrastructure

Road and Marine Services
Traffic Services, Traffic Solutions Unit

Drawn: A. Simister


Scale: 1:10

Authorisation:

Date: 8 January, 2020


REGULATORY SIGN
'One Lane'

RM9-9A

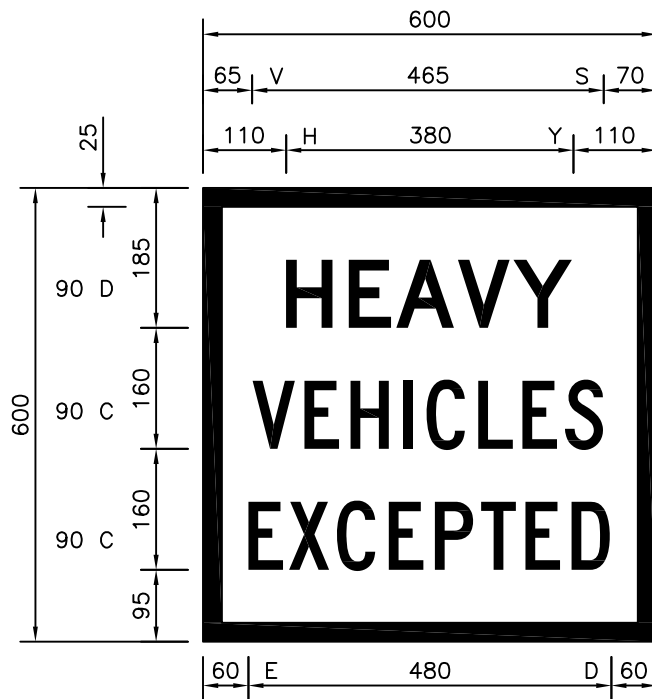

NOTE:

To be used in multi-message sign frames only.

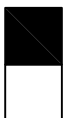

Black

White class 1

Note: Letters & Numerals AS1744:2015.



Government of South Australia
Department of Planning,
Transport and Infrastructure

Road and Marine Services
Traffic Services, Traffic Solutions Unit

Drawn: A. Simister

Scale: 1:10


Authorisation:

Date: 9 January, 2020

GUIDE SIGN

'Heavy Vehicles Excepted'

RM9-SA109A

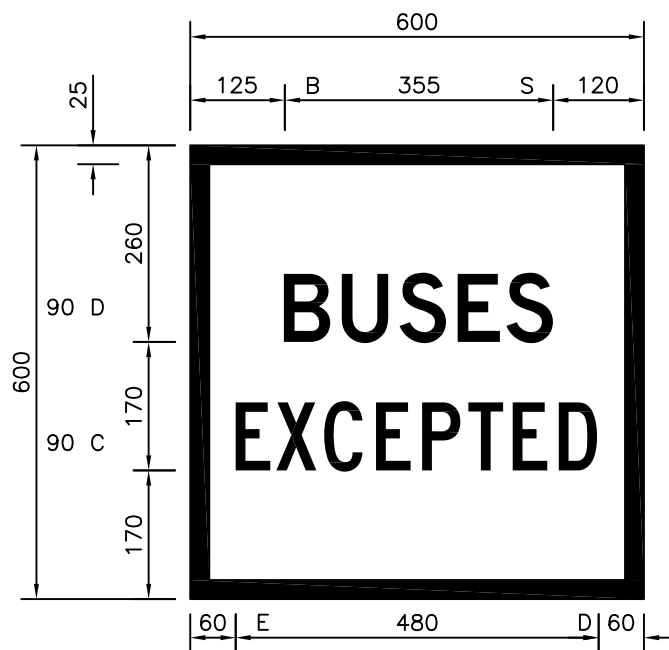

NOTE:

To be used in multi-message sign frames only.



Black

White class 1

Note: Letters & Numerals AS1744:2015.



Government of South Australia
Department of Planning,
Transport and Infrastructure

Road and Marine Services
Traffic Services, Traffic Solutions Unit

Drawn: A. Simister


Scale: 1:10

Authorisation:

Date: 9 January, 2020

REGULATORY SIGN
'Buses Excepted'

RM9-SA2A

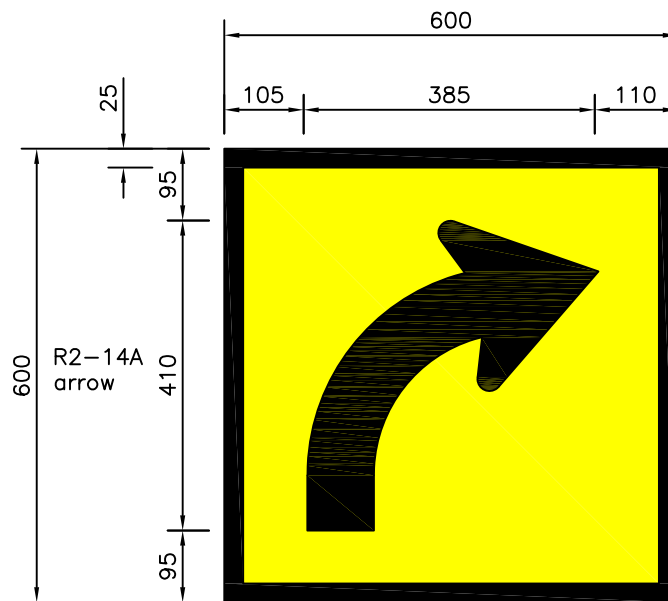

NOTE:
To be used in
multi-message sign frames
only.



Black

Yellow class 1

Note: Letters & Numerals AS1744:2015.



Government of South Australia
Department of Planning,
Transport and Infrastructure

Road and Marine Services
Traffic Services, Traffic Solutions Unit

Drawn: A. Simister


Scale: 1:10

Authorisation:


Date: 9 January, 2020

TEMPORARY WARNING SIGN
'Lane Status'

TM10-11A

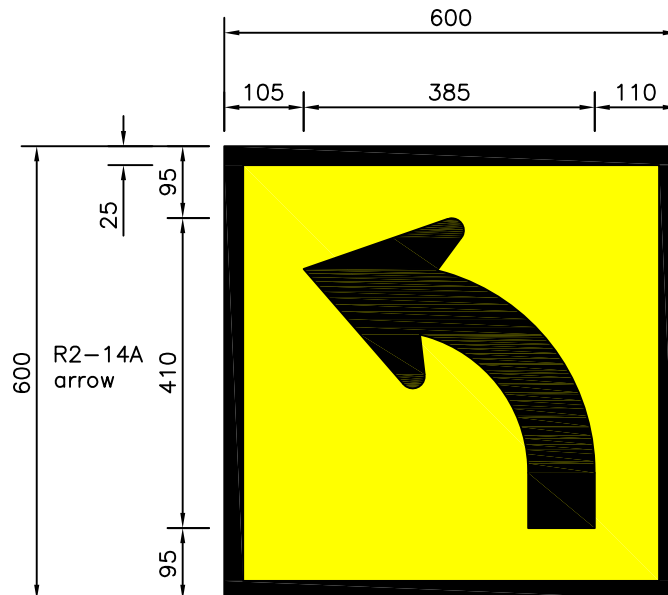


NOTE:
To be used in multi-message sign frames only.

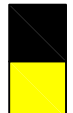

Black
Yellow class 1

Note: Letters & Numerals AS1744:2015.



 Government of South Australia Department of Planning, Transport and Infrastructure	TEMPORARY WARNING SIGN 'Lane Status'		
Road and Marine Services Traffic Services, Traffic Solutions Unit	Authorisation: 	TM10-12A	
Drawn: A. Simister	Scale: 1:10	Date: 9 January, 2020	

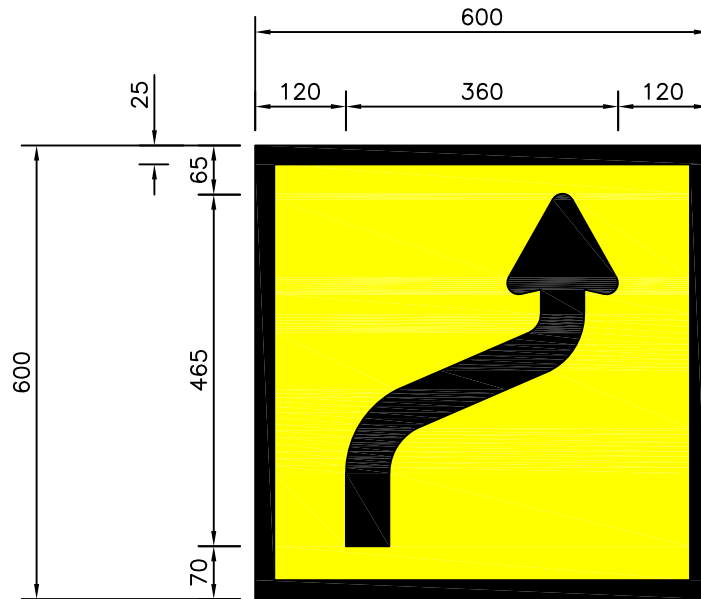

NOTE:

To be used in multi-message sign frames only.

ARROW DETAILS

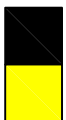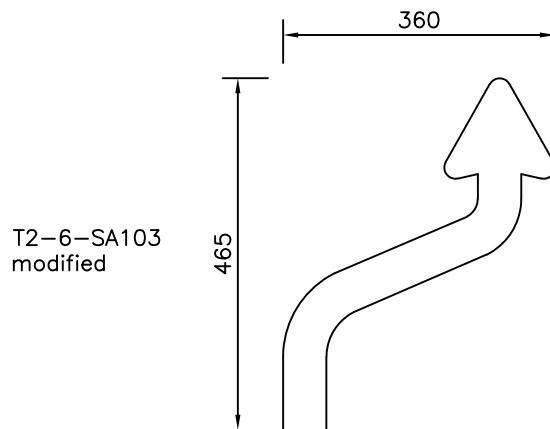

Black

Yellow class 1

Note: Letters & Numerals AS1744:2015.



Government of South Australia
Department of Planning,
Transport and Infrastructure

Road and Marine Services
Traffic Services, Traffic Solutions Unit

Drawn: A. Simister


Scale: 1:10

Authorisation:

Date: 9 January, 2020



TEMPORARY WARNING SIGN
'Lane Status'

TM10-16A

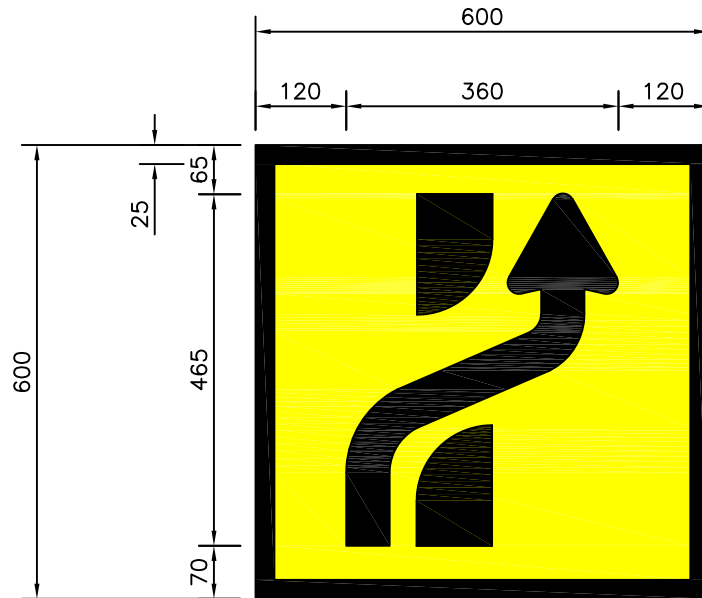

NOTE:
To be used in
multi-message sign frames
only.

ARROW DETAILS

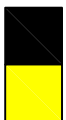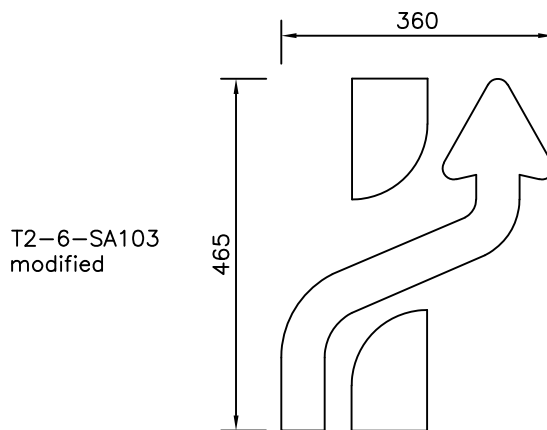

Black

Yellow class 1

Note: Letters & Numerals AS1744:2015.



Government of South Australia
Department of Planning,
Transport and Infrastructure

Road and Marine Services
Traffic Services, Traffic Solutions Unit

Drawn: A. Simister


Scale: 1:10

Authorisation:

Date: 9 January, 2020


TEMPORARY WARNING SIGN
'Lane Status – Through Median'

TM10-17A

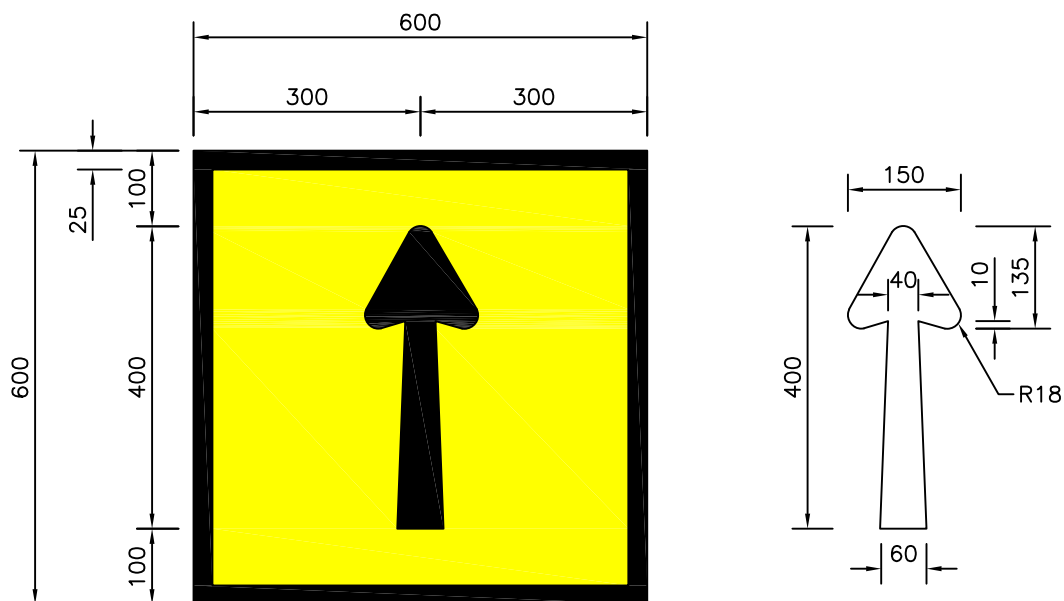

NOTE:

To be used in
multi-message sign frames
only.

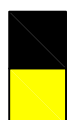

Black

Yellow class 1

Note: Letters & Numerals AS1744:2015.



Government of South Australia
Department of Planning,
Transport and Infrastructure

Road and Marine Services
Traffic Services, Traffic Solutions Unit

Drawn: A. Simister


Scale: 1:10

Authorisation:

Date: 9 January, 2020

TEMPORARY WARNING SIGN
'Lane Through Ahead'

TM10-1A

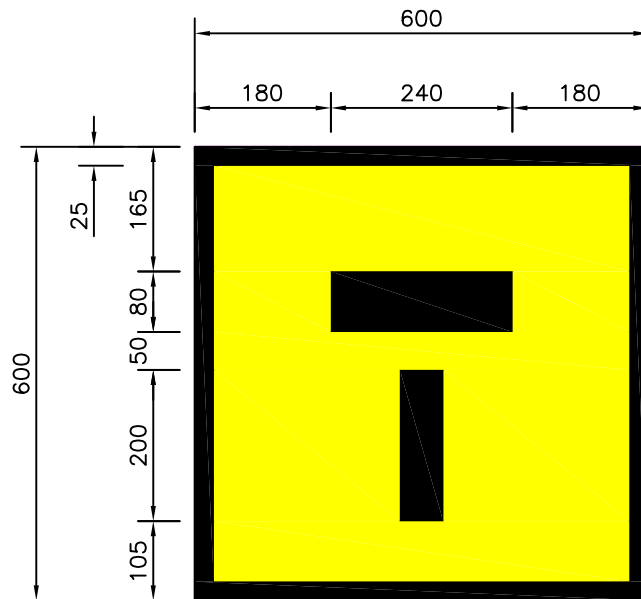

NOTE:

To be used in
multi-message sign frames
only.



Black

Yellow class 1

Note: Letters & Numerals AS1744:2015.



Government of South Australia
Department of Planning,
Transport and Infrastructure

Road and Marine Services
Traffic Services, Traffic Solutions Unit

Drawn: A. Simister



Scale: 1:10

Authorisation:

Date: 9 January, 2020

TEMPORARY WARNING SIGN
'Lane Closed Ahead'

TM10-2A

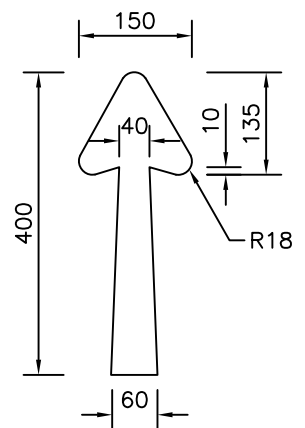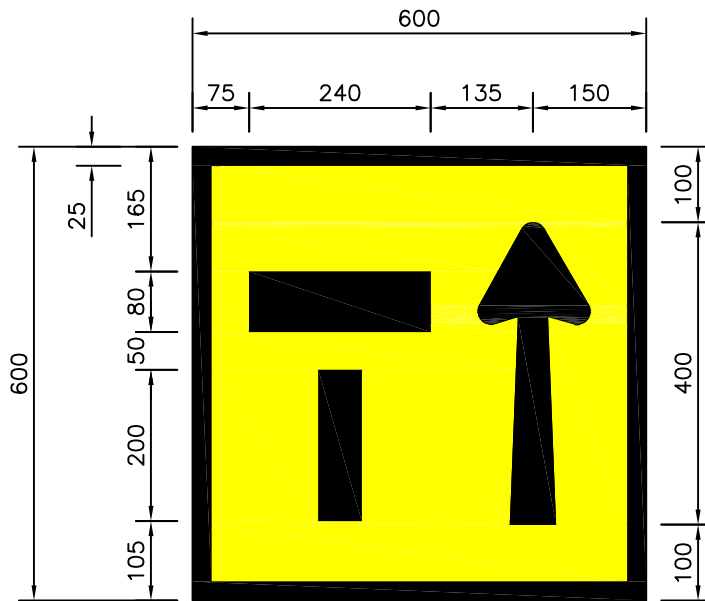

NOTE:
To be used in
multi-message sign frames
only.



Black

Yellow class 1

Note: Letters & Numerals AS1744:2015.



Government of South Australia
Department of Planning,
Transport and Infrastructure

Road and Marine Services
Traffic Services, Traffic Solutions Unit

Drawn: A. Simister



Scale: 1:10

Authorisation:

Date: 9 January, 2020

TEMPORARY WARNING SIGN
'Left Lane of Two Lane Closed'

TM10-3A

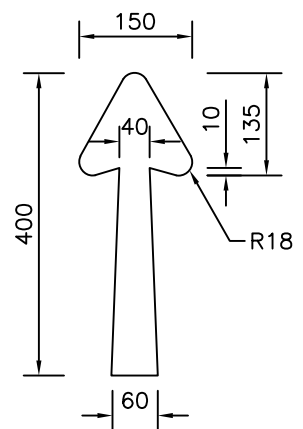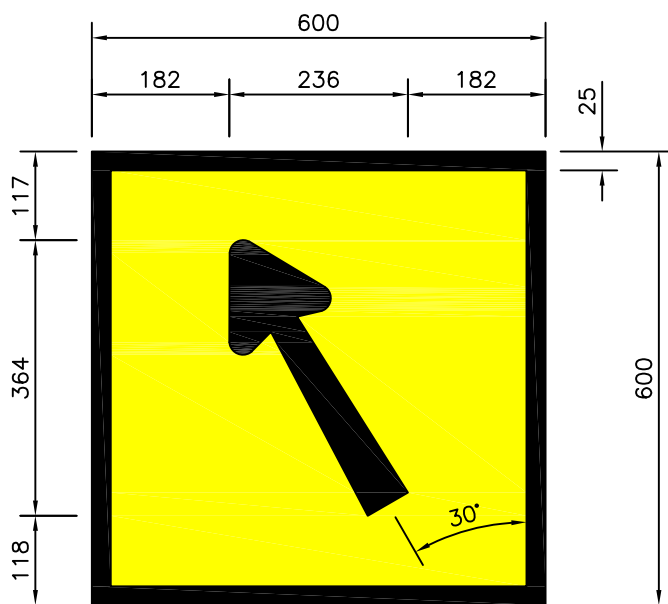

NOTE:

To be used in multi-message sign frames only.



Black

Yellow class 1

Note: Letters & Numerals AS1744:2015.



Government of South Australia
Department of Planning,
Transport and Infrastructure

Road and Marine Services
Traffic Services, Traffic Solutions Unit

Drawn: A. Simister



Scale: 1:10

Authorisation:


Date: 9 January, 2020

TEMPORARY WARNING SIGN
'Merge Left'

TM10-SA111A

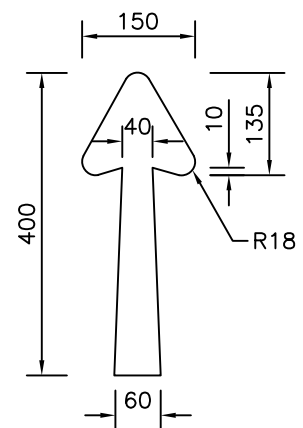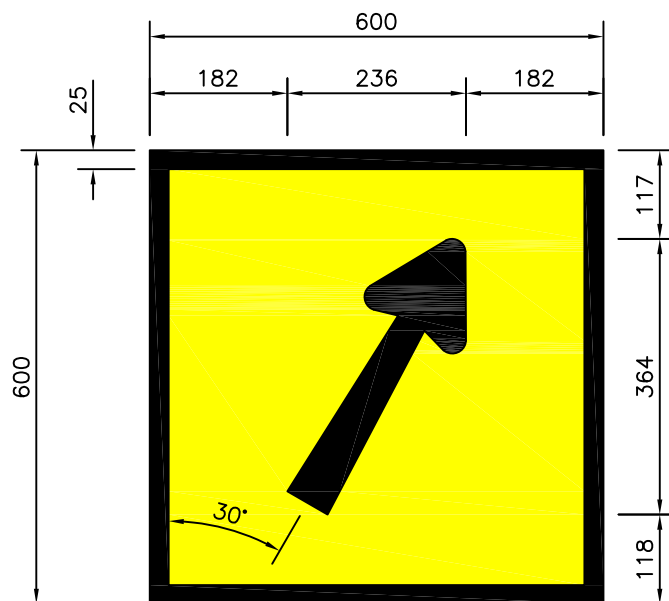

NOTE:
To be used in multi-message
sign frames only.

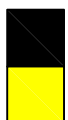

Black

Yellow class 1

Note: Letters & Numerals AS1744:2015.



Government of South Australia
Department of Planning,
Transport and Infrastructure

Road and Marine Services
Traffic Services, Traffic Solutions Unit

Drawn: A. Simister



Scale: 1:10

Authorisation:

Date: 9 January, 2020

TEMPORARY WARNING SIGN
'Merge Right'

TM10-SA112A

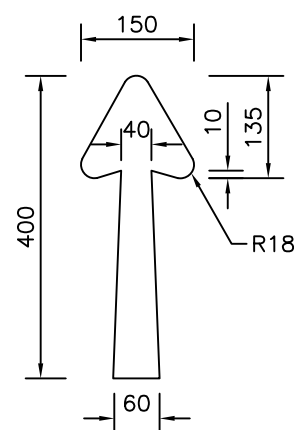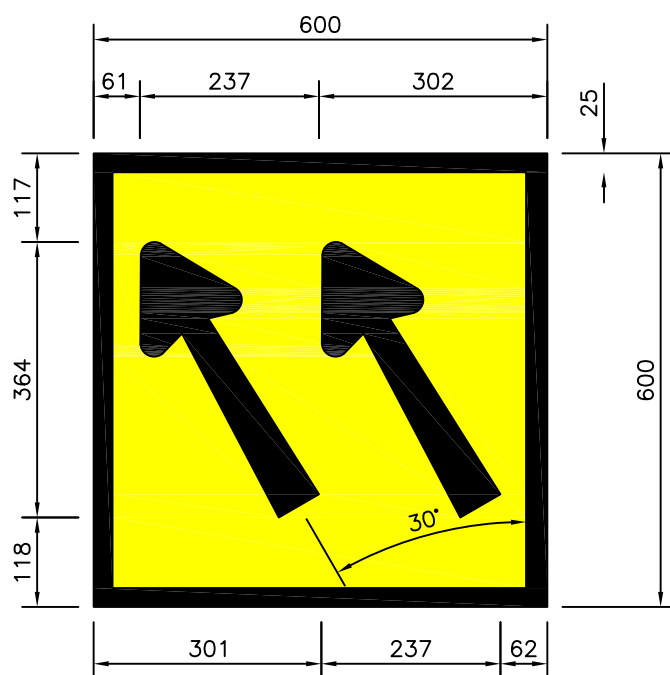

NOTE:

To be used in multi-message sign frames only.



Black

Yellow class 1

Note: Letters & Numerals AS1744:2015.



Government of South Australia
Department of Planning,
Transport and Infrastructure

Road and Marine Services
Traffic Services, Traffic Solutions Unit

Drawn: A. Simister



Scale: 1:10

Authorisation:

Date: 9 January, 2020

TEMPORARY WARNING SIGN
'Lateral Shift Left – 2 Lanes'

TM10-SA113A

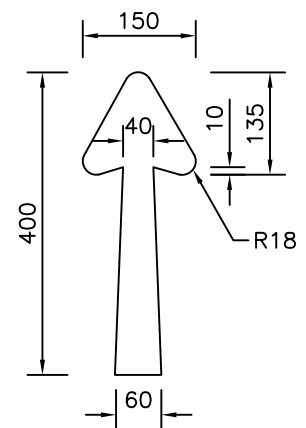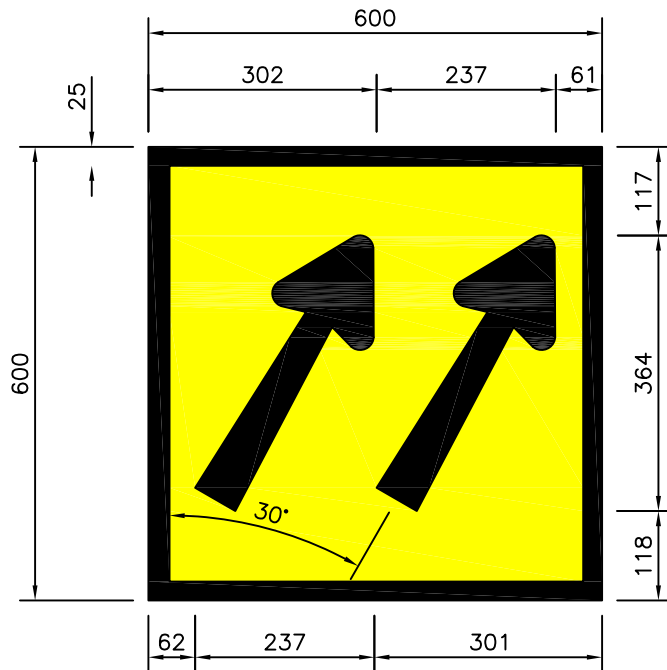

NOTE:

To be used in multi-message sign frames only.



Black

Yellow class 1

Note: Letters & Numerals AS1744:2015.



Government of South Australia
Department of Planning,
Transport and Infrastructure

Road and Marine Services
Traffic Services, Traffic Solutions Unit

Drawn: A. Simister


Scale: 1:10

Authorisation:

Date: 9 January, 2020

TEMPORARY WARNING SIGN
'Lateral Shift Right – 2 Lanes'

TM10-SA114A

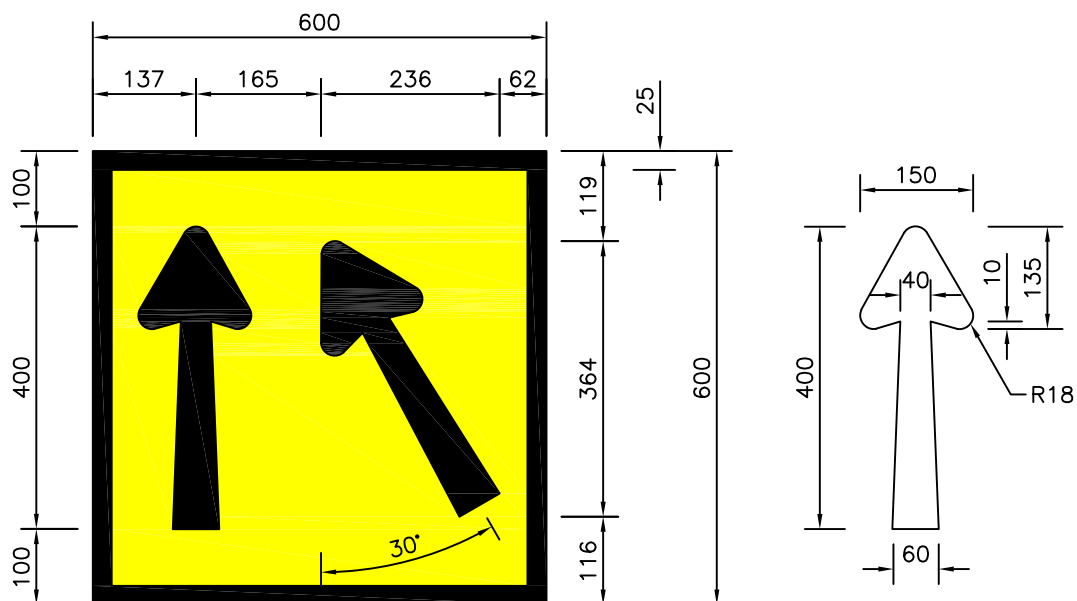

NOTE:
To be used in multi-message
sign frames only.



Black

Yellow class 1

Note: Letters & Numerals AS1744:2015.



Government of South Australia
Department of Planning,
Transport and Infrastructure

Road and Marine Services
Traffic Services, Traffic Solutions Unit

Drawn: A. Simister


Scale: 1:10

Authorisation:


Date: 9 January, 2020

TEMPORARY WARNING SIGN
'Merge Left - Right Lane'

TM10-SA115A

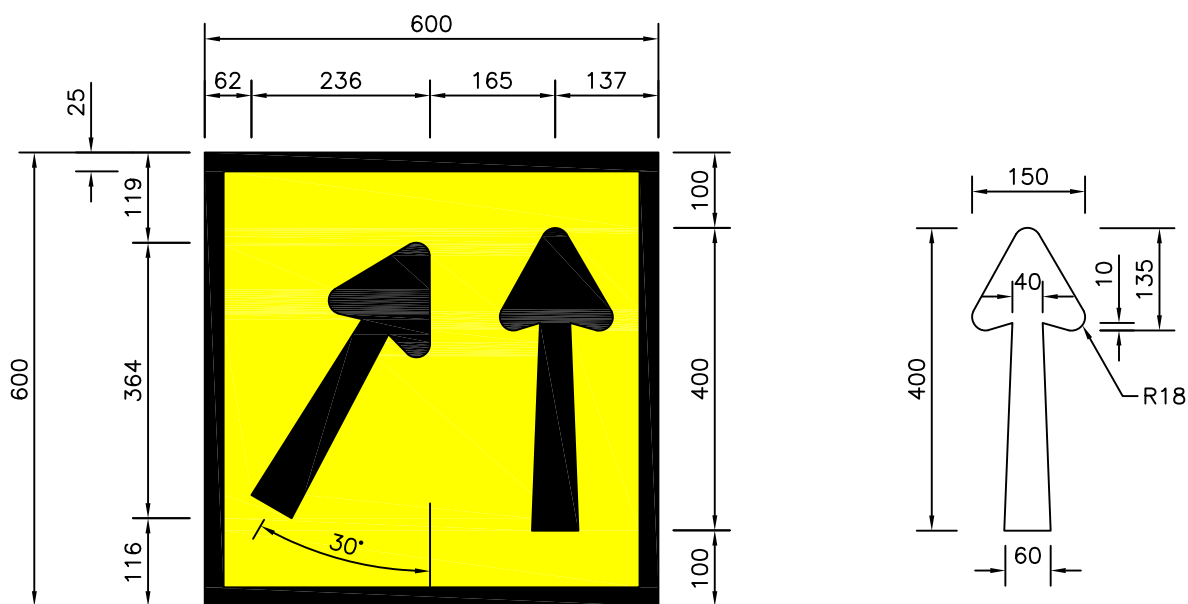


NOTE:
To be used in multi-message
sign frames only.

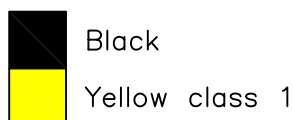


Note: Letters & Numerals AS1744:2015.

 Government of South Australia Department of Planning, Transport and Infrastructure	TEMPORARY WARNING SIGN 'Merge Right - Left Lane'		
Road and Marine Services Traffic Services, Traffic Solutions Unit		Authorisation: 	TM10-SA116A
Drawn: A. Simister	Scale: 1:10	Date: 9 January, 2020	

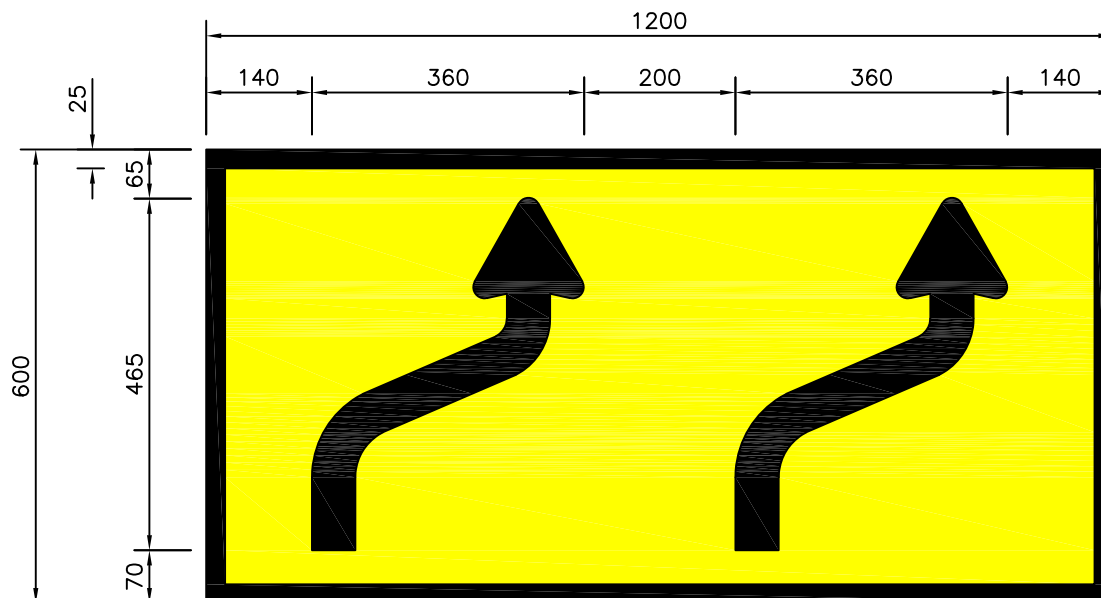

NOTE:

To be used in multi-message sign frames only.

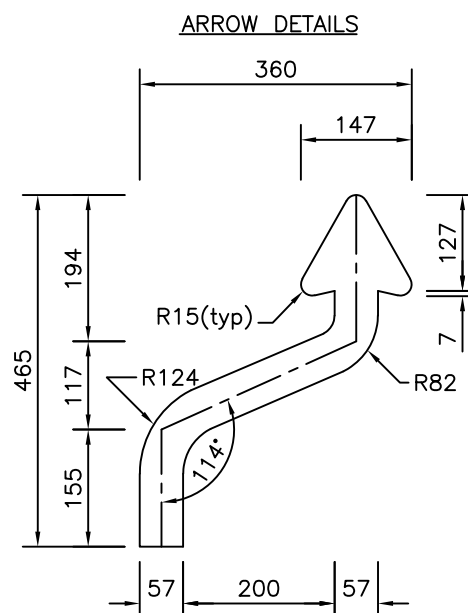

Black

Yellow class 1

Note: Letters & Numerals AS1744:2015.



Government of South Australia
Department of Planning,
Transport and Infrastructure

Road and Marine Services
Traffic Services, Traffic Solutions Unit

Drawn: A. Simister


Scale: 1:10

Authorisation:

Date: 9 January, 2019

TEMPORARY WARNING SIGN
'Lanes Status'

TM10-SA14C

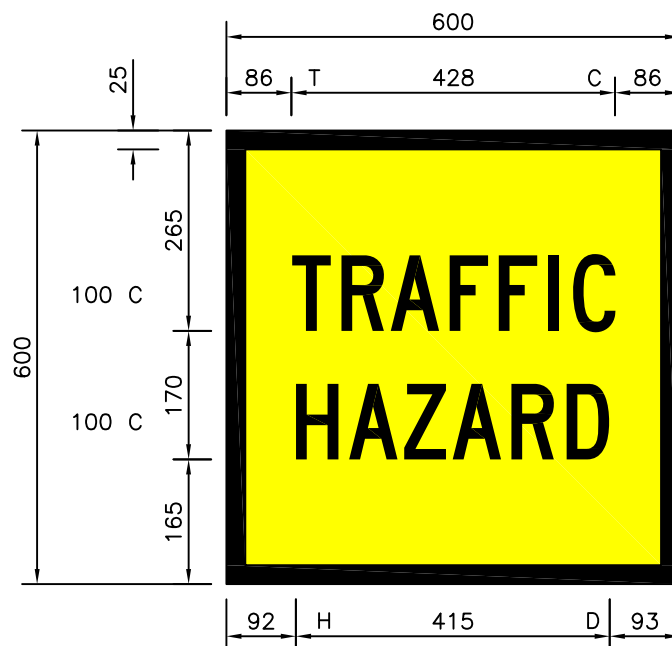

NOTE:

To be used in multi-message sign frames only.



Black

Yellow class 1

Note: Letters & Numerals AS1744:2015.



Government of South Australia
Department of Planning,
Transport and Infrastructure

Road and Marine Services
Traffic Services, Traffic Solutions Unit

Drawn: A. Simister


Scale: 1:10

Authorisation:

Date: 9 January, 2020


TEMPORARY WARNING SIGN
'Traffic Hazard'

TM1-10A

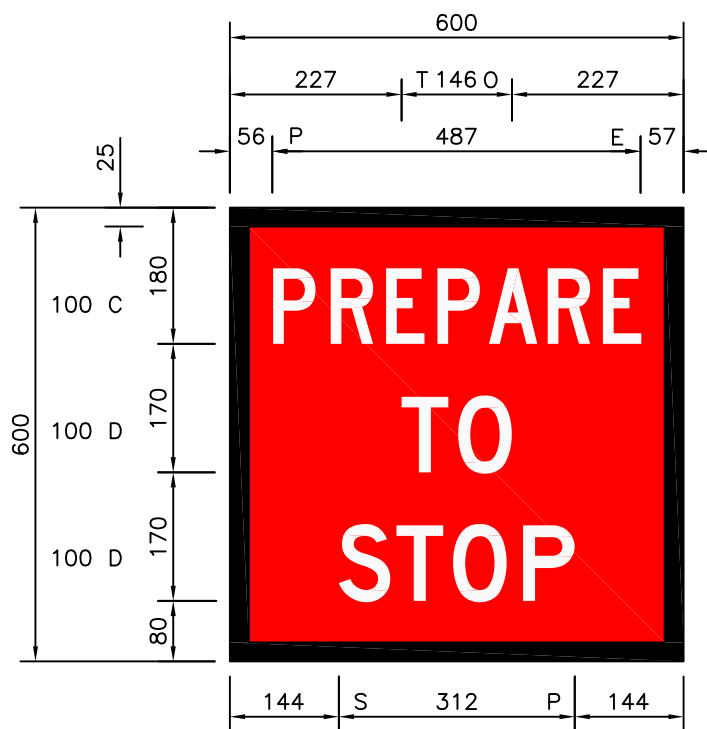

NOTE:

To be used in multi-message sign frames only.

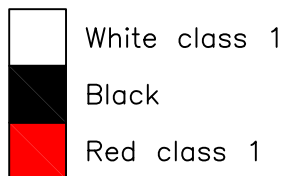

Note: Letters & Numerals AS1744:2015.



Government of South Australia
Department of Planning,
Transport and Infrastructure

Road and Marine Services
Traffic Services, Traffic Solutions Unit

Drawn: A. Simister


Scale: 1:10

Authorisation:

Date: 9 January, 2020

TEMPORARY WARNING SIGN
'Prepare To Stop'

TM1-18A

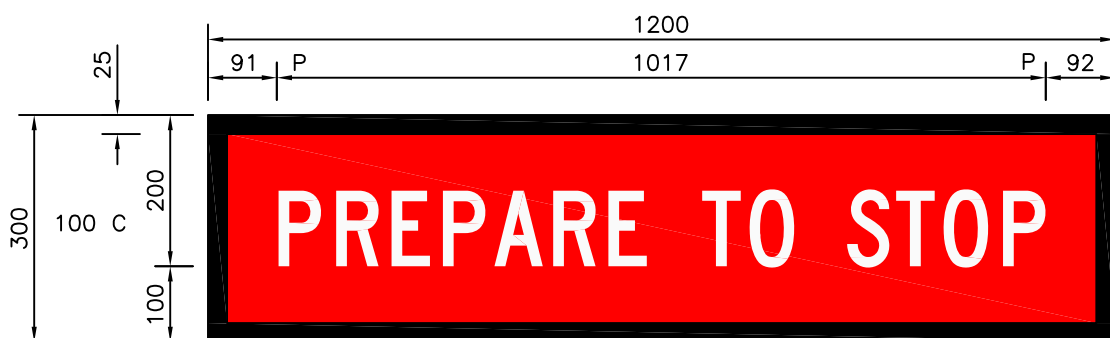

NOTE:

To be used in multi-message sign frames only.



Black

Red class 1

White class 1

Note: Letters & Numerals AS1744:2015.



Government of South Australia

Department of Planning,
Transport and Infrastructure

Road and Marine Services
Traffic Services, Traffic Solutions Unit

Drawn: A. Simister


Scale: 1:10

Authorisation:

Date: 9 January, 2020

TEMPORARY WARNING SIGN
'Prepare To Stop'

TM1-18B

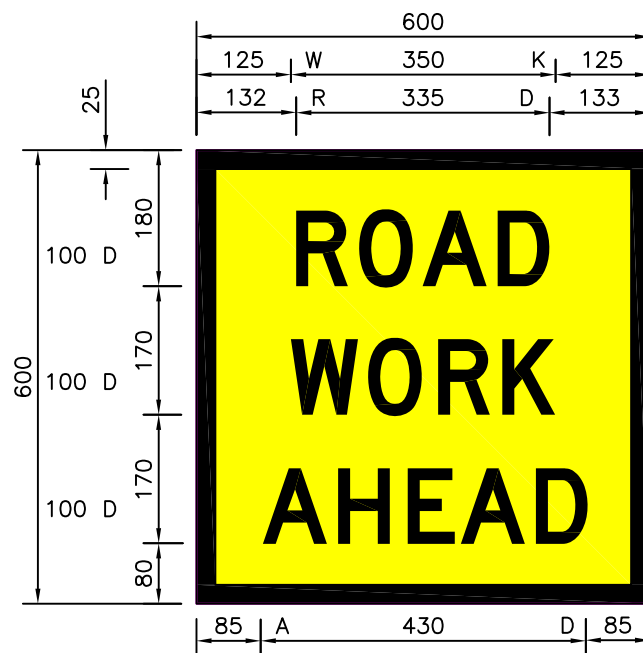

NOTE:

To be used in multi-message sign frames only.



Black

Yellow class 1

Note: Letters & Numerals AS1744:2015.



Government of South Australia
Department of Planning,
Transport and Infrastructure

Road and Marine Services
Traffic Services, Traffic Solutions Unit

Drawn: A. Simister

Scale: 1:10


Authorisation:

Signature of the authorising officer.

Date: 9 January, 2020


TEMPORARY WARNING SIGN
'Road Work Ahead'

TM1-1A

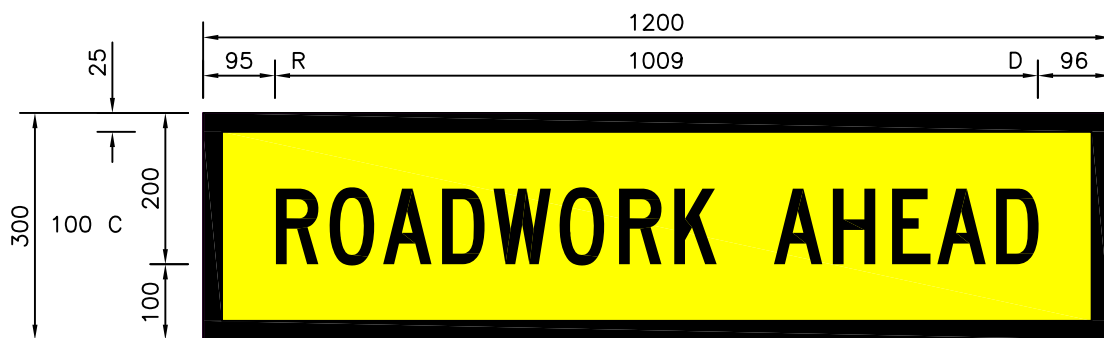

NOTE:

To be used in multi-message sign frames only.

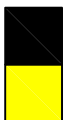

Black

Yellow class 1

Note: Letters & Numerals AS1744:2015.



Government of South Australia
Department of Planning,
Transport and Infrastructure

Road and Marine Services
Traffic Services, Traffic Solutions Unit

Drawn: A. Simister


Scale: 1:10

Authorisation:

Date: 9 January, 2020

TEMPORARY WARNING SIGN
'Roadwork Ahead'

TM1-1B

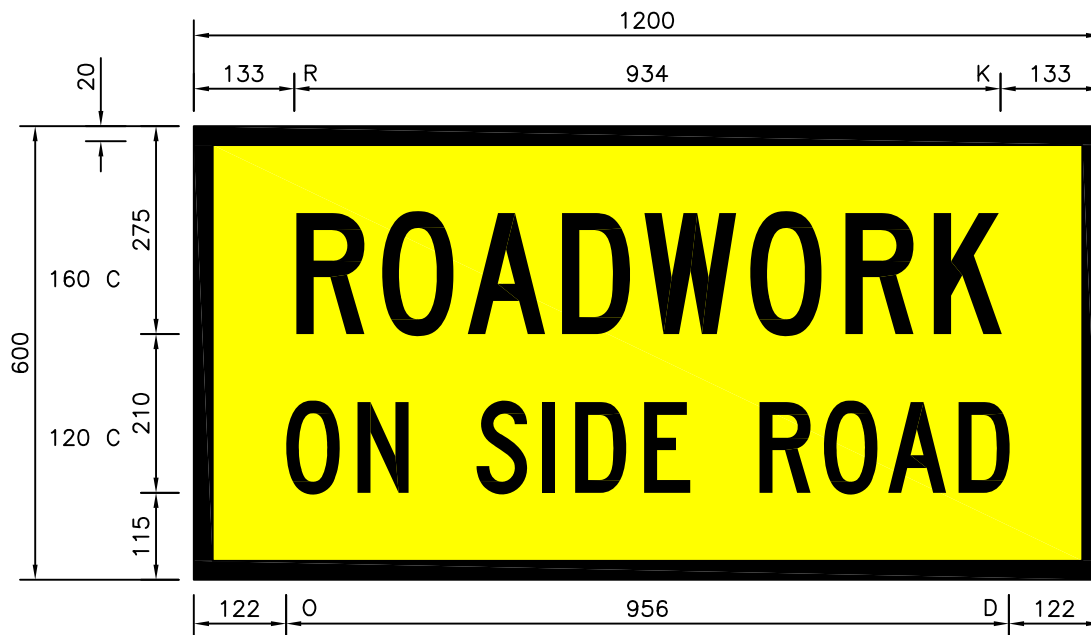

NOTE:

To be used in multi-message sign frames only.



Black

Yellow class 1

Note: Letters & Numerals AS1744:2015.



Government of South Australia
Department of Planning,
Transport and Infrastructure

Road and Marine Services
Traffic Services, Traffic Solutions Unit

Drawn: A. Simister


Scale: 1:10

Authorisation:

Date: 9 January, 2020

TEMPORARY WARNING SIGN
'Roadwork On Side Road'

TM1-25C

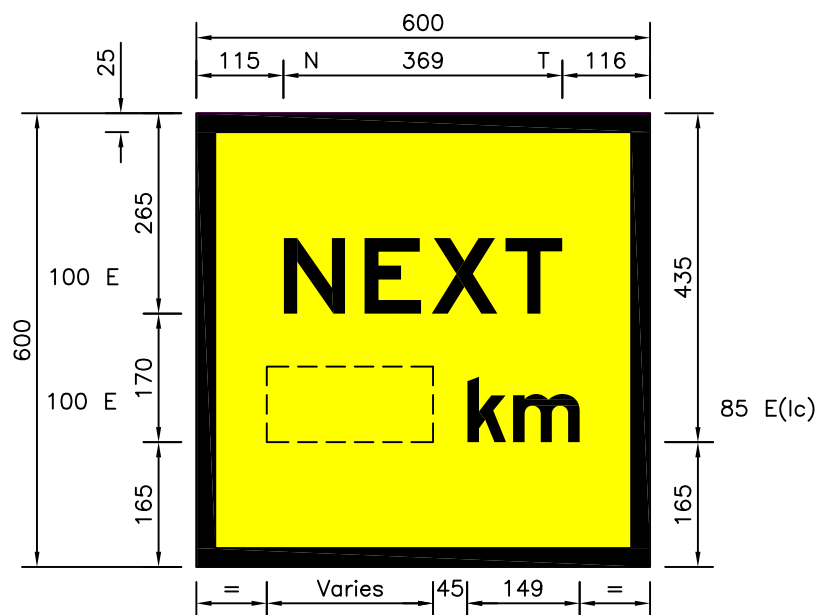

NOTE:

To be used in multi-message sign frames only.



Black

Yellow class 1

Note: Letters & Numerals AS1744:2015.



Government of South Australia

Department of Planning,
Transport and Infrastructure

Road and Marine Services
Traffic Services, Traffic Solutions Unit

Drawn: A. Simister

Scale: 1:10


Authorisation:

Date: 9 January, 2020

TEMPORARY WARNING SIGN

'Next xx km'

TM1-28A

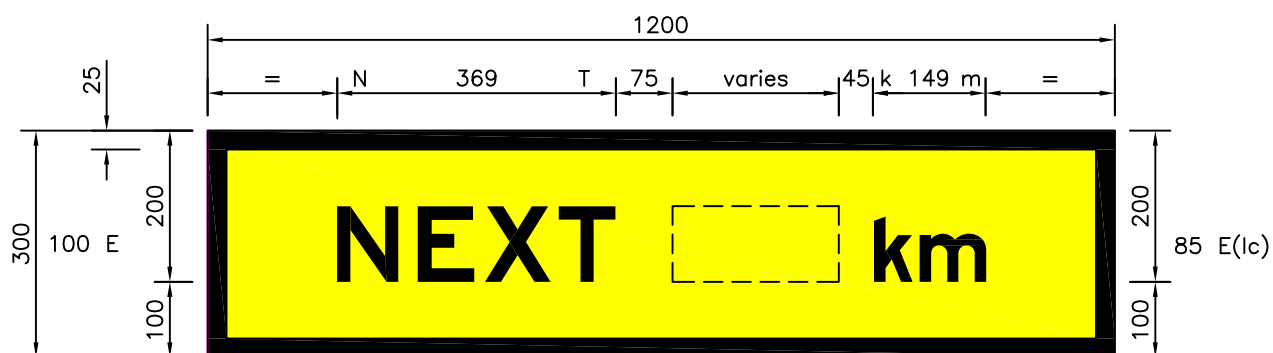

NOTE:

To be used in multi-message sign frames only.



Black

Yellow class 1

Note: Letters & Numerals AS1744:2015.



Government of South Australia

Department of Planning,
Transport and Infrastructure

Road and Marine Services
Traffic Services, Traffic Solutions Unit

Drawn: A. Simister

Scale: 1:10


TEMPORARY WARNING SIGN

'Next xx km'

Authorisation:

Date: 9 January, 2020

TM1-28B

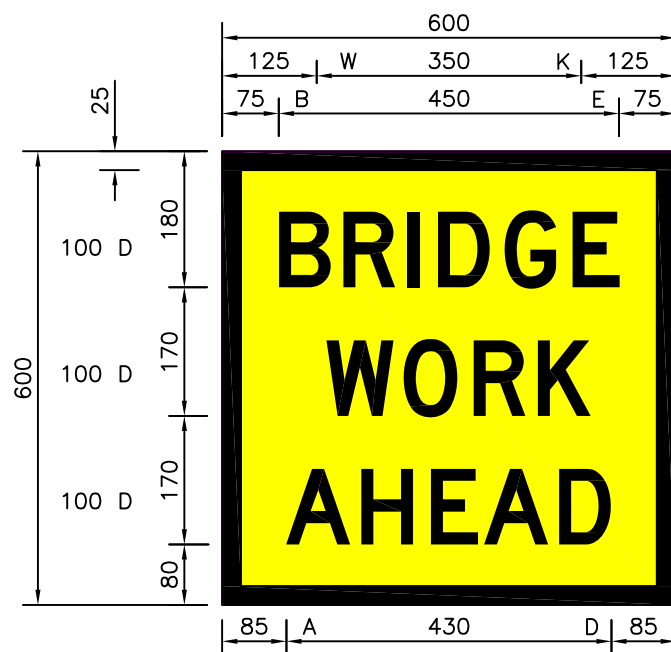

NOTE:
To be used in
multi-message sign frames
only.



Black

Yellow class 1

Note: Letters & Numerals AS1744:2015.



Government of South Australia

Department of Planning,
Transport and Infrastructure

Road and Marine Services
Traffic Services, Traffic Solutions Unit

Drawn: A. Simister


Scale: 1:10

Authorisation:

Date: 9 January, 2020

TEMPORARY WARNING SIGN
'Bridge Work Ahead'

TM1-2A

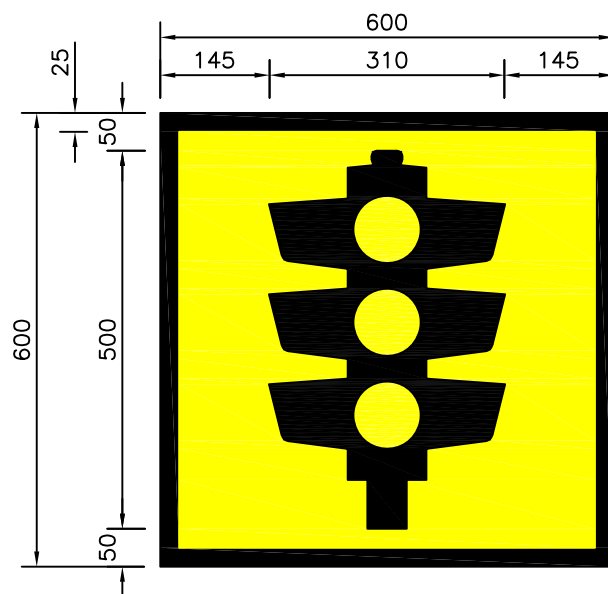

T1-30mod@100%

NOTE:

To be used in
multi-message sign frames
only.



Black

Yellow class 1

Note: Letters & Numerals AS1744:2015.



Government of South Australia

Department of Planning,
Transport and Infrastructure

Road and Marine Services
Traffic Services, Traffic Solutions Unit

Drawn: A. Simister


Scale: 1:10

Authorisation:

Date: 9 January, 2020

TEMPORARY WARNING SIGN
'Signals Ahead'

TM1-30A

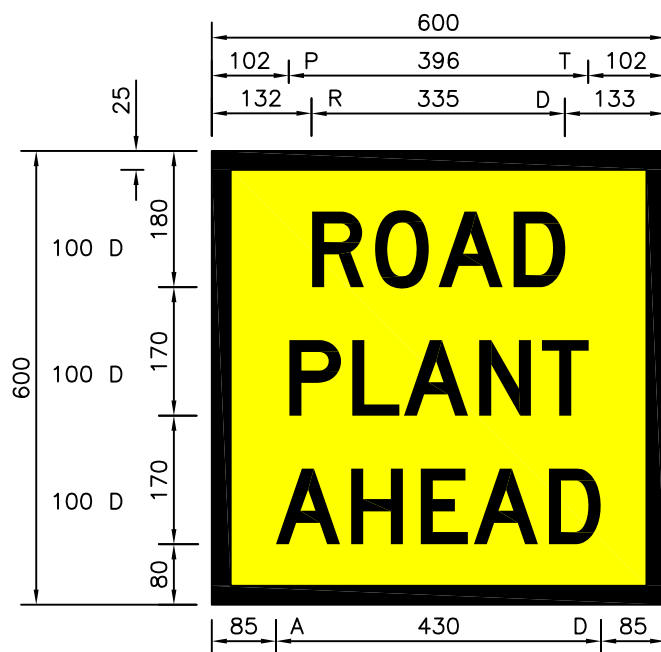

NOTE:

To be used in multi-message sign frames only.



Black

Yellow class 1

Note: Letters & Numerals AS1744:2015.



Government of South Australia

Department of Planning,
Transport and Infrastructure

Road and Marine Services
Traffic Services, Traffic Solutions Unit

Drawn: A. Simister

Scale: 1:10


Authorisation:

Date: 9 January, 2020

TEMPORARY WARNING SIGN

'Road Plant Ahead'

TM1-3-1A

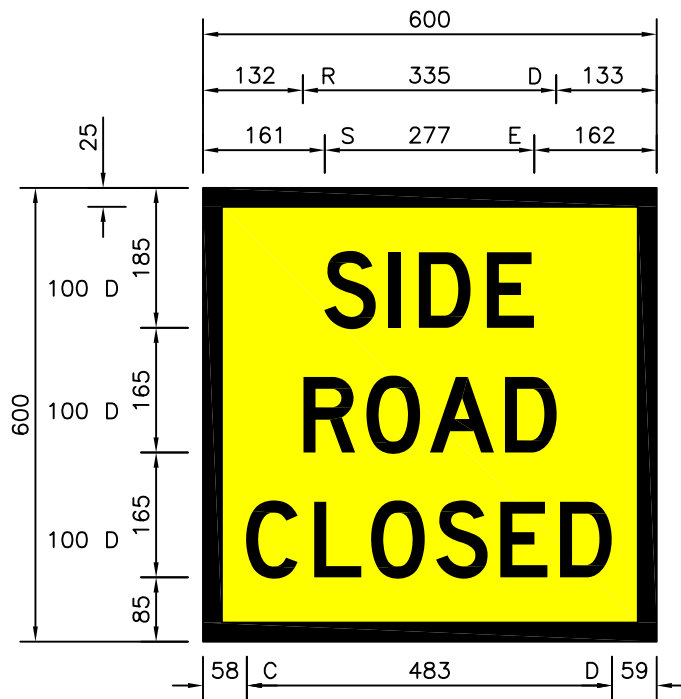

NOTE:

To be used in multi-message sign frames only.



Black

Yellow class 1

Note: Letters & Numerals AS1744:2015.



Government of South Australia
Department of Planning,
Transport and Infrastructure

Road and Marine Services
Traffic Services, Traffic Solutions Unit

Drawn: A. Simister


Scale: 1:10

Authorisation:

Date: 9 January, 2020

TEMPORARY WARNING SIGN
'Side Road Closed'

TM1-32A

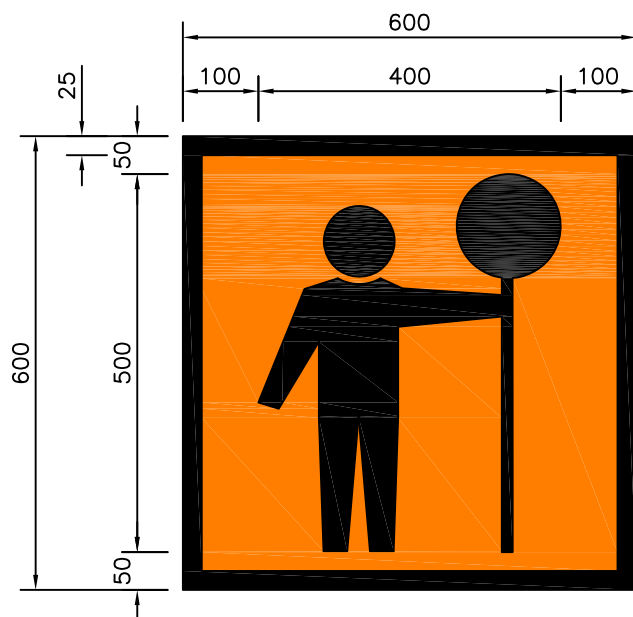

T1-34mod@100%

NOTE:

To be used in
multi-message sign frames
only.



Black

Fluorescent Orange

Note: Letters & Numerals AS1744:2015.



Government of South Australia
Department of Planning,
Transport and Infrastructure

Road and Marine Services
Traffic Services, Traffic Solutions Unit

Drawn: A. Simister


Scale: 1:10

Authorisation:

Date: 9 January, 2020

TEMPORARY WARNING SIGN
'Traffic Controller'

TM1-34A

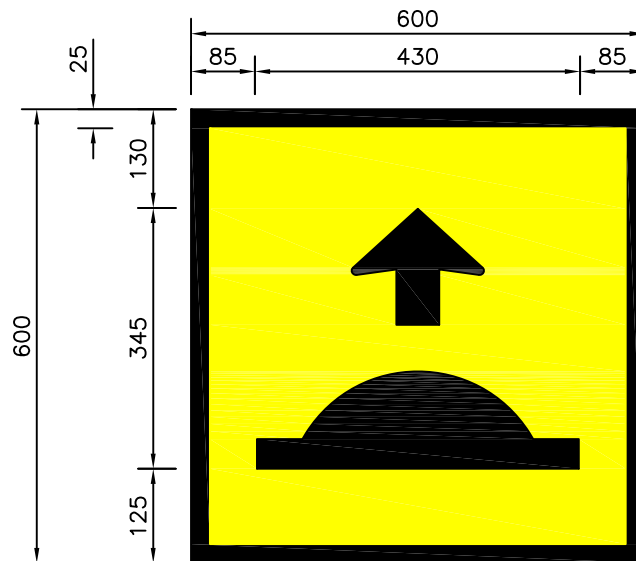

W3-4B(mod) @70%

NOTE:

To be used in multi-message sign frames only.



Black

Yellow class 1

Note: Letters & Numerals AS1744:2015.



Government of South Australia
Department of Planning,
Transport and Infrastructure

Road and Marine Services
Traffic Services, Traffic Solutions Unit

Drawn: A. Simister


Scale: 1:10

Authorisation:

Date: 9 January, 2020

TEMPORARY WARNING SIGN
'Road Hump(s) Ahead'

TM1-38A

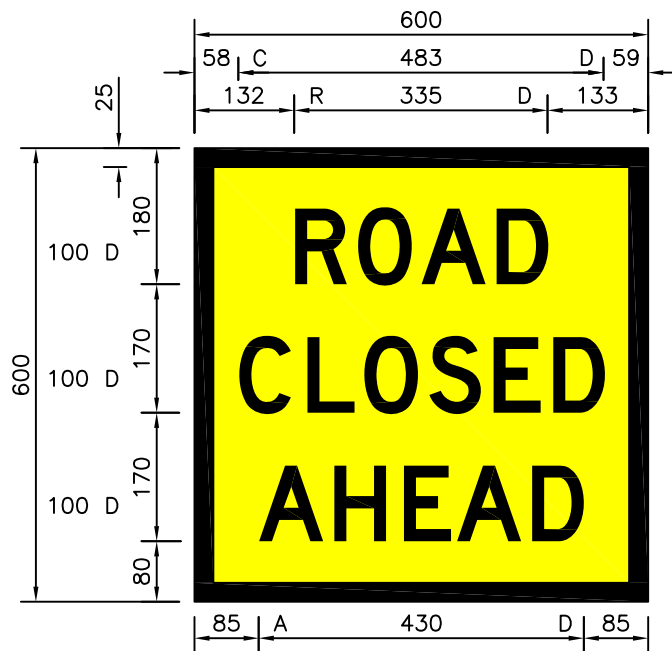

NOTE:

To be used in multi-message sign frames only.



Black

Yellow class 1

Note: Letters & Numerals AS1744:2015.



Government of South Australia
Department of Planning,
Transport and Infrastructure

Road and Marine Services
Traffic Services, Traffic Solutions Unit

Drawn: A. Simister


Scale: 1:10

Authorisation:

Date: 9 January, 2020

TEMPORARY WARNING SIGN
'Road Closed Ahead'

TM1-43A

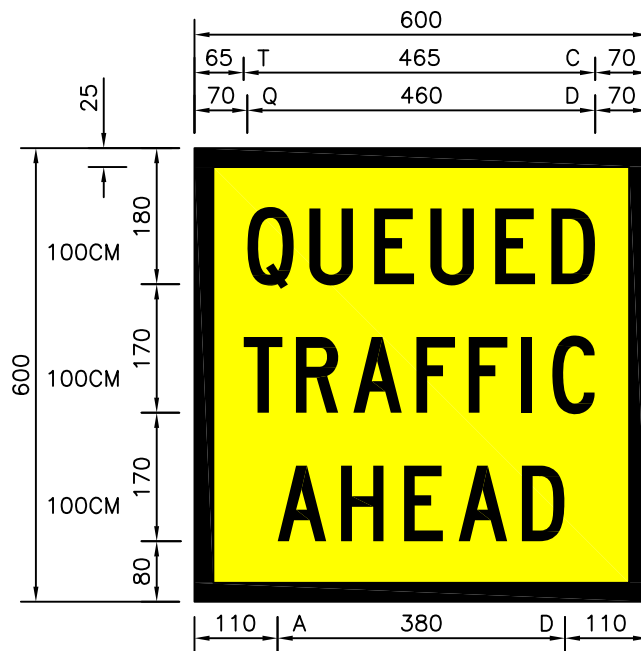

NOTE:

To be used in multi-message sign frames only.



Black

Yellow class 1

Note: Letters & Numerals AS1744:2015.



Government of South Australia
Department of Planning,
Transport and Infrastructure

Road and Marine Services
Traffic Services, Traffic Solutions Unit

Drawn: A. Simister


Scale: 1:10

Authorisation:

Date: 9 January, 2020



TEMPORARY WARNING SIGN
'Queued Traffic Ahead'

TM1-46A

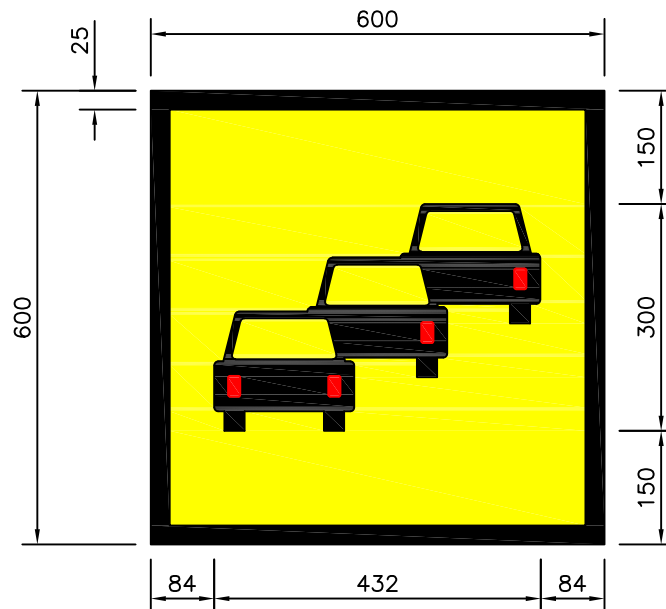

NOTE:

To be used in multi-message sign frames only.

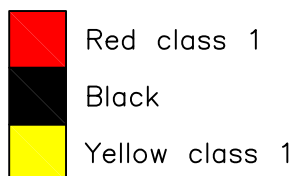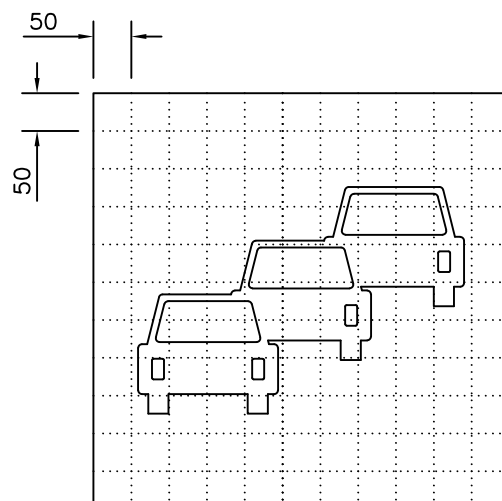

Note: Letters & Numerals AS1744:2015.



Government of South Australia
Department of Planning,
Transport and Infrastructure

Road and Marine Services
Traffic Services, Traffic Solutions Unit

Drawn: A. Simister


Scale: 1:10

Authorisation:


Date: 9 January, 2020

TEMPORARY WARNING SIGN
'Queuing Cars' (graphical)

TM1-47A

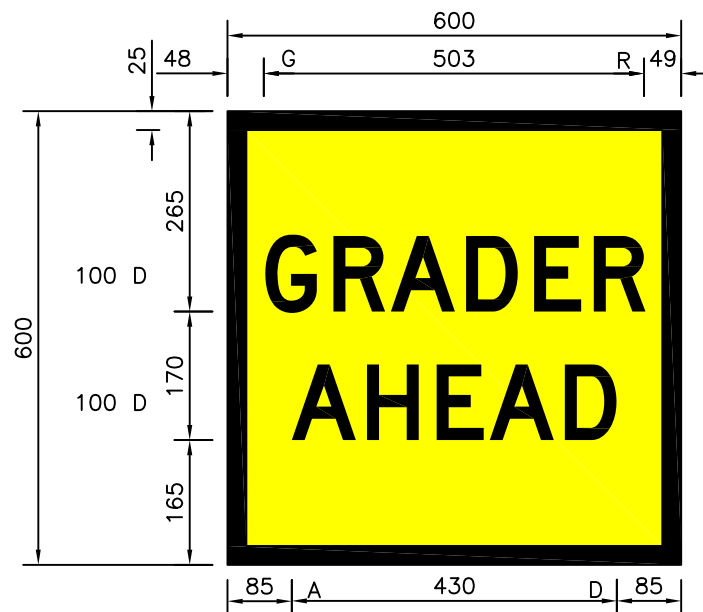


NOTE:
To be used in
multi-message sign frames
only.

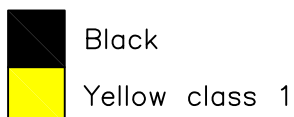

Note: Letters & Numerals AS1744:2015.

 Government of South Australia Department of Planning, Transport and Infrastructure	TEMPORARY WARNING SIGN 'Grader ahead'	
Road and Marine Services Traffic Services, Traffic Solutions Unit	Authorisation: 	TM1-4A
Drawn: A. Simister	Scale: 1:5	
Date: 9 January, 2020		

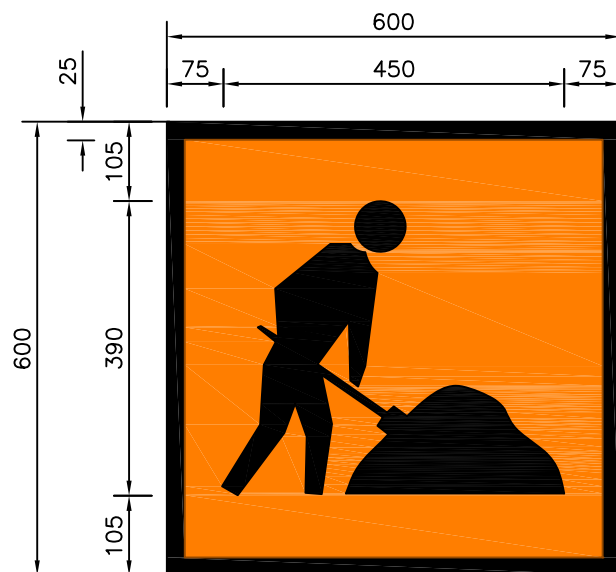

T1-5Amod@80%

NOTE:
To be used in
multi-message sign frames
only.



Black

Fluorescent Orange

Note: Letters & Numerals AS1744:2015.



Government of South Australia
Department of Planning,
Transport and Infrastructure

Road and Marine Services
Traffic Services, Traffic Solutions Unit

Drawn: A. Simister


Scale: 1:10

Authorisation:

Date: 9 January, 2020


TEMPORARY WARNING SIGN
'Workers Ahead'

TM1-5A

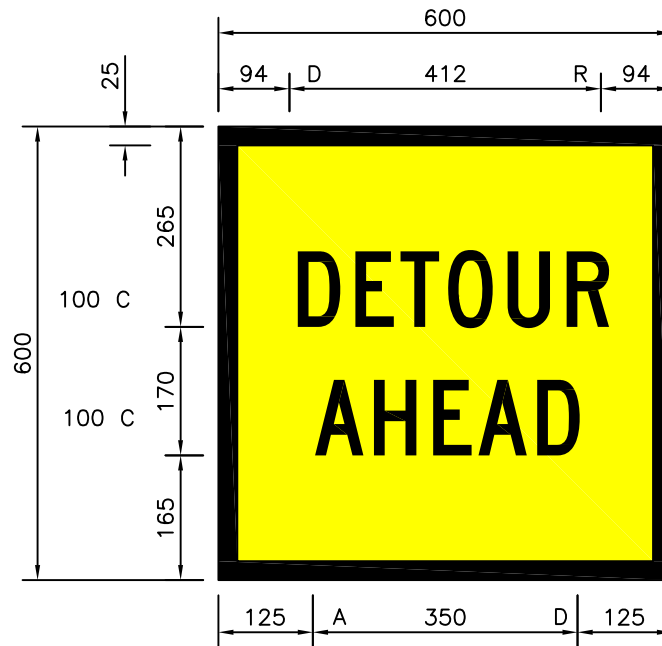

NOTE:

To be used in multi-message sign frames only.

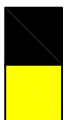

Black

Yellow class 1

Note: Letters & Numerals AS1744:2015.



Government of South Australia
Department of Planning,
Transport and Infrastructure

Road and Marine Services
Traffic Services, Traffic Solutions Unit

Drawn: A. Simister


Scale: 1:10

Authorisation:

Date: 9 January, 2020

TEMPORARY WARNING SIGN
'Detour Ahead'

TM1-6A

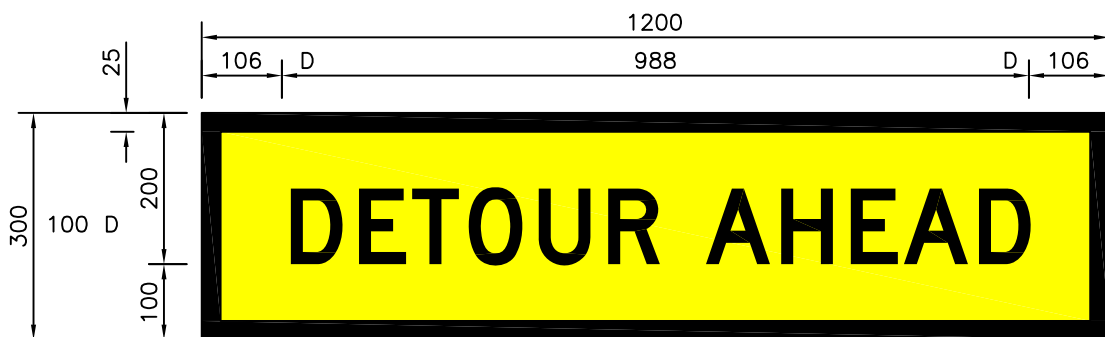

NOTE:

To be used in multi-message sign frames only.



Black

Yellow class 1

Note: Letters & Numerals AS1744:2015.



Government of South Australia

Department of Planning,
Transport and Infrastructure

Road and Marine Services
Traffic Services, Traffic Solutions Unit

Drawn: A. Simister

Scale: 1:10


Authorisation:

Date: 9 January, 2020

TEMPORARY WARNING SIGN

'Detour Ahead'

TM1-6B

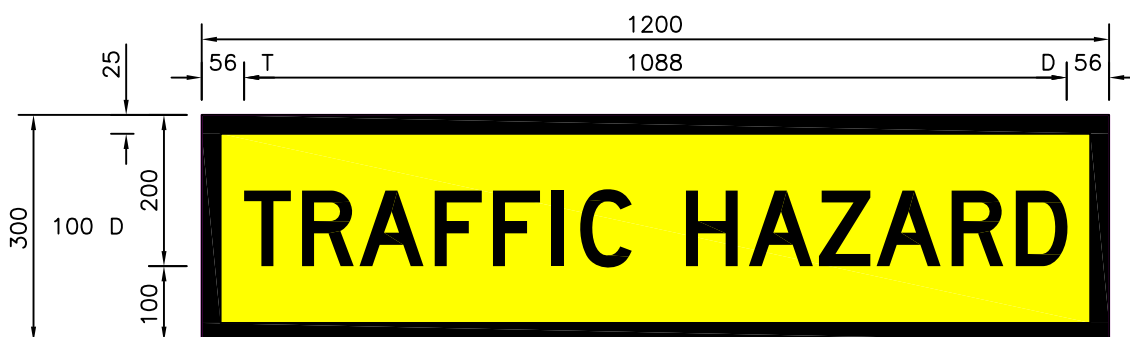

NOTE:

To be used in multi-message sign frames only.



Black

Yellow class 1

Note: Letters & Numerals AS1744:2015.



Government of South Australia

Department of Planning,
Transport and Infrastructure

Road and Marine Services
Traffic Services, Traffic Solutions Unit

Drawn: A. Simister


Scale: 1:10

Authorisation:

Date: 9 January, 2020

TEMPORARY WARNING SIGN
'Traffic hazard'

TM1-SA10B

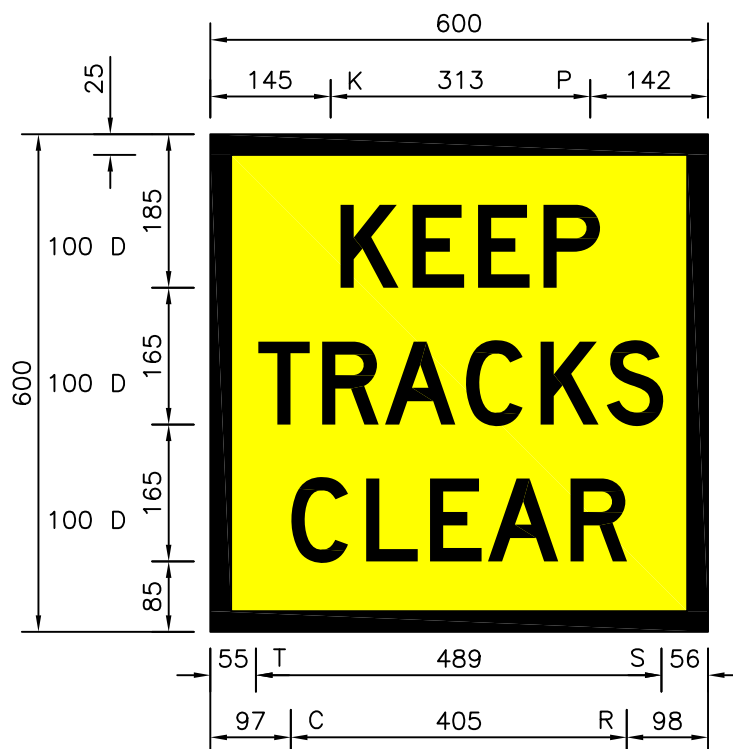

NOTE:

To be used in multi-message sign frames only.



Black

Yellow class 1

Note: Letters & Numerals AS1744:2015.



Government of South Australia

Department of Planning,
Transport and Infrastructure

Road and Marine Services
Traffic Services, Traffic Solutions Unit

Drawn: A. Simister

Scale: 1:10


TEMPORARY WARNING SIGN

'Keep Tracks Clear'

Authorisation:

Date: 9 January, 2020

TM1-SA124A

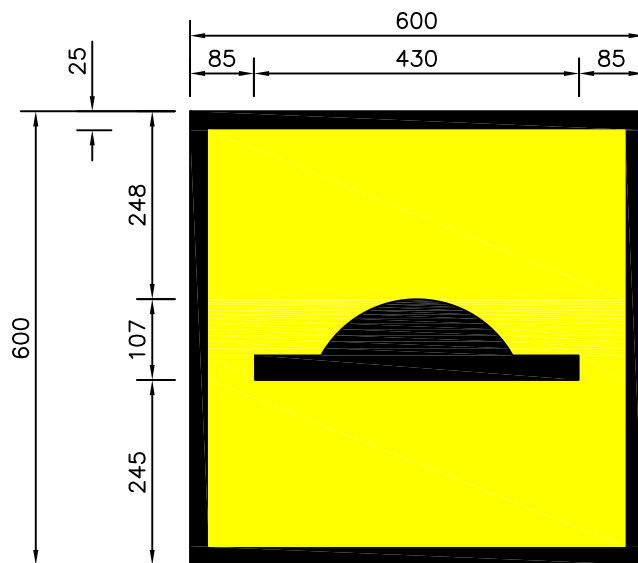

W5-10B(mod)@58%

NOTE:

To be used in multi-message sign frames only.



Black

Yellow class 1

Note: Letters & Numerals AS1744:2015.



Government of South Australia
Department of Planning,
Transport and Infrastructure

Road and Marine Services
Traffic Services, Traffic Solutions Unit

Drawn: A. Simister


Scale: 1:10

Authorisation:

Date: 9 January, 2020

TEMPORARY WARNING SIGN
'Road Hump'

TM1-SA130A

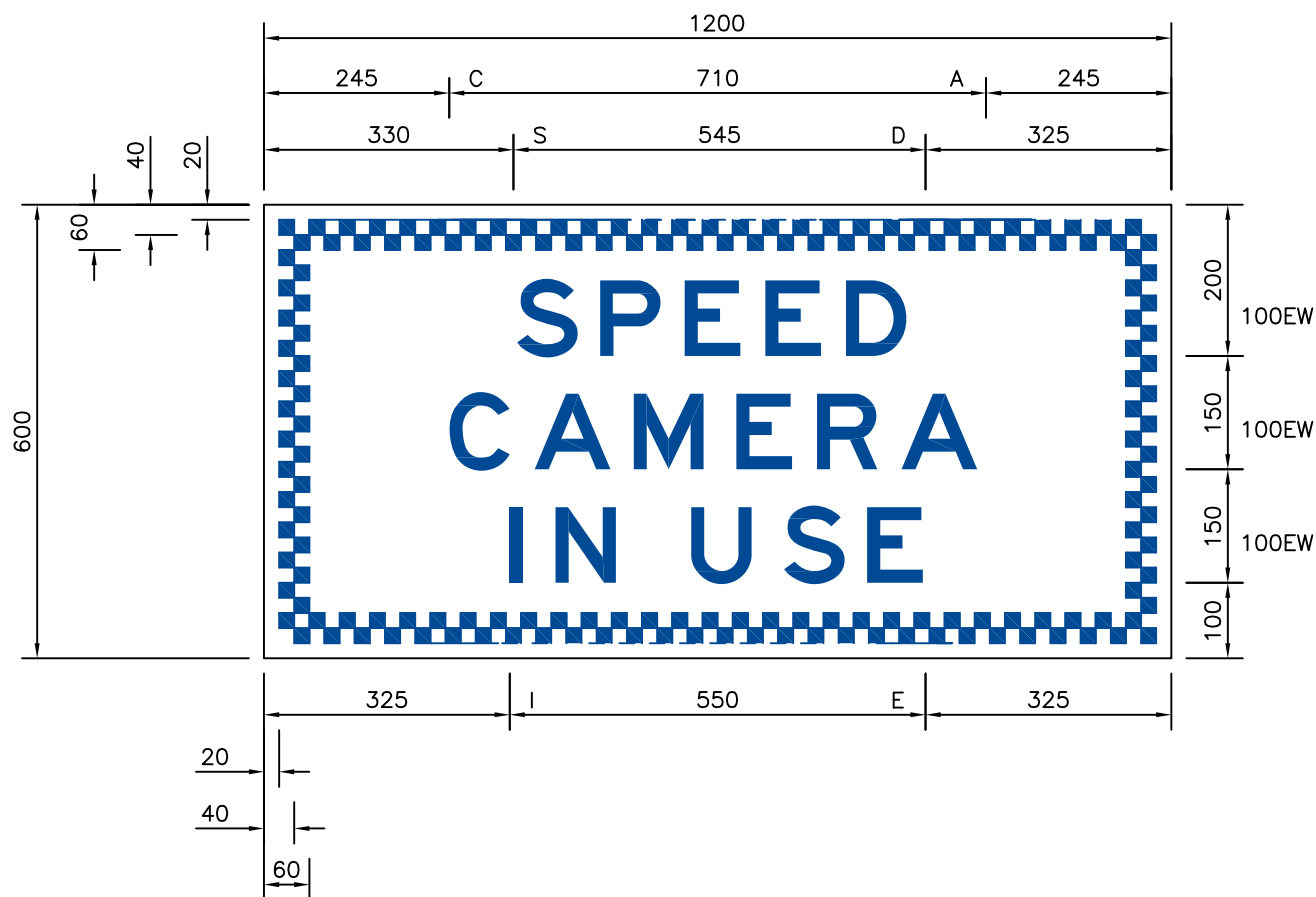

NOTE:

To be used in multi-message sign frames only.



White class 1

Blue class 1

Note: Letters & Numerals AS1744:2015.



Government of South Australia
Department of Planning,
Transport and Infrastructure

Road and Marine Services
Traffic Services, Traffic Solutions Unit

Drawn: A. Simister


Scale: 1:10

Authorisation:

Date: 9 January, 2020

TEMPORARY WARNING SIGN
'Speed Camera in Use'

TM1-SA136C

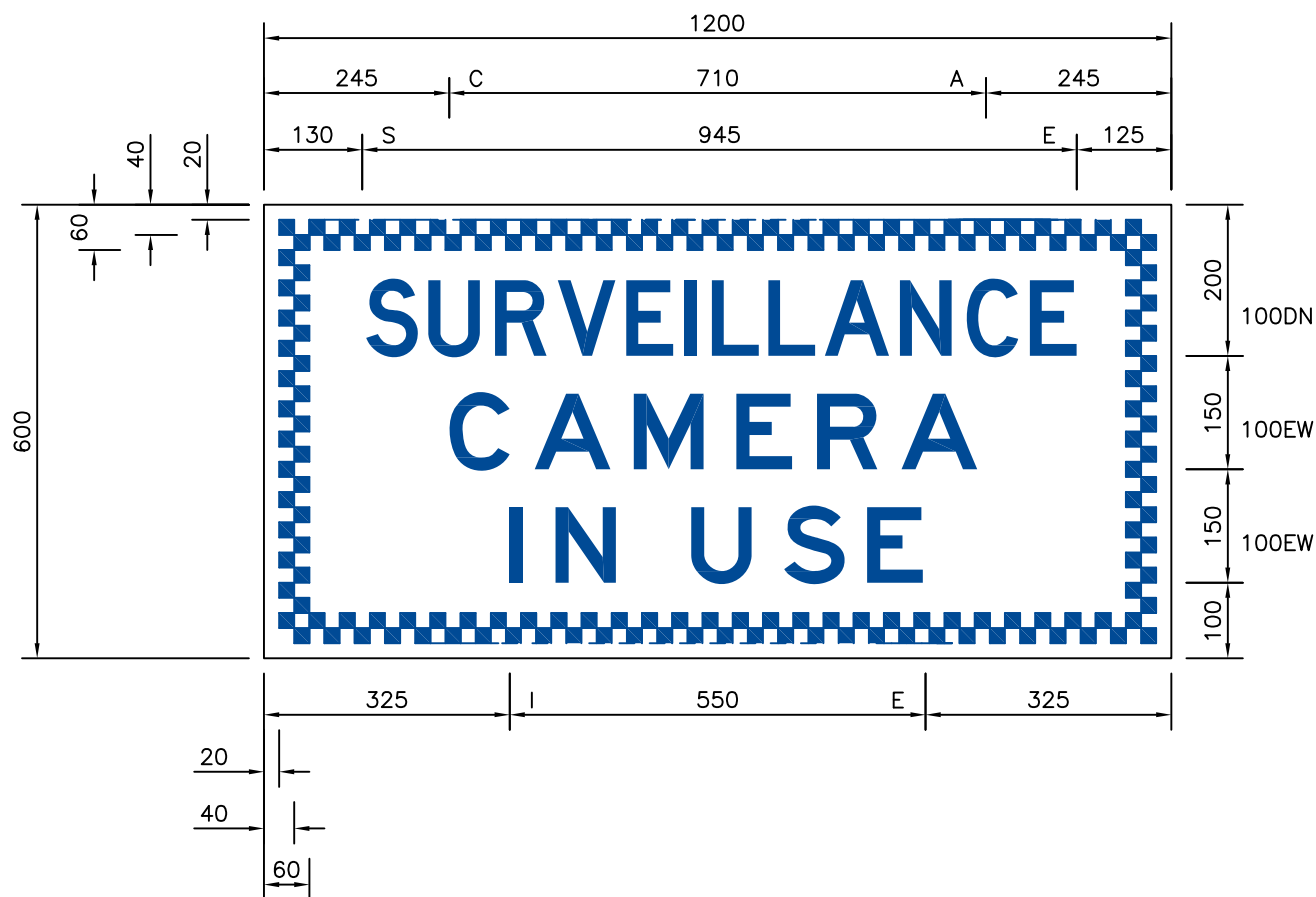

NOTE:

To be used in multi-message sign frames only.



White class 1

Blue class 1

Note: Letters & Numerals AS1744:2015.



Government of South Australia
Department of Planning,
Transport and Infrastructure

Road and Marine Services
Traffic Services, Traffic Solutions Unit

Drawn: A. Simister


Scale: 1:10

Authorisation:

Date: 9 January, 2020

TEMPORARY WARNING SIGN
'Surveillance Camera in Use'

TM1-SA137C

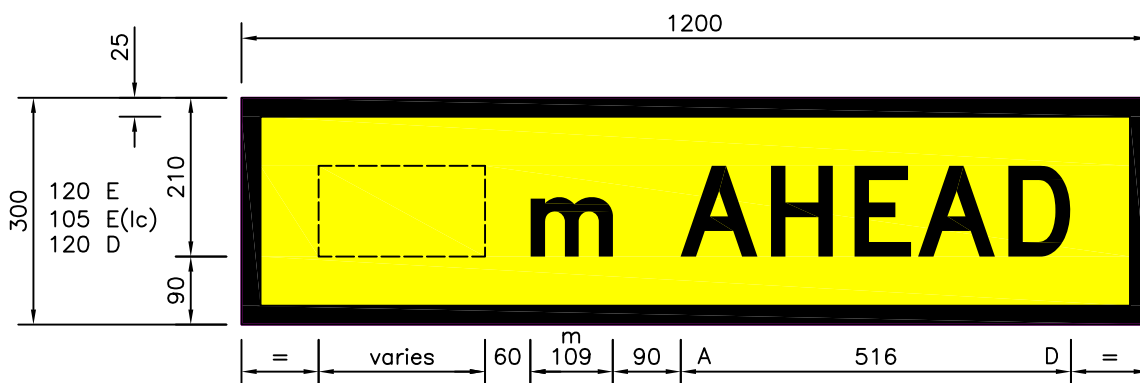

NOTE: To be used in multi-message sign frame only.



Black

Yellow (retro-reflective)

Note: Letters & Numerals AS1744:2015.



Government of South Australia
Department of Planning,
Transport and Infrastructure

Road and Marine Services
Traffic Services, Traffic Solutions Unit

Drawn: A. Simister


Scale: 1:10

Authorisation:

Date: 9 January, 2020

TEMPORARY WARNING SIGN
'x m Ahead'

TM1-SA140B

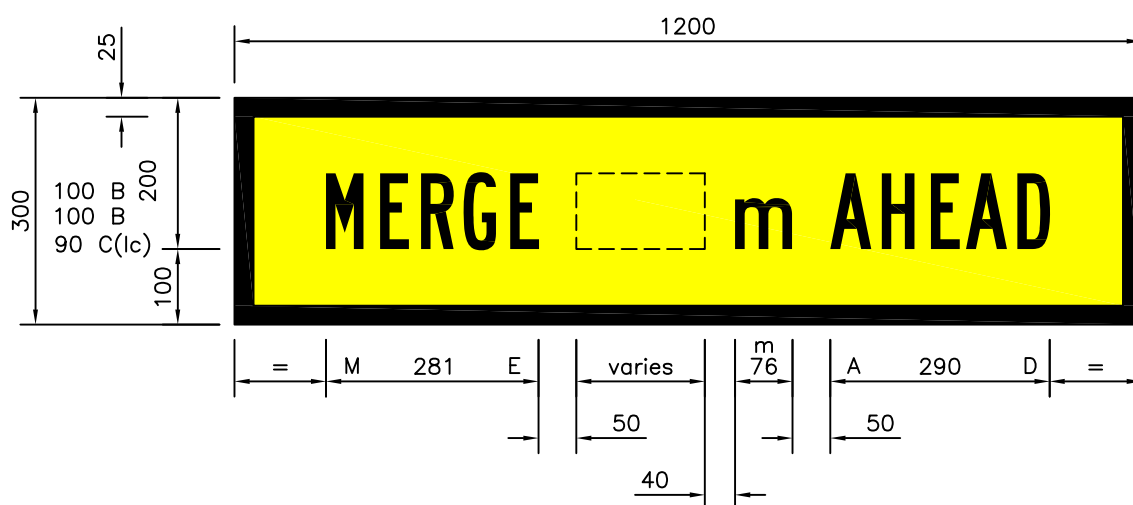

NOTE: To be used in multi-message sign frame only.



Black

Yellow (retro-reflective)

Note: Letters & Numerals AS1744:2015.



Government of South Australia
Department of Planning,
Transport and Infrastructure

Road and Marine Services
Traffic Services, Traffic Solutions Unit

Drawn: A. Simister



Scale: 1:10

Authorisation:

Date: 9 January, 2020

TEMPORARY WARNING SIGN
'Merge xxx m Ahead'

TM1-SA141B

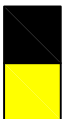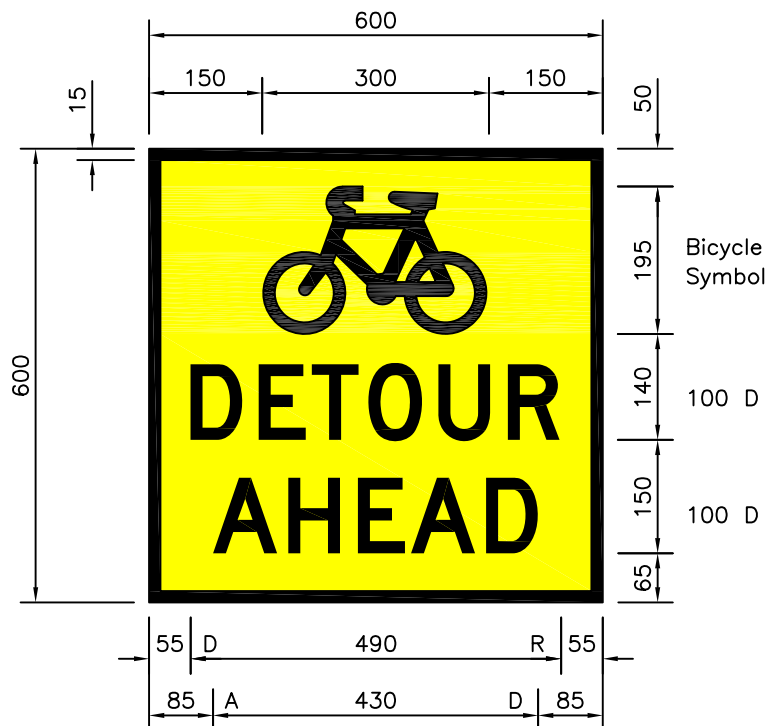

Black

Yellow class 1

Note: Letters & Numerals AS1744:2015.



Government of South Australia

Department of Planning,
Transport and Infrastructure

Road and Marine Services
Traffic Services, Traffic Solutions Unit

Drawn: A. Simister


Scale: 1:10

TEMPORARY WARNING SIGN
'Bicycle Detour Ahead'

Authorisation:


Date: 9 January, 2020

TM1-SA145A

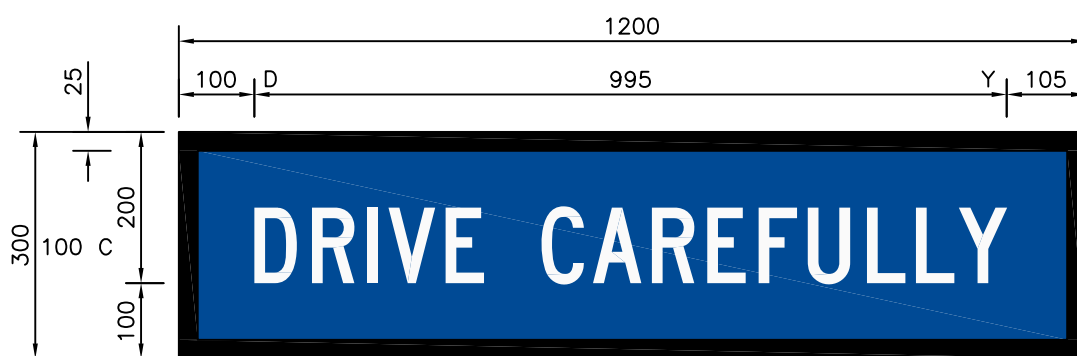


NOTE:

To be used in multi-message sign frames only.

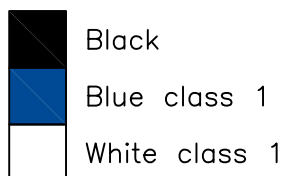


Note: Letters & Numerals AS1744:2015.

 Government of South Australia Department of Planning, Transport and Infrastructure	TEMPORARY WARNING SIGN 'Drive Carefully'	
Road and Marine Services Traffic Services, Traffic Solutions Unit	Authorisation: 	TM1-SA147B
Drawn: A. Simister	Scale: 1:10	
Date: 9 January, 2020		

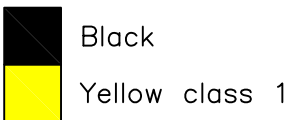

 Government of South Australia Department of Planning, Transport and Infrastructure		TEMPORARY WARNING SIGN 'Expect Delays xx min'	
Road and Marine Services Traffic Services, Traffic Solutions Unit		Authorisation: 	TM1-SA149A
Drawn: A. Simister	Scale: 1:10	Date: 9 January, 2020	

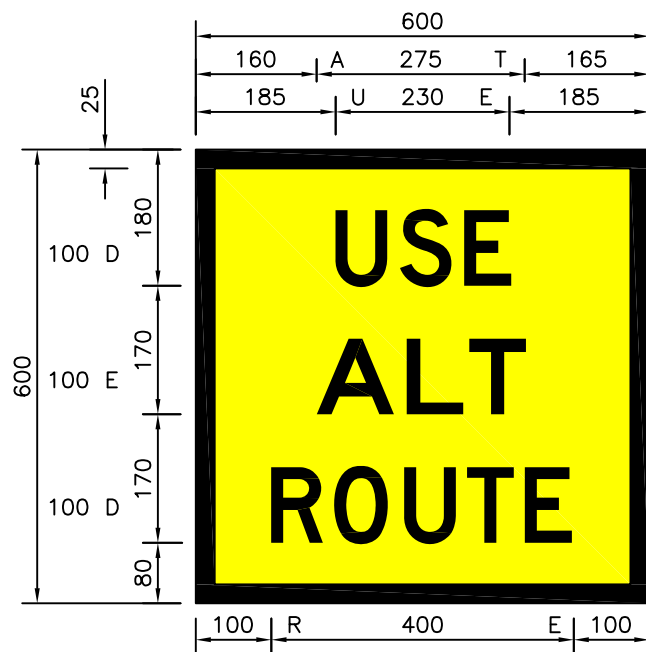

NOTE:

To be used in multi-message sign frames only.



Black

Yellow class 1

Note: Letters & Numerals AS1744:2015.



Government of South Australia
Department of Planning,
Transport and Infrastructure

Road and Marine Services
Traffic Services, Traffic Solutions Unit

Drawn: A. Simister


Scale: 1:10

Authorisation:

Date: 21 August, 2018

TEMPORARY WARNING SIGN
'Use Alternative Route'

T1-SA150M

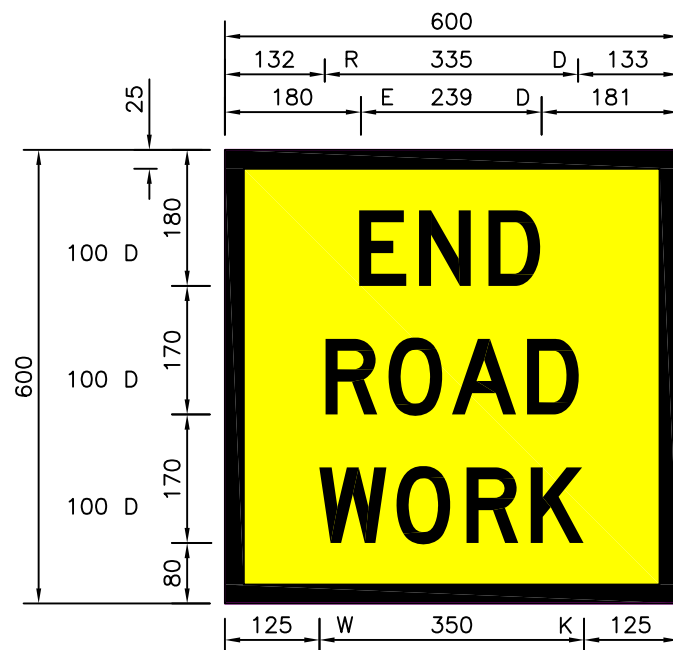

NOTE:

To be used in multi-message sign frames only.



Black

Yellow class 1

Note: Letters & Numerals AS1744:2015.



Government of South Australia

Department of Planning,
Transport and Infrastructure

Road and Marine Services
Traffic Services, Traffic Solutions Unit

Drawn: A. Simister

Scale: 1:10


TEMPORARY WARNING SIGN

'End Road Work'

Authorisation:

Date: 9 January, 2020

TM2-17A

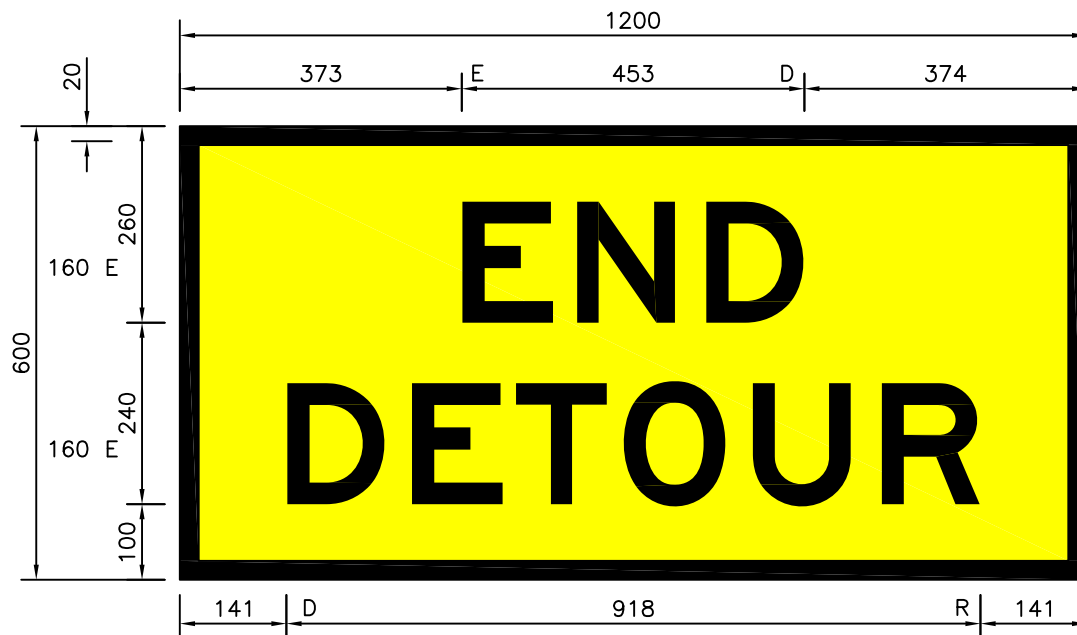

NOTE:

To be used in multi-message sign frames only.



Black

Yellow class 1

Note: Letters & Numerals AS1744:2015.



Government of South Australia
Department of Planning,
Transport and Infrastructure

Road and Marine Services
Traffic Services, Traffic Solutions Unit

Drawn: A. Simister


Scale: 1:10

Authorisation:

Date: 9 January, 2020

TEMPORARY WARNING SIGN
'End Detour'

TM2-23C

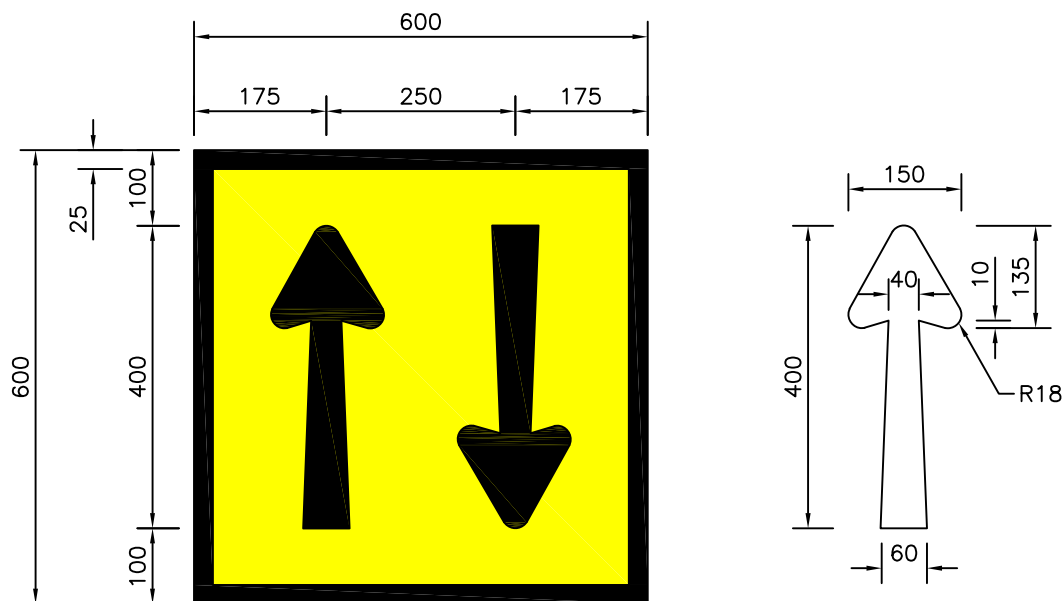

NOTE:
To be used in
multi-message sign frames
only.



Black

Yellow class 1

Note: Letters & Numerals AS1744:2015.



Government of South Australia
Department of Planning,
Transport and Infrastructure

Road and Marine Services
Traffic Services, Traffic Solutions Unit

Drawn: A. Simister


Scale: 1:10

Authorisation:

Date: 9 January, 2020

TEMPORARY WARNING SIGN
'Two Way Traffic'


TM2-24A

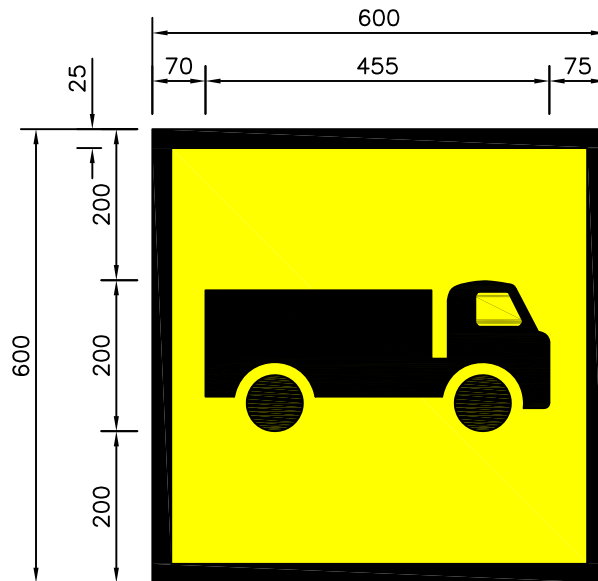

W5-22Amod@60%

NOTE:

To be used in
multi-message sign frames
only.

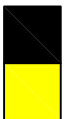

Black

Yellow class 1

Note: Letters & Numerals AS1744:2015.



Government of South Australia

Department of Planning,
Transport and Infrastructure

Road and Marine Services
Traffic Services, Traffic Solutions Unit

Drawn: A. Simister


Scale: 1:10

Authorisation:

Date: 9 January, 2020

TEMPORARY WARNING SIGN
'Trucks'

TM2-25A

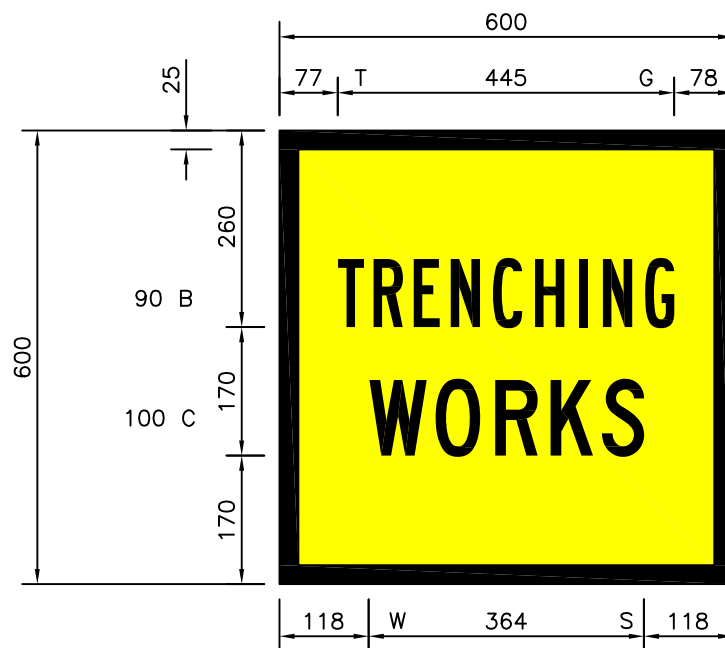

NOTE:

To be used in multi-message sign frames only.



Black

Yellow class 1

Note: Letters & Numerals AS1744:2015.



Government of South Australia
Department of Planning,
Transport and Infrastructure

Road and Marine Services
Traffic Services, Traffic Solutions Unit

Drawn: A. Simister


Scale: 1:10

Authorisation:

Date: 10 January, 2020

TEMPORARY WARNING SIGN
'Trenching Works'

TM2-29A

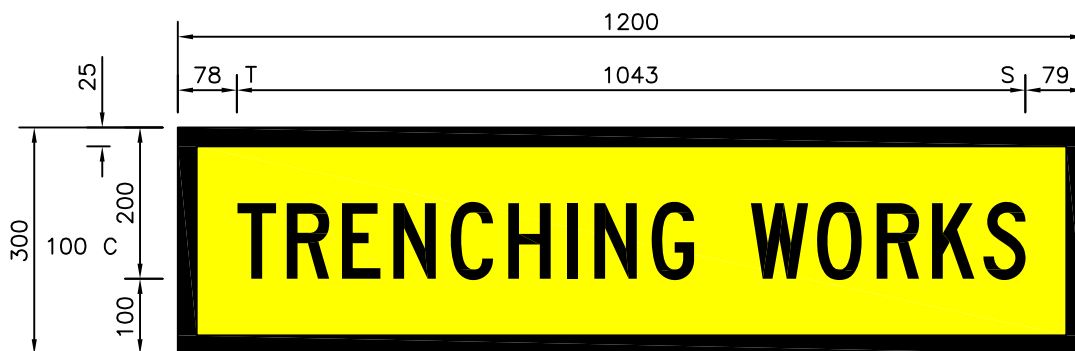

NOTE:

To be used in multi-message sign frames only.



Black

Yellow class 1

Note: Letters & Numerals AS1744:2015.



Government of South Australia
Department of Planning,
Transport and Infrastructure

Road and Marine Services
Traffic Services, Traffic Solutions Unit

Drawn: A. Simister

Scale: 1:10


Authorisation:

A handwritten signature in blue ink.

Date: 10 January, 2020

TEMPORARY WARNING SIGN
'Trenching Works'

TM2-29B

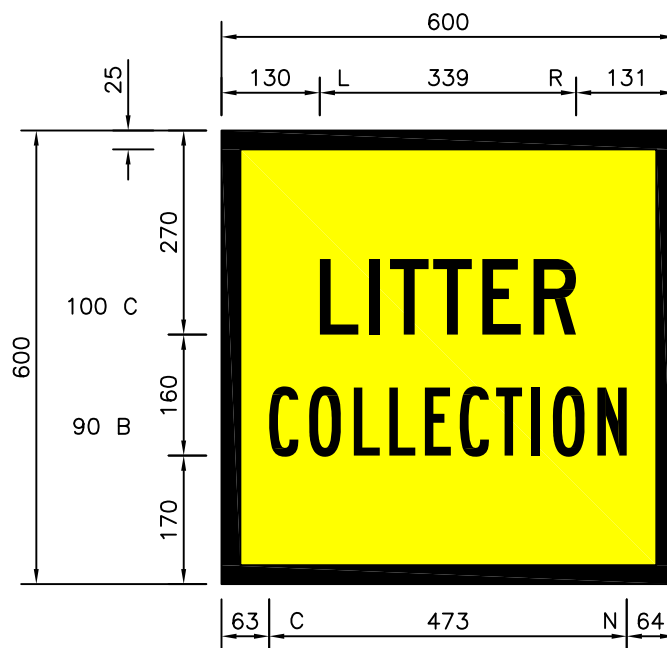

NOTE:

To be used in multi-message sign frames only.



Black

Yellow class 1

Note: Letters & Numerals AS1744:2015.



Government of South Australia
Department of Planning,
Transport and Infrastructure

Road and Marine Services
Traffic Services, Traffic Solutions Unit

Drawn: A. Simister


Scale: 1:10

Authorisation:

Date: 10 January, 2020

TEMPORARY WARNING SIGN
'Litter Collection'

TM2-31A

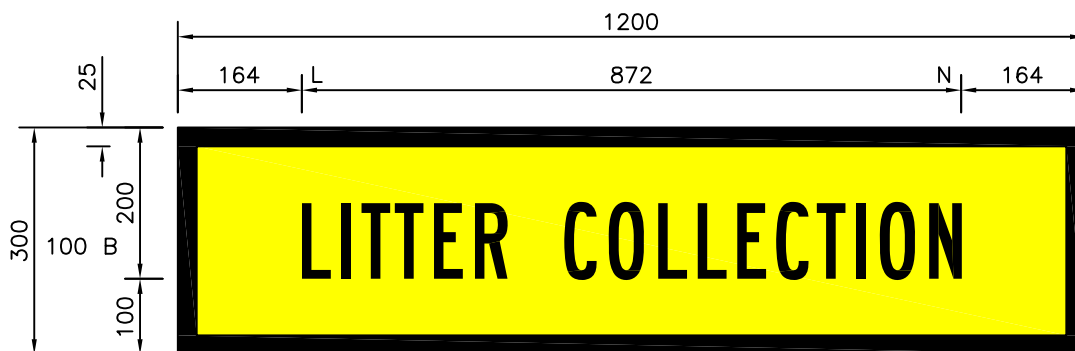

NOTE:

To be used in multi-message sign frames only.



Black

Yellow class 1

Note: Letters & Numerals AS1744:2015.



Government of South Australia
Department of Planning,
Transport and Infrastructure

Road and Marine Services
Traffic Services, Traffic Solutions Unit

Drawn: A. Simister


Scale: 1:10

Authorisation:

Date: 10 January, 2020

TEMPORARY WARNING SIGN
'Litter Collection'

TM2-31B

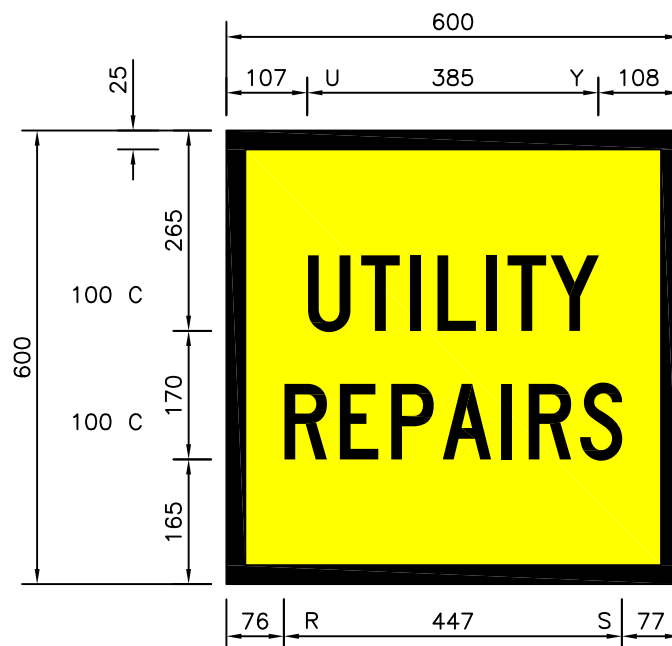

NOTE:

To be used in multi-message sign frames only.



Black

Yellow class 1

Note: Letters & Numerals AS1744:2015.



Government of South Australia
Department of Planning,
Transport and Infrastructure

Road and Marine Services
Traffic Services, Traffic Solutions Unit

Drawn: A. Simister


Scale: 1:10

Authorisation:

Date: 10 January, 2020

TEMPORARY WARNING SIGN
'Utility Repairs'

TM2-32A

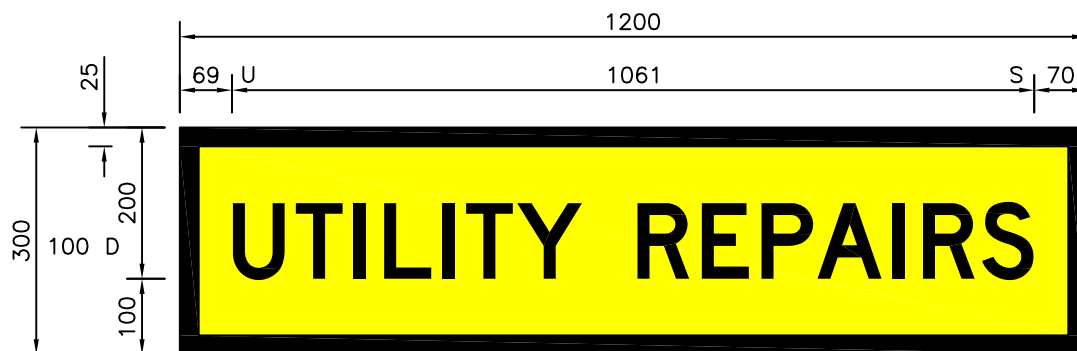

NOTE:

To be used in multi-message sign frames only.



Black

Yellow class 1

Note: Letters & Numerals AS1744:2015.



Government of South Australia
Department of Planning,
Transport and Infrastructure

Road and Marine Services
Traffic Services, Traffic Solutions Unit

Drawn: A. Simister


Scale: 1:10

Authorisation:

Date: 9 January, 2020

TEMPORARY WARNING SIGN
'Utility Repairs'

TM2-32B

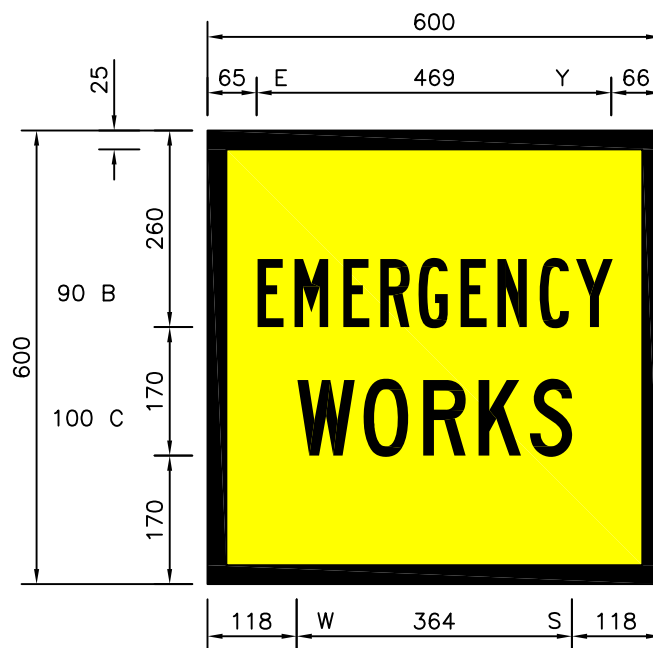

NOTE:

To be used in multi-message sign frames only.



Black

Yellow class 1

Note: Letters & Numerals AS1744:2015.



Government of South Australia
Department of Planning,
Transport and Infrastructure

Road and Marine Services
Traffic Services, Traffic Solutions Unit

Drawn: A. Simister


Scale: 1:10

Authorisation:

Date: 10 January, 2020


TEMPORARY WARNING SIGN
'Emergency Works'

TM2-33A

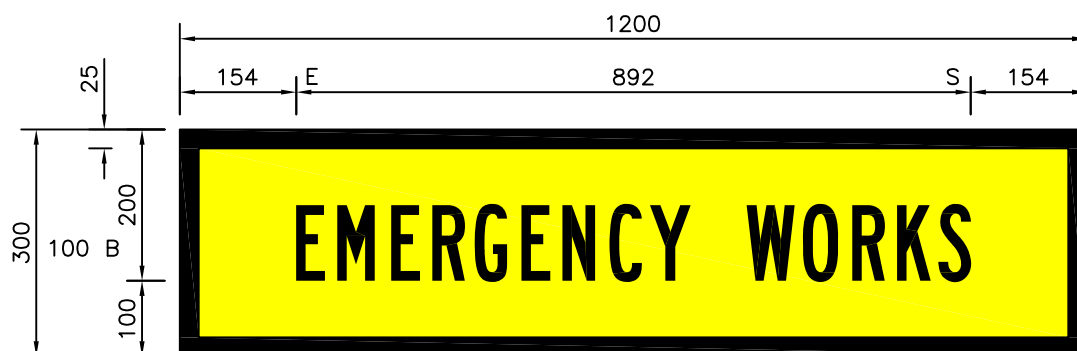

NOTE:

To be used in multi-message sign frames only.

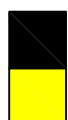

Black

Yellow class 1

Note: Letters & Numerals AS1744:2015.



Government of South Australia
Department of Planning,
Transport and Infrastructure

Road and Marine Services
Traffic Services, Traffic Solutions Unit

Drawn: A. Simister


Scale: 1:10

Authorisation:

Date: 10 January, 2020

TEMPORARY WARNING SIGN
'Emergency Works'

TM2-33B

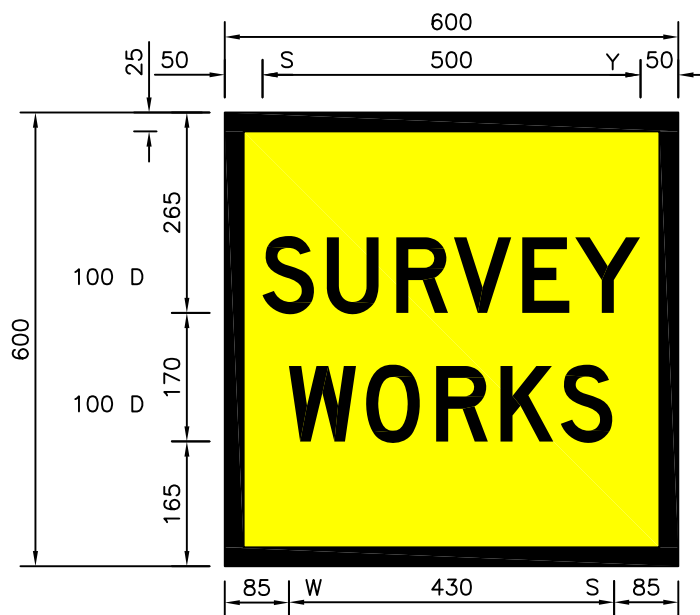

NOTE:

To be used in
multi-message sign frames
only.



Black

Yellow class 1

Note: Letters & Numerals AS1744:2015.



Government of South Australia
Department of Planning,
Transport and Infrastructure

Road and Marine Services
Traffic Services, Traffic Solutions Unit

Drawn: A. Simister


Scale: 1:5

Authorisation:

Date: 9 January, 2020

TEMPORARY WARNING SIGN
'Survey Works'

TM2-34A

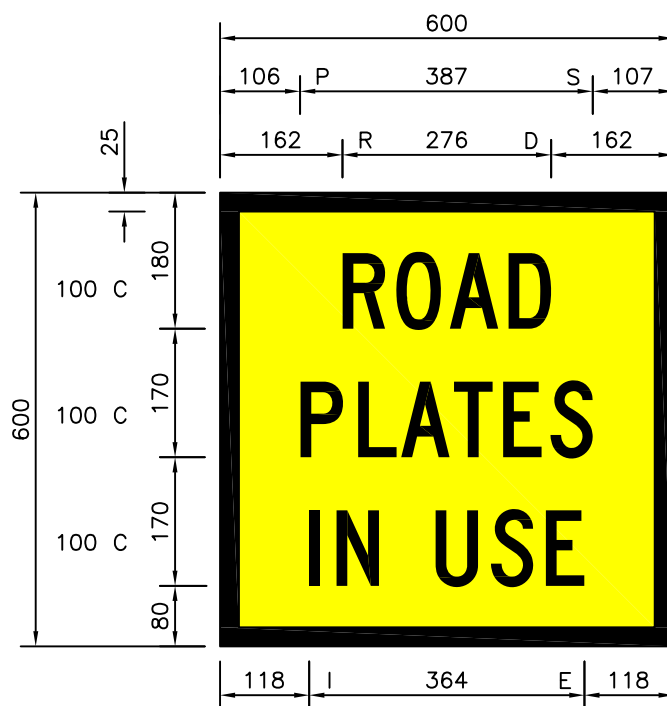

NOTE:

To be used in multi-message sign frames only.



Black

Yellow class 1

Note: Letters & Numerals AS1744:2015.



Government of South Australia
Department of Planning,
Transport and Infrastructure

Road and Marine Services
Traffic Services, Traffic Solutions Unit

Drawn: A. Simister


Scale: 1:10

Authorisation:

Date: 10 January, 2020

TEMPORARY WARNING SIGN
'Road Plates In Use'

TM2-36A

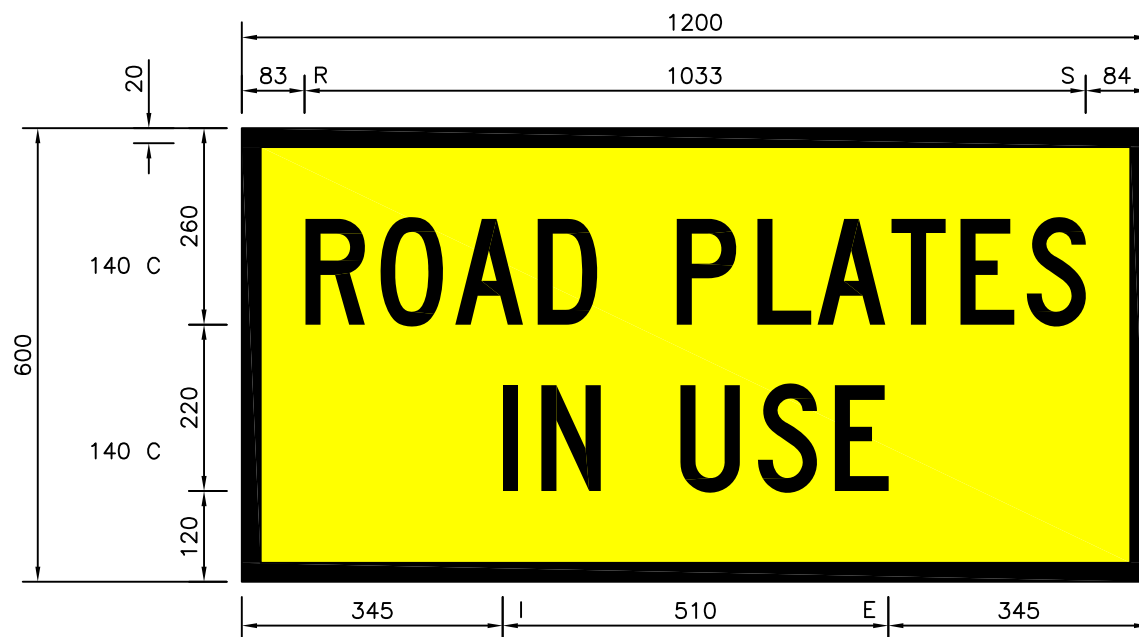

NOTE:

To be used in multi-message sign frames only.



Black

Yellow class 1

Note: Letters & Numerals AS1744:2015.



Government of South Australia
Department of Planning,
Transport and Infrastructure

Road and Marine Services
Traffic Services, Traffic Solutions Unit

Drawn: A. Simister


Scale: 1:10

Authorisation:

Date: 10 January, 2020

TEMPORARY WARNING SIGN
'Road Plates In Use'

TM2-36C

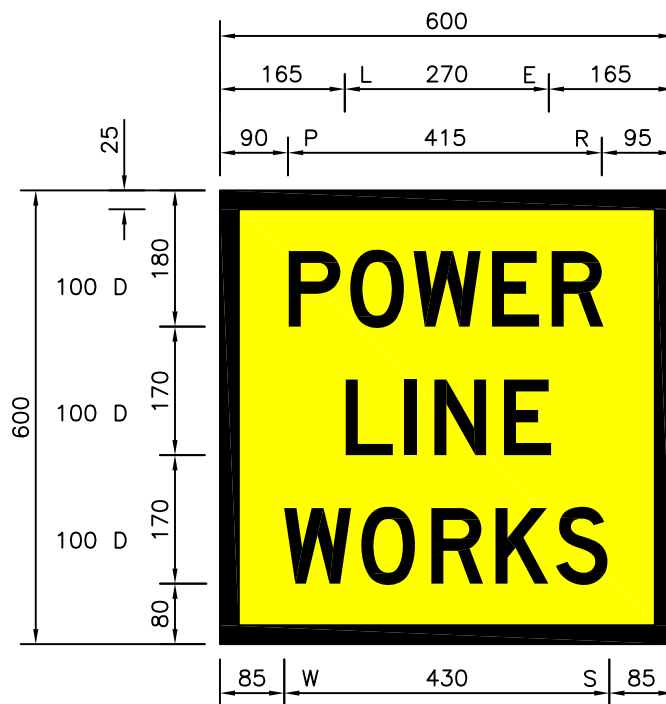

NOTE:

To be used in multi-message sign frames only.



Black

Yellow class 1

Note: Letters & Numerals AS1744:2015.



Government of South Australia
Department of Planning,
Transport and Infrastructure

Road and Marine Services
Traffic Services, Traffic Solutions Unit

Drawn: A. Simister


Scale: 1:10

Authorisation:

Date: 10 January, 2020

TEMPORARY WARNING SIGN
'Power Line Works'

TM2-37A

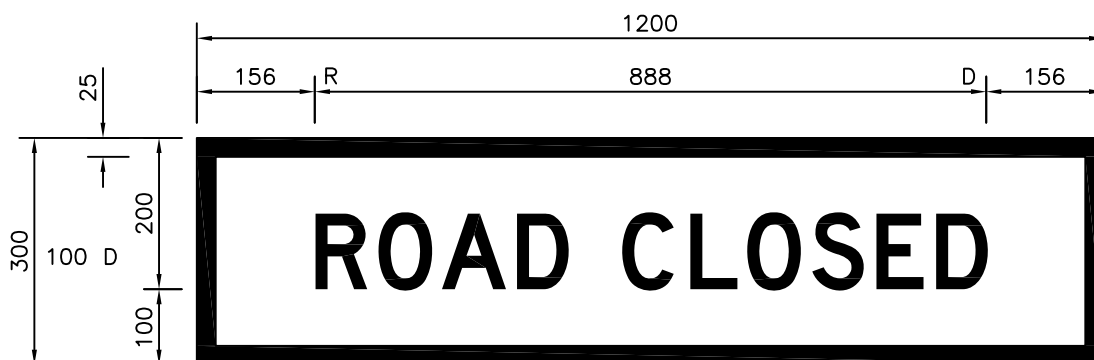

NOTE:

To be used in multi-message sign frames only.



Black

White class 1

Note: Letters & Numerals AS1744:2015.



Government of South Australia
Department of Planning,
Transport and Infrastructure

Road and Marine Services
Traffic Services, Traffic Solutions Unit

Drawn: A. Simister


Scale: 1:10

Authorisation:

Date: 20 December, 2019

TEMPORARY WARNING SIGN
'Road Closed'

TM2-4B

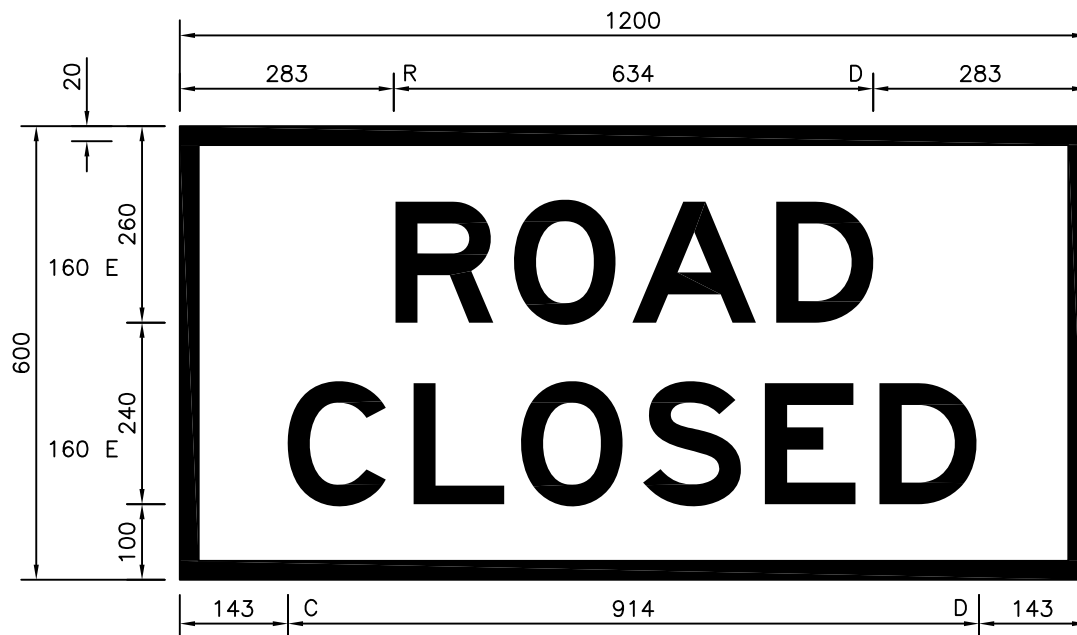

NOTE:

To be used in multi-message sign frames only.



Black

White class 1

Note: Letters & Numerals AS1744:2015.



Government of South Australia
Department of Planning,
Transport and Infrastructure

Road and Marine Services
Traffic Services, Traffic Solutions Unit

Drawn: A. Simister



Scale: 1:10

Authorisation:

Date: 20 December, 2019

TEMPORARY WARNING SIGN
'Road Closed'

TM2-4C

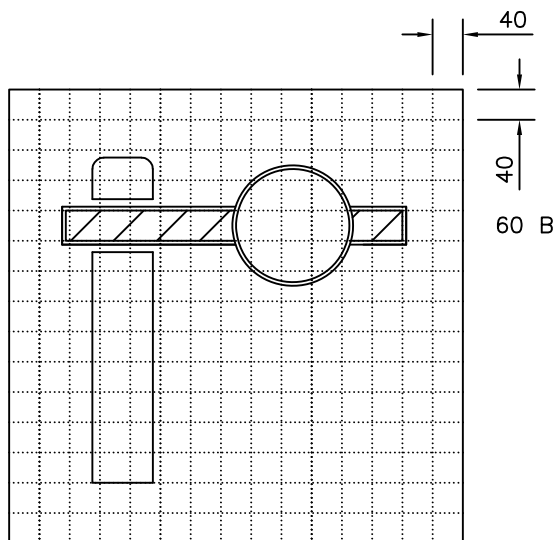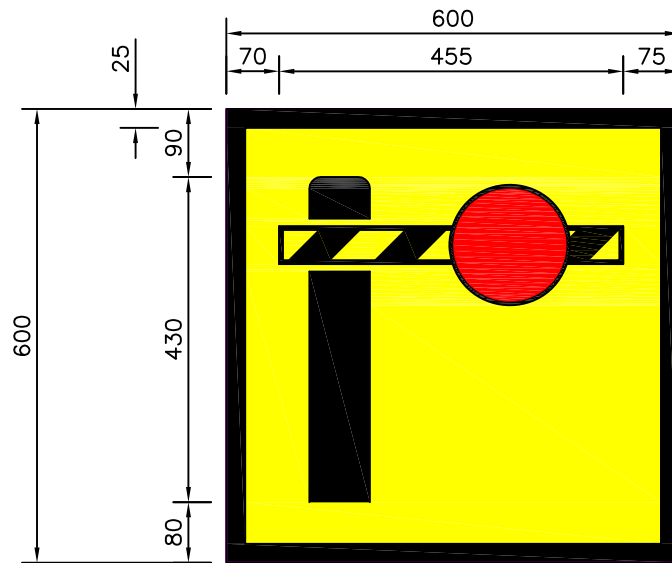


NOTE:

To be used in multi-message sign frames only.



Approved sign combination

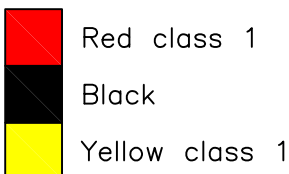

Note: Letters & Numerals AS1744:2015.



Government of South Australia
Department of Planning,
Transport and Infrastructure

Road and Marine Services
Traffic Services, Traffic Solutions Unit

Drawn: A. Simister


Scale: 1:10

Authorisation:

Date: 9 January, 2020


TEMPORARY WARNING SIGN
'Boom Barrier'

TM2-52A

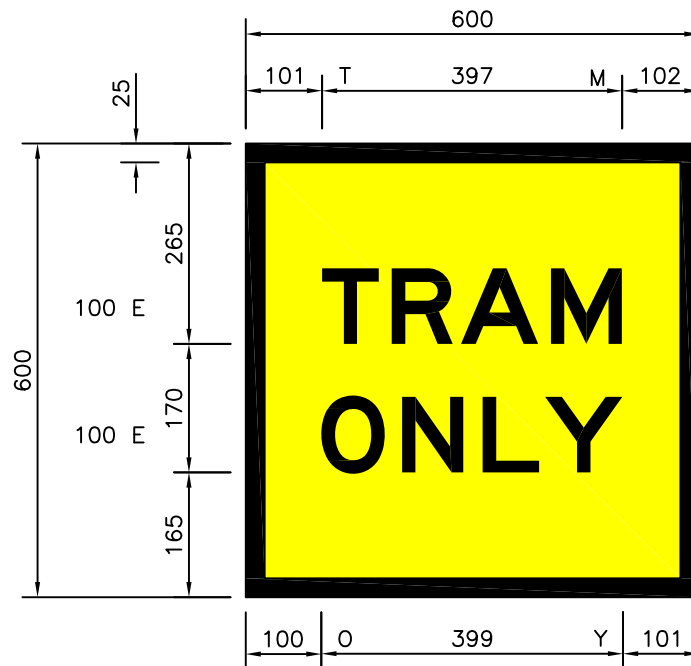

NOTE:

To be used in multi-message sign frames only.

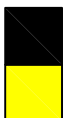

Black

Yellow class 1

Note: Letters & Numerals AS1744:2015.



Government of South Australia
Department of Planning,
Transport and Infrastructure

Road and Marine Services
Traffic Services, Traffic Solutions Unit

Drawn: A. Simister


Scale: 1:5

Authorisation:

Date: 9 January, 2020

TEMPORARY WARNING SIGN
'Tram Only'

TM2-54A

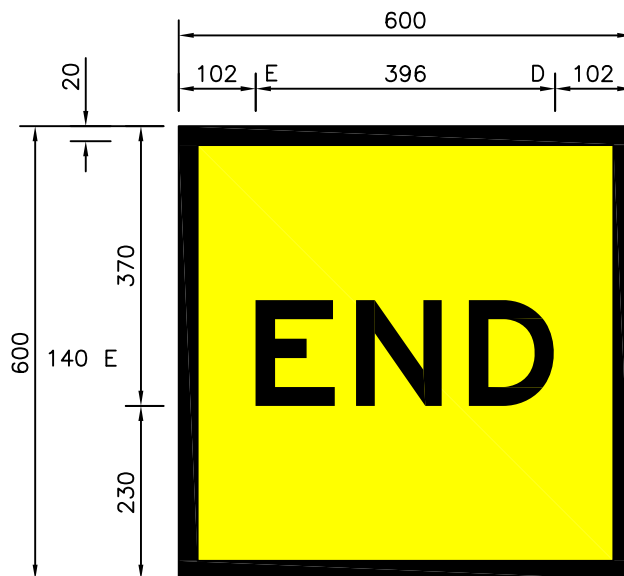

NOTE:

To be used in multi-message sign frames only.



Black

Yellow class 1

Note: Letters & Numerals AS1744:2015.



Government of South Australia
Department of Planning,
Transport and Infrastructure

Road and Marine Services
Traffic Services, Traffic Solutions Unit

Drawn: A. Simister


Scale: 1:10

Authorisation:

Date: 9 January, 2020

TEMPORARY WARNING SIGN
'End'

TM2-SA106A

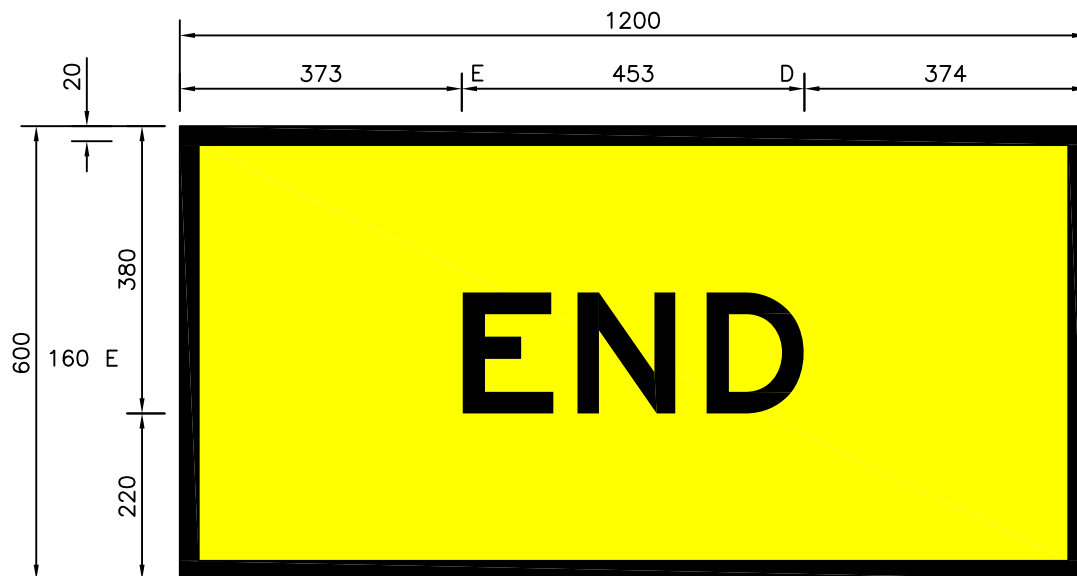

NOTE:

To be used in multi-message sign frames only.



Black

Yellow class 1

Note: Letters & Numerals AS1744:2015.



Government of South Australia
Department of Planning,
Transport and Infrastructure

Road and Marine Services
Traffic Services, Traffic Solutions Unit

Drawn: A. Simister


Scale: 1:10

Authorisation:

Date: 9 January, 2020

TEMPORARY WARNING SIGN
'End'

TM2-SA106C

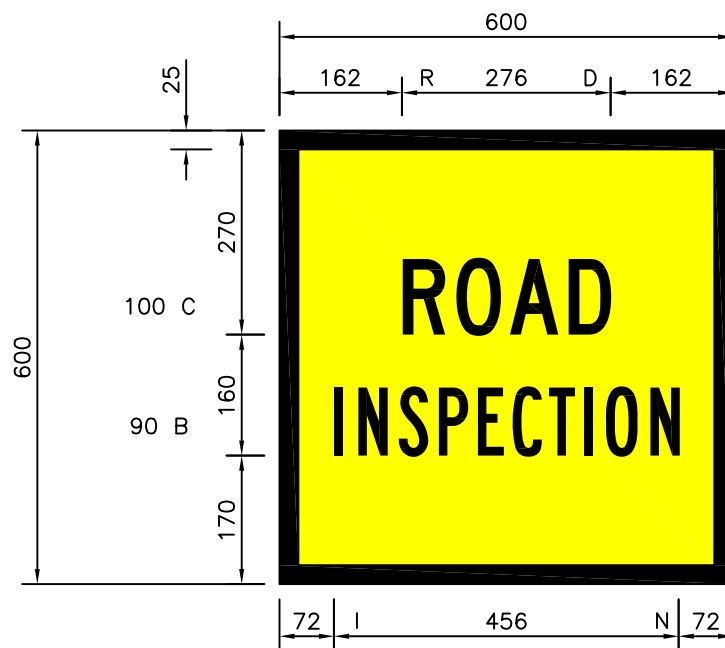

NOTE:

To be used in multi-message sign frames only.



Black

Yellow class 1

Note: Letters & Numerals AS1744:2015.



Government of South Australia
Department of Planning,
Transport and Infrastructure

Road and Marine Services
Traffic Services, Traffic Solutions Unit

Drawn: A. Simister


Scale: 1:10

Authorisation:

Date: 10 January, 2020

TEMPORARY WARNING SIGN
'Road Inspection'

TM2-SA107A

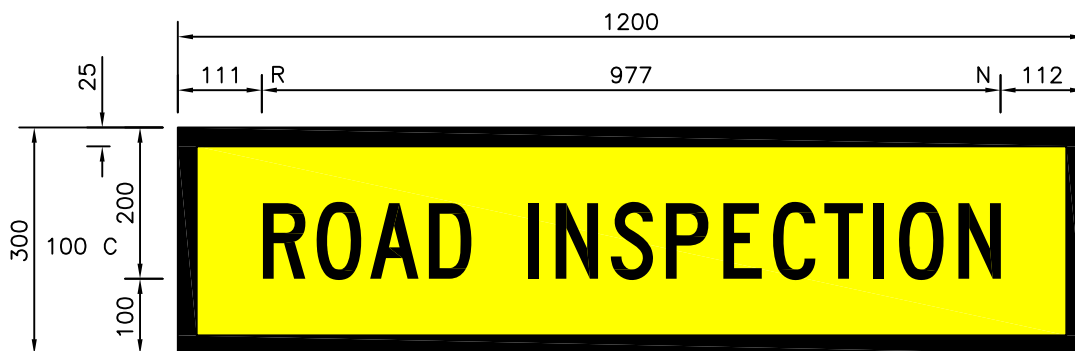

NOTE:

To be used in multi-message sign frames only.



Black

Yellow class 1

Note: Letters & Numerals AS1744:2015.



Government of South Australia
Department of Planning,
Transport and Infrastructure

Road and Marine Services
Traffic Services, Traffic Solutions Unit

Drawn: A. Simister


Scale: 1:10

Authorisation:

Date: 10 January, 2020

TEMPORARY WARNING SIGN
'Road Inspection'

TM2-SA107B

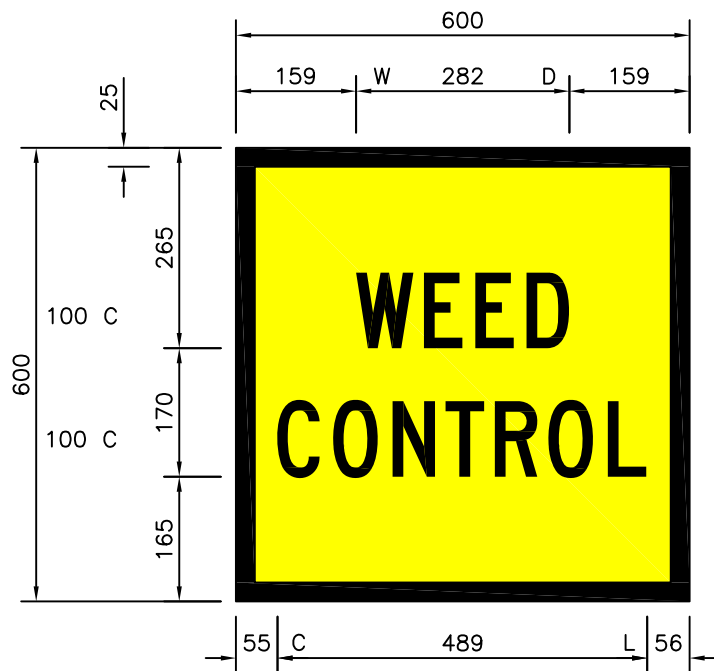

NOTE:

To be used in multi-message sign frames only.



Black

Yellow class 1

Note: Letters & Numerals AS1744:2015.



Government of South Australia
Department of Planning,
Transport and Infrastructure

Road and Marine Services
Traffic Services, Traffic Solutions Unit

Drawn: A. Simister


Scale: 1:10

Authorisation:

Date: 10 January, 2020


TEMPORARY WARNING SIGN
'Weed Control'

TM2-SA110A

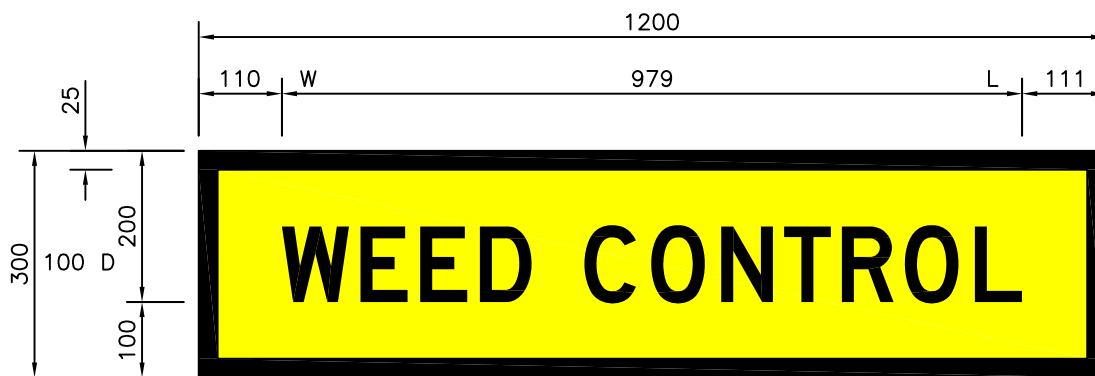

NOTE:

To be used in multi-message sign frames only.

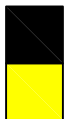

Black

Yellow class 1

Note: Letters & Numerals AS1744:2015.



Government of South Australia

Department of Planning,
Transport and Infrastructure

Road and Marine Services
Traffic Services, Traffic Solutions Unit

Drawn: A. Simister

Scale: 1:10

TEMPORARY WARNING SIGN


'Weed Control'

Authorisation:

A handwritten signature in blue ink.

Date: 10 January, 2020

TM2-SA110B

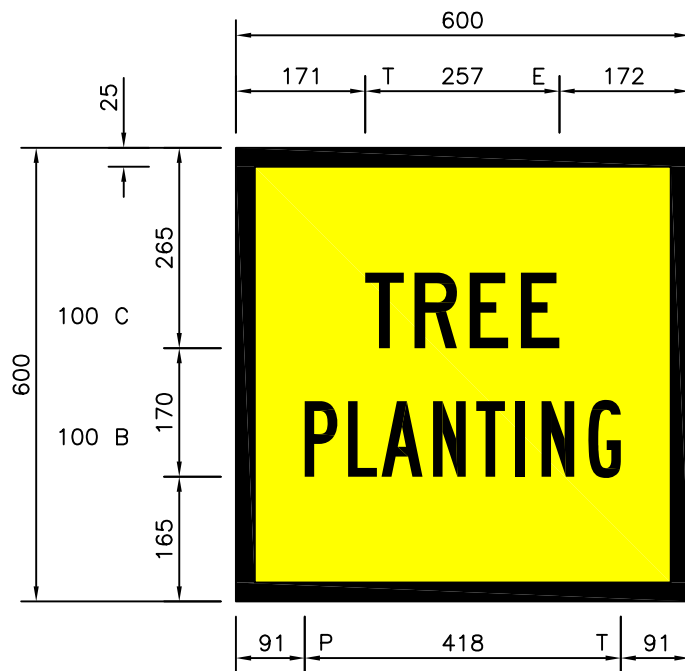

NOTE:

To be used in multi-message sign frames only.



Black

Yellow class 1

Note: Letters & Numerals AS1744:2015.



Government of South Australia
Department of Planning,
Transport and Infrastructure

Road and Marine Services
Traffic Services, Traffic Solutions Unit

Drawn: A. Simister


Scale: 1:10

Authorisation:

Date: 10 January, 2020

TEMPORARY WARNING SIGN
'Tree Planting'

TM2-SA111A

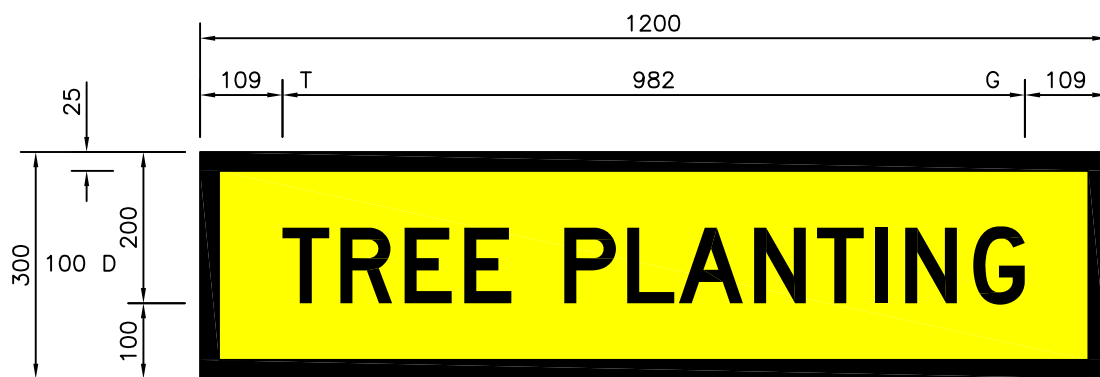

NOTE:

To be used in multi-message sign frames only.



Black

Yellow class 1

Note: Letters & Numerals AS1744:2015.



Government of South Australia

Department of Planning,
Transport and Infrastructure

Road and Marine Services
Traffic Services, Traffic Solutions Unit

Drawn: A. Simister

Scale: 1:10


TEMPORARY WARNING SIGN
'Tree Planting'

Authorisation:

A handwritten signature in blue ink.

Date: 10 January, 2020

TM2-SA111B

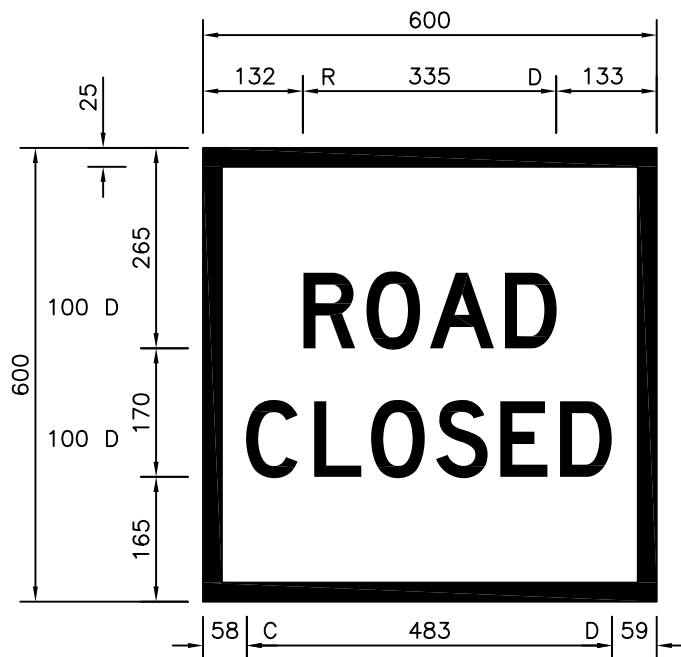

NOTE:

To be used in multi-message sign frames only.



Black

White class 1

Note: Letters & Numerals AS1744:2015.



Government of South Australia
Department of Planning,
Transport and Infrastructure

Road and Marine Services
Traffic Services, Traffic Solutions Unit

Drawn: A. Simister


Scale: 1:10

Authorisation:

Date: 9 January, 2020

TEMPORARY WARNING SIGN
'Road Closed'

TM2-SA4A

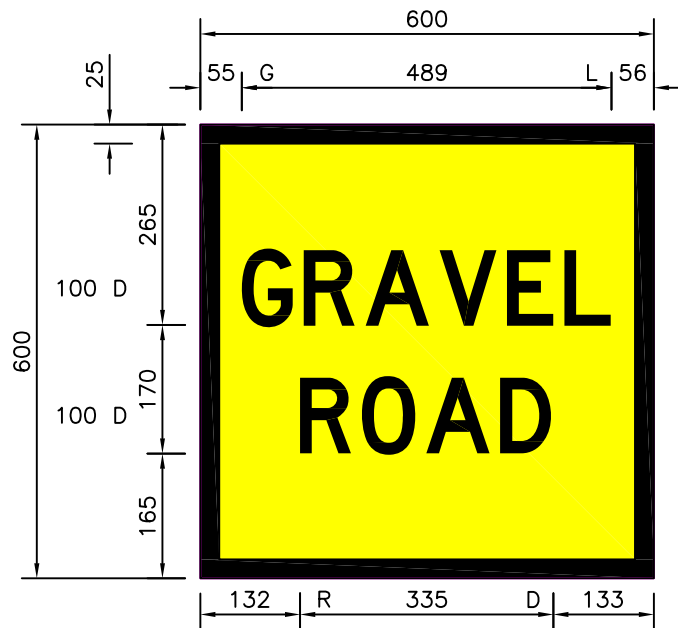

NOTE:

To be used in multi-message sign frames only.



Black

Yellow class 1

Note: Letters & Numerals AS1744:2015.



Government of South Australia

Department of Planning,
Transport and Infrastructure

Road and Marine Services
Traffic Services, Traffic Solutions Unit

Drawn: A. Simister

Scale: 1:10


TEMPORARY WARNING SIGN

'Gravel Road'

Authorisation:

Date: 9 January, 2020

TM3-13A

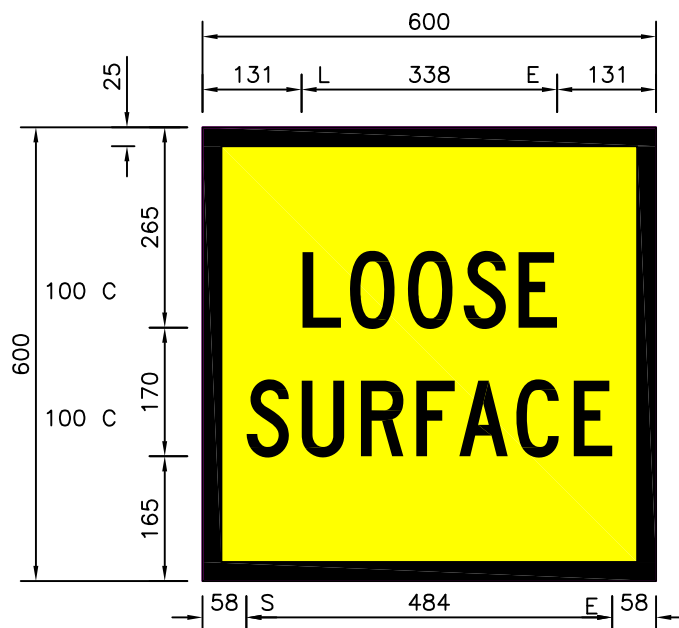

NOTE:

To be used in multi-message sign frames only.



Black

Yellow class 1

Note: Letters & Numerals AS1744:2015.



Government of South Australia

Department of Planning,
Transport and Infrastructure

Road and Marine Services
Traffic Services, Traffic Solutions Unit

Drawn: A. Simister


Scale: 1:5

Authorisation:

Date: 9 January, 2020

TEMPORARY WARNING SIGN
'Loose surface'

TM3-14A

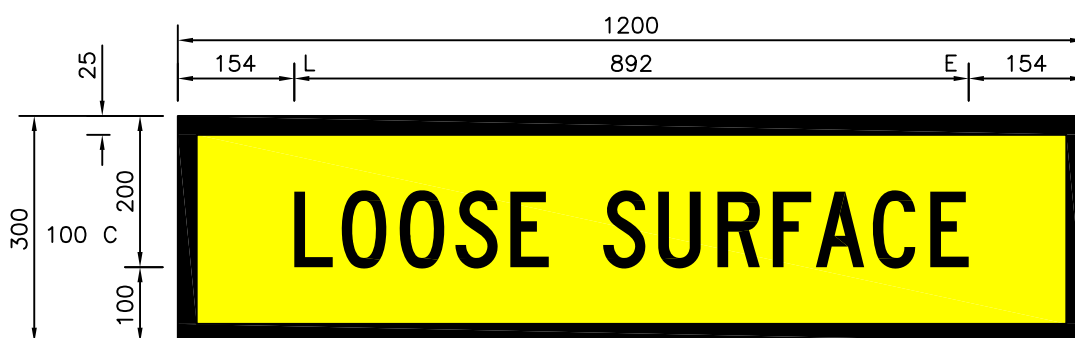

NOTE:

To be used in multi-message sign frames only.



Black

Yellow class 1

Note: Letters & Numerals AS1744:2015.



Government of South Australia
Department of Planning,
Transport and Infrastructure

Road and Marine Services
Traffic Services, Traffic Solutions Unit

Drawn: A. Simister

Scale: 1:10


Authorisation:

A handwritten signature in blue ink.

Date: 9 January, 2020

TEMPORARY WARNING SIGN
'Loose Surface'

TM3-14B

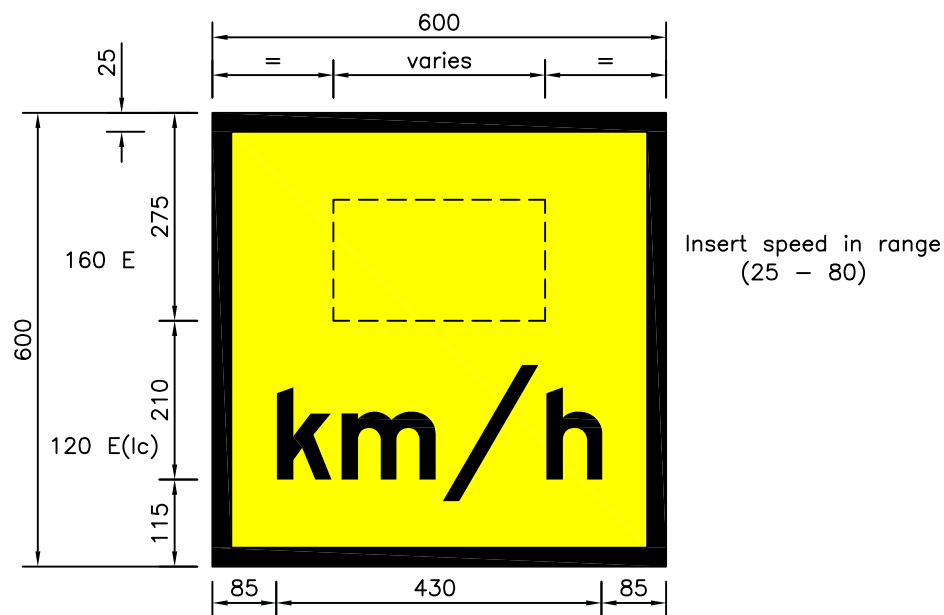

NOTE:

To be used in multi-message sign frames only.

ADDITIONAL NOTE:

To be used in conjunction with 'ON SIDE ROAD' or 'ROADWORK ON SIDE ROAD'.



Black

Yellow class 1

Note: Letters & Numerals AS1744:2015.



Government of South Australia
Department of Planning,
Transport and Infrastructure

Road and Marine Services
Traffic Services, Traffic Solutions Unit

Drawn: A. Simister


Scale: 1:10

Authorisation:

Date: 9 January, 2020


TEMPORARY WARNING SIGN
'XX km/h'

TM3-16-1A

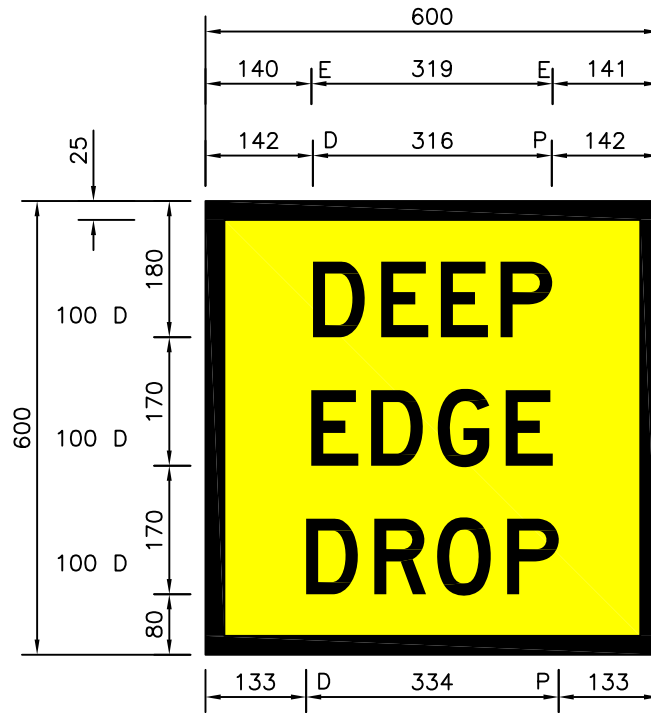

NOTE:

To be used in multi-message sign frames only.

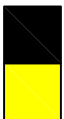

Black

Yellow class 1

Note: Letters & Numerals AS1744:2015.



Government of South Australia

Department of Planning,
Transport and Infrastructure

Road and Marine Services
Traffic Services, Traffic Solutions Unit

Drawn: A. Simister


Scale: 1:10

Authorisation:

Date: 10 January, 2020

TEMPORARY WARNING SIGN
'Deep Edge Drop'


TM3-25A

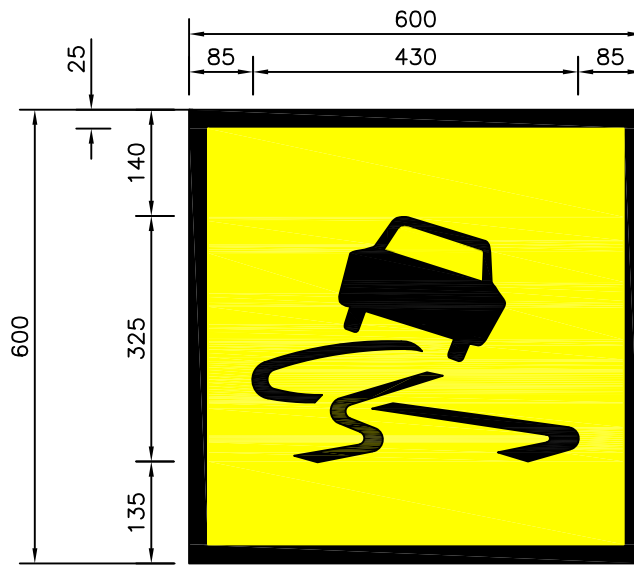

T3-3Amod @80%

NOTE:

To be used in
multi-message sign frames
only.

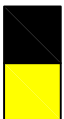

Black

Yellow class 1

Note: Letters & Numerals AS1744:2015.



Government of South Australia

Department of Planning,
Transport and Infrastructure

Road and Marine Services
Traffic Services, Traffic Solutions Unit

Drawn: A. Simister

Scale: 1:10


Authorisation:

Signature of the authorising officer.

Date: 9 January, 2020

TEMPORARY WARNING SIGN
'Slippery'

TM3-3A

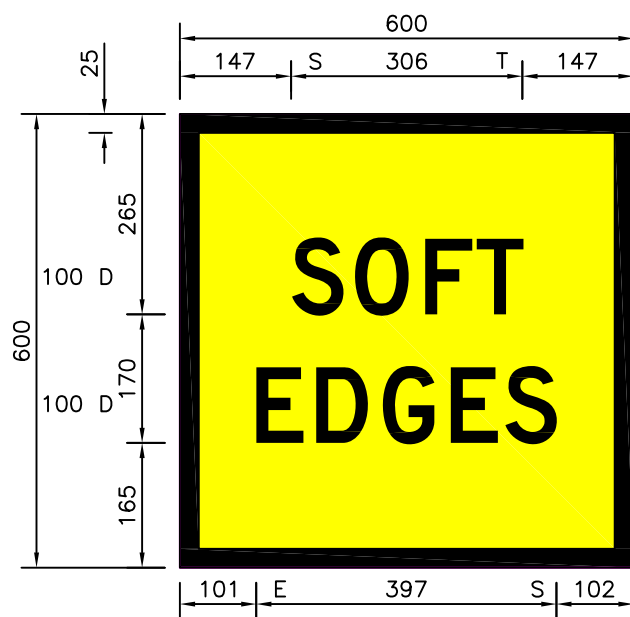

NOTE:

To be used in multi-message sign frames only.



Black

Yellow class 1

Note: Letters & Numerals AS1744:2015.



Government of South Australia

Department of Planning,
Transport and Infrastructure

Road and Marine Services
Traffic Services, Traffic Solutions Unit

Drawn: A. Simister


Scale: 1:10

Authorisation:

Date: 9 January, 2020

TEMPORARY WARNING SIGN
'Soft Edges'

TM3-6A

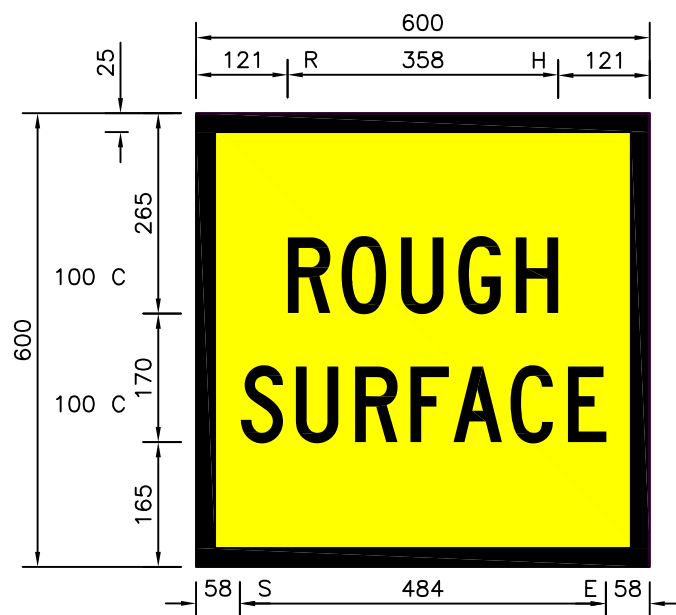

NOTE:

To be used in multi-message sign frames only.



Black

Yellow class 1

Note: Letters & Numerals AS1744:2015.



Government of South Australia

Department of Planning,
Transport and Infrastructure

Road and Marine Services
Traffic Services, Traffic Solutions Unit

Drawn: A. Simister


Scale: 1:10

Authorisation:

Date: 9 January, 2020

TEMPORARY WARNING SIGN
'Rough Surface'


TM3-7A

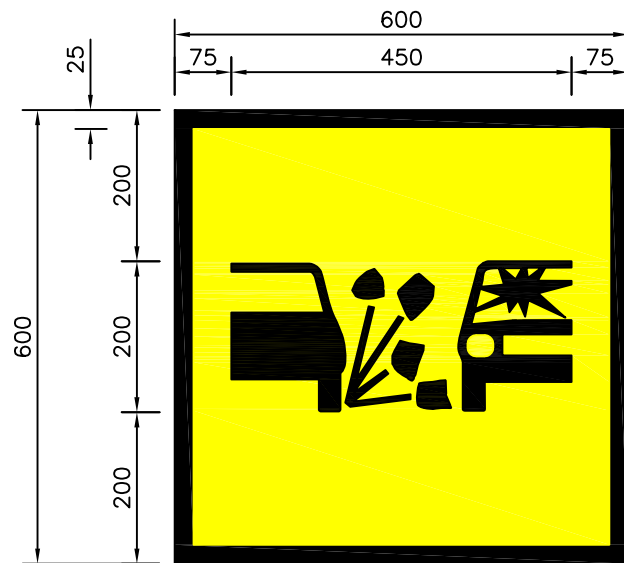

T3-9Amod @60%

NOTE:

To be used in
multi-message sign frames
only.

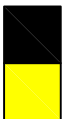

Black

Yellow class 1

Note: Letters & Numerals AS1744:2015.



Government of South Australia

Department of Planning,
Transport and Infrastructure

Road and Marine Services
Traffic Services, Traffic Solutions Unit

Drawn: A. Simister

Scale: 1:10

Authorisation:

Date: 9 January, 2020

TEMPORARY WARNING SIGN
'Loose Stones'

TM3-9A



NOTE:

To be used in multi-message sign frames only.



Black

Yellow class 1

Note: Letters & Numerals AS1744:2015.



Government of South Australia

Department of Planning,
Transport and Infrastructure

Road and Marine Services
Traffic Services, Traffic Solutions Unit

Drawn: A. Simister

Scale: 1:10

TEMPORARY WARNING SIGN


'Wet Paint On Road'

Authorisation:

A handwritten signature in blue ink.

Date: 10 January, 2020

TM3-SA101C

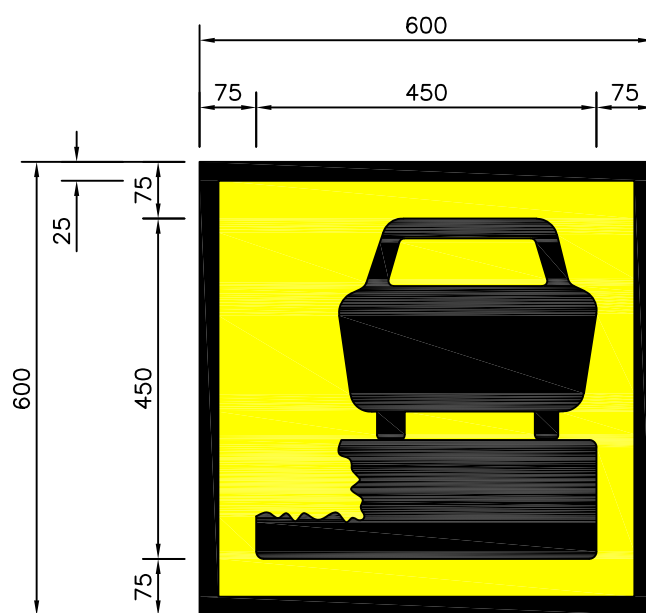

NOTE:

To be used in multi-message sign frames only.



Black

Yellow class 1

Note: Letters & Numerals AS1744:2015.



Government of South Australia

Department of Planning,
Transport and Infrastructure

Road and Marine Services
Traffic Services, Traffic Solutions Unit

Drawn: A. Simister


Scale: 1:10

Authorisation:

Date: 10 January, 2020

TEMPORARY WARNING SIGN
'Deep Edge Drop Symbol'

TM3-SA102A

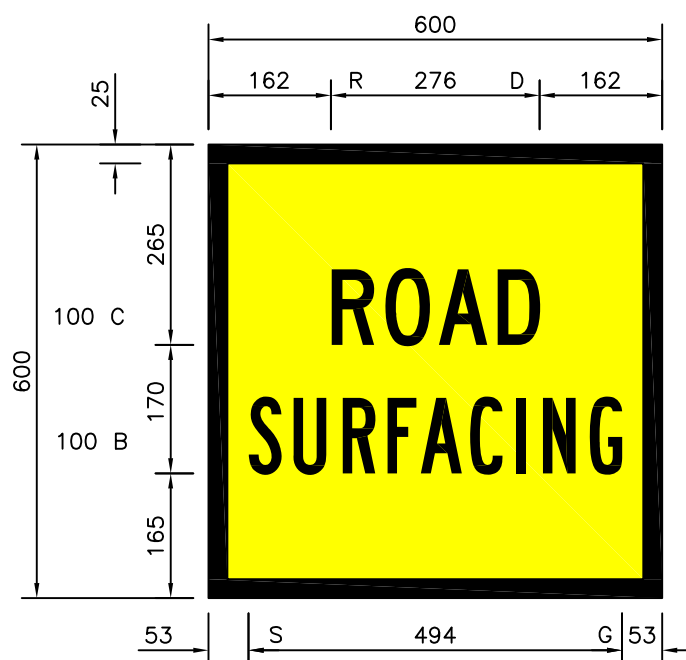

NOTE:

To be used in multi-message sign frames only.



Black

Yellow class 1

Note: Letters & Numerals AS1744:2015.



Government of South Australia
Department of Planning,
Transport and Infrastructure

Road and Marine Services
Traffic Services, Traffic Solutions Unit

Drawn: A. Simister


Scale: 1:10

Authorisation:

Date: 10 January, 2020

TEMPORARY WARNING SIGN
'Road Surfacing'

TM3-SA103A

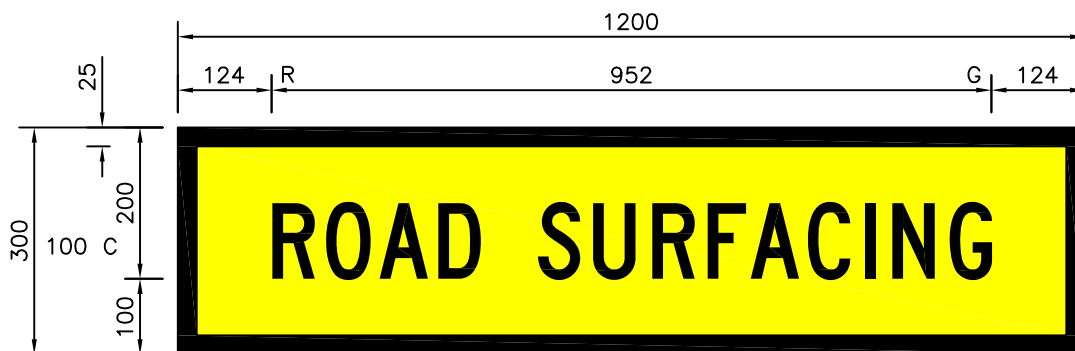

NOTE:

To be used in multi-message sign frames only.



Black

Yellow class 1

Note: Letters & Numerals AS1744:2015.



Government of South Australia
Department of Planning,
Transport and Infrastructure

Road and Marine Services
Traffic Services, Traffic Solutions Unit

Drawn: A. Simister

Scale: 1:10


Authorisation:

A handwritten signature in blue ink.

Date: 10 January, 2020

TEMPORARY WARNING SIGN
'Road Surfacing'

TM3-SA103B

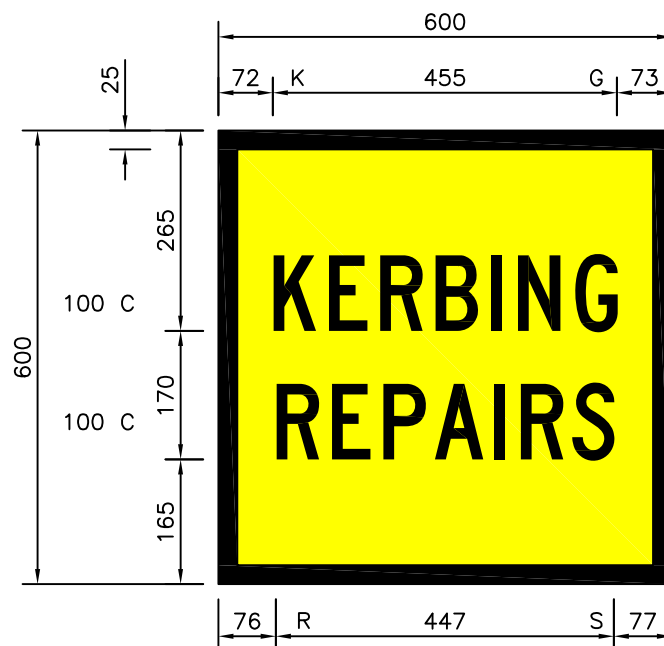

NOTE:

To be used in multi-message sign frames only.



Black

Yellow class 1

Note: Letters & Numerals AS1744:2015.



Government of South Australia
Department of Planning,
Transport and Infrastructure

Road and Marine Services
Traffic Services, Traffic Solutions Unit

Drawn: A. Simister


Scale: 1:10

Authorisation:

Date: 10 January, 2020

TEMPORARY WARNING SIGN
'Kerbing Repairs'

TM3-SA104A

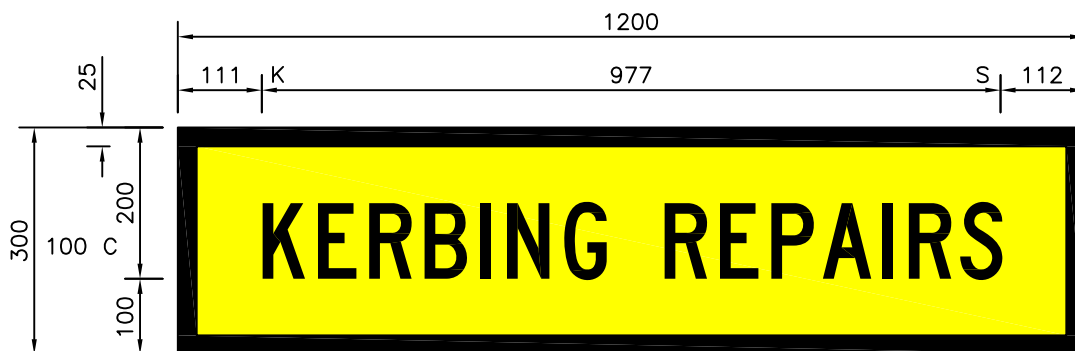

NOTE:

To be used in multi-message sign frames only.



Black

Yellow class 1

Note: Letters & Numerals AS1744:2015.



Government of South Australia
Department of Planning,
Transport and Infrastructure

Road and Marine Services
Traffic Services, Traffic Solutions Unit

Drawn: A. Simister


Scale: 1:10

Authorisation:

Date: 10 January, 2020

TEMPORARY WARNING SIGN
'Kerbing Repairs'

TM3-SA104B

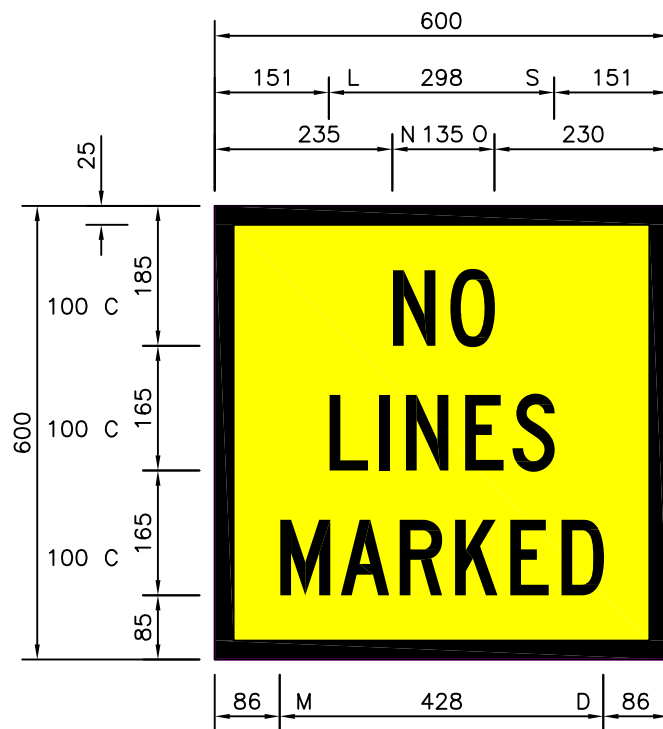

NOTE:

To be used in multi-message sign frames only.



Black

Yellow class 1

Note: Letters & Numerals AS1744:2015.



Government of South Australia
Department of Planning,
Transport and Infrastructure

Road and Marine Services
Traffic Services, Traffic Solutions Unit

Drawn: A. Simister


Scale: 1:10

Authorisation:

Date: 9 January, 2020


TEMPORARY WARNING SIGN
'No Lines Marked'

TM3-SA106A

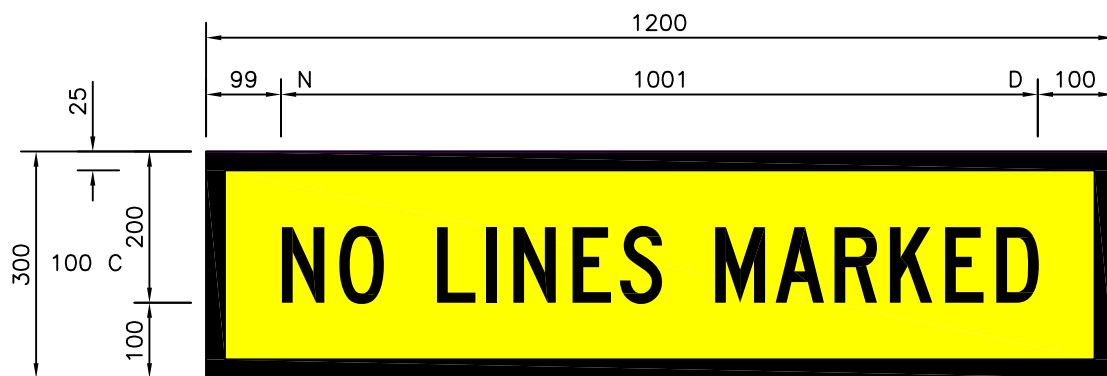

NOTE:

To be used in multi-message sign frames only.

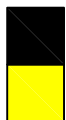

Black

Yellow class 1

Note: Letters & Numerals AS1744:2015.



Government of South Australia
Department of Planning,
Transport and Infrastructure

Road and Marine Services
Traffic Services, Traffic Solutions Unit

Drawn: A. Simister

Scale: 1:10

Authorisation:

Date: 9 January, 2020

TEMPORARY WARNING SIGN
'No Lines Marked'

TM3-SA106B



NOTE:

To be used in multi-message sign frames only.



Black

Yellow class 1

Note: Letters & Numerals AS1744:2015.



Government of South Australia
Department of Planning,
Transport and Infrastructure

Road and Marine Services
Traffic Services, Traffic Solutions Unit

Drawn: A. Simister


Scale: 1:10

Authorisation:

Date: 9 January, 2020

TEMPORARY WARNING SIGN
'No Lines Marked'

TM3-SA106C

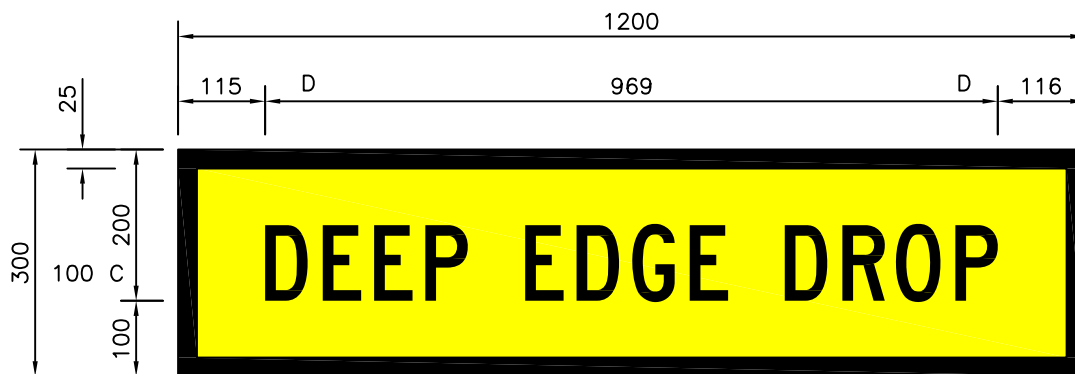

NOTE:

To be used in multi-message sign frames only.



Black

Yellow class 1

Note: Letters & Numerals AS1744:2015.



Government of South Australia

Department of Planning,
Transport and Infrastructure

Road and Marine Services
Traffic Services, Traffic Solutions Unit

Drawn: A. Simister


Scale: 1:10

Authorisation:

Date: 10 January, 2020


TEMPORARY WARNING SIGN
'Deep Edge Drop'

TM3-SA25B

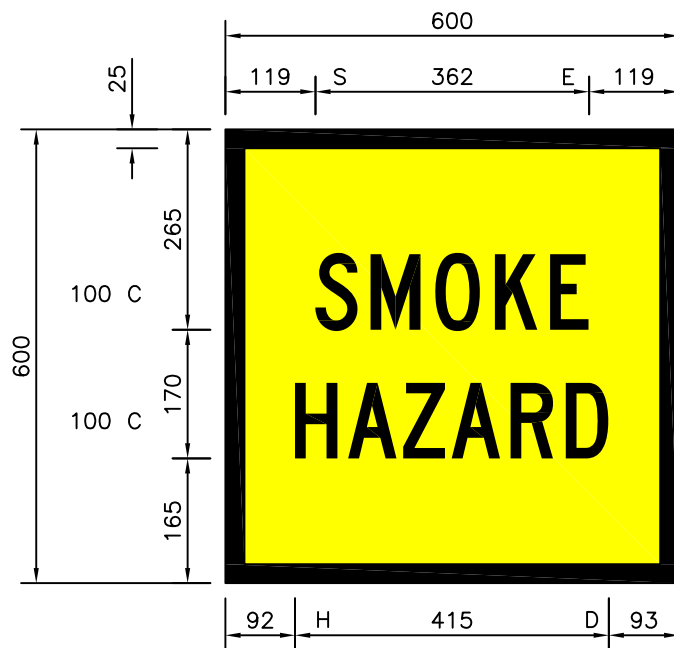

NOTE:

To be used in multi-message sign frames only.

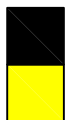

Black

Yellow class 1

Note: Letters & Numerals AS1744:2015.



Government of South Australia
Department of Planning,
Transport and Infrastructure

Road and Marine Services
Traffic Services, Traffic Solutions Unit

Drawn: A. Simister


Scale: 1:10

Authorisation:

Date: 10 January, 2020

TEMPORARY WARNING SIGN
'Smoke Hazard'

TM4-6A

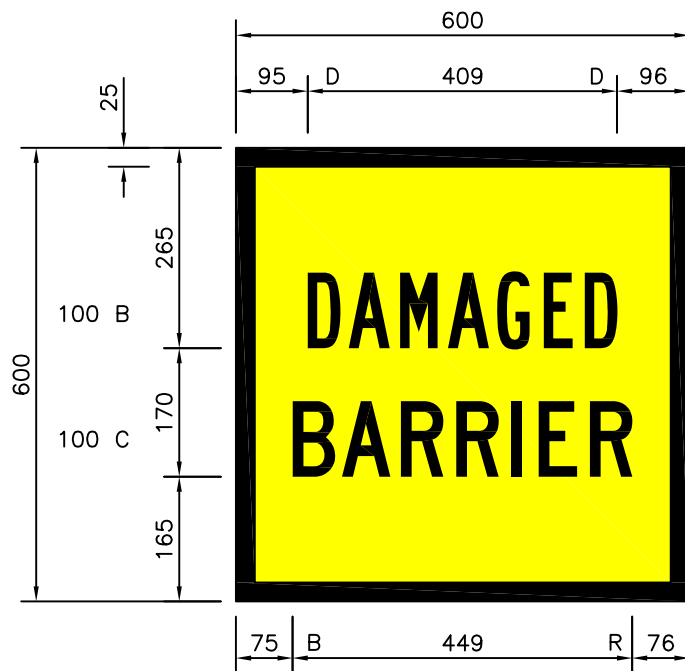

NOTE:

To be used in multi-message sign frames only.



Black

Yellow class 1

Note: Letters & Numerals AS1744:2015.



Government of South Australia
Department of Planning,
Transport and Infrastructure

Road and Marine Services
Traffic Services, Traffic Solutions Unit

Drawn: A. Simister


Scale: 1:10

Authorisation:

Date: 10 January, 2020

TEMPORARY WARNING SIGN
'Damaged Barrier'

TM4-SA109A

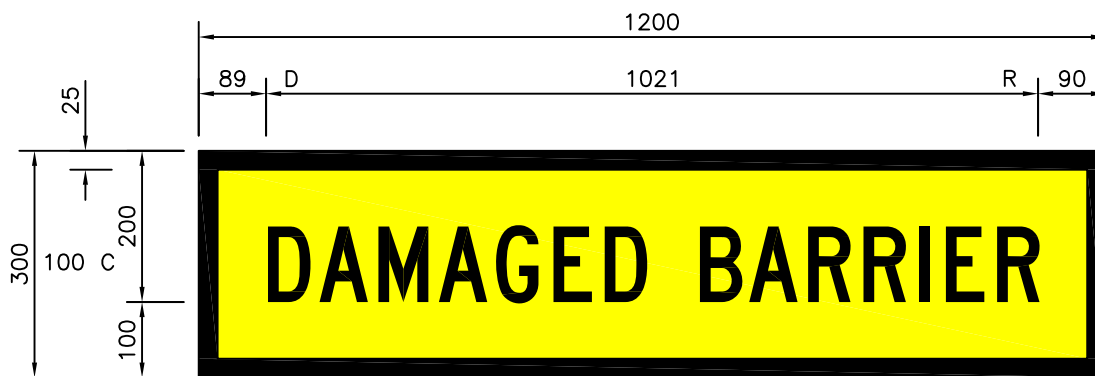

NOTE:

To be used in multi-message sign frames only.



Black

Yellow class 1

Note: Letters & Numerals AS1744:2015.



Government of South Australia

Department of Planning,
Transport and Infrastructure

Road and Marine Services
Traffic Services, Traffic Solutions Unit

Drawn: A. Simister

Scale: 1:10

TEMPORARY WARNING SIGN
'Damaged Barrier'

Authorisation:

Date: 10 January, 2020

TM4-SA109B



NOTE:

To be used in multi-message sign frames only.



Black

Yellow class 1

Note: Letters & Numerals AS1744:2015.



Government of South Australia
Department of Planning,
Transport and Infrastructure

Road and Marine Services
Traffic Services, Traffic Solutions Unit

Drawn: A. Simister


Scale: 1:10

Authorisation:

Date: 10 January, 2020

TEMPORARY WARNING SIGN
'Prescribed Burn'

TM4-SA112B

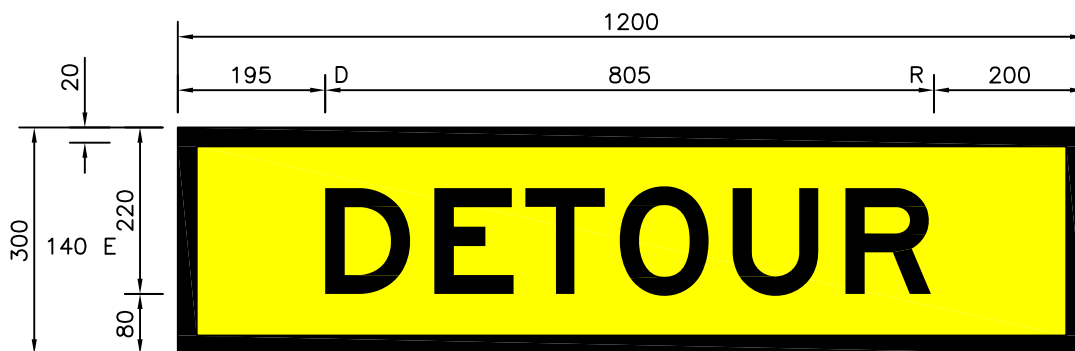

NOTE:

To be used in multi-message sign frames only.



Black

Yellow class 1

Note: Letters & Numerals AS1744:2015.



Government of South Australia
Department of Planning,
Transport and Infrastructure

Road and Marine Services
Traffic Services, Traffic Solutions Unit

Drawn: A. Simister


Scale: 1:10

Authorisation:

Date: 10 January, 2020


TEMPORARY WARNING SIGN
'Detour'

TM5-7B

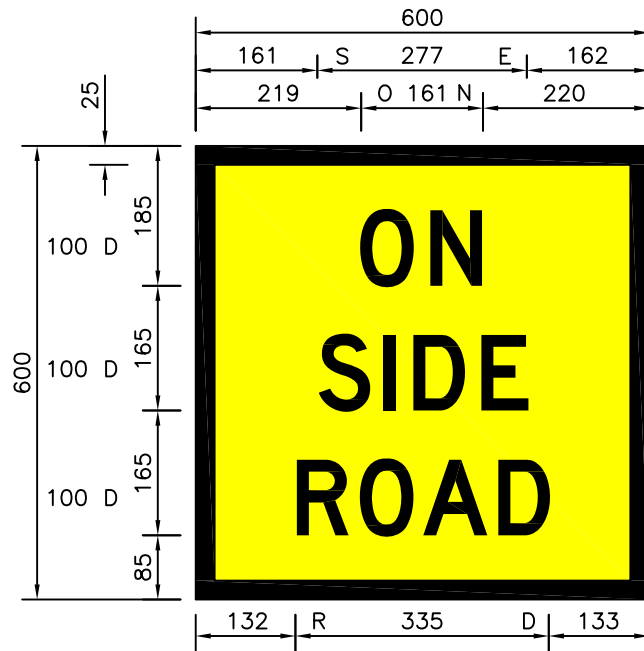

NOTE:

To be used in multi-message sign frames only.

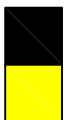

Black

Yellow class 1

Note: Letters & Numerals AS1744:2015.



Government of South Australia
Department of Planning,
Transport and Infrastructure

Road and Marine Services
Traffic Services, Traffic Solutions Unit

Drawn: A. Simister


Scale: 1:10

Authorisation:

Date: 9 January, 2020

TEMPORARY WARNING SIGN
'On Side Road'

TM5-9A

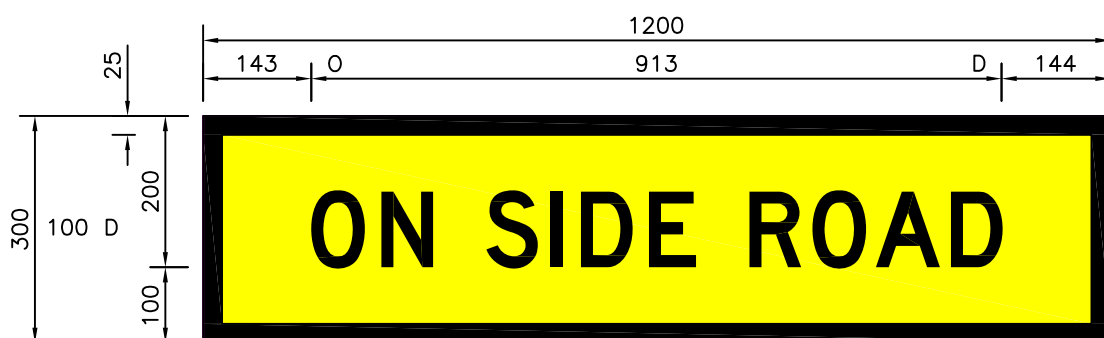

NOTE:
To be used in multi-message sign frames only.



Black

Yellow class 1

Note: Letters & Numerals AS1744:2015.



Government of South Australia
Department of Planning,
Transport and Infrastructure

Road and Marine Services
Traffic Services, Traffic Solutions Unit

Drawn: A. Simister



Scale: 1:10

Authorisation:

Date: 9 January, 2020

TEMPORARY WARNING SIGN
'On Side Road'

TM5-9B

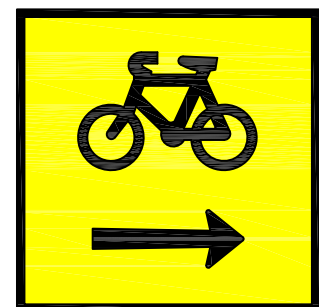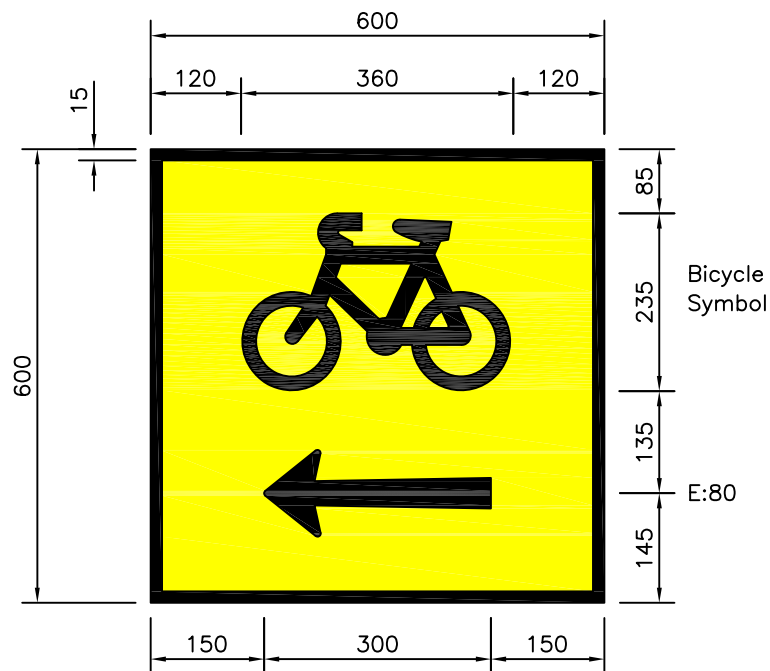

Black

Yellow class 1

Note: Letters & Numerals AS1744:2015.



Government of South Australia
Department of Planning,
Transport and Infrastructure

Road and Marine Services
Traffic Services, Traffic Solutions Unit

Drawn: A. Simister


Scale: 1:10

Authorisation:

Date: 9 January, 2020

TEMPORARY WARNING SIGN
'Bicycle Detour'

TM5-SA101A(LorR)

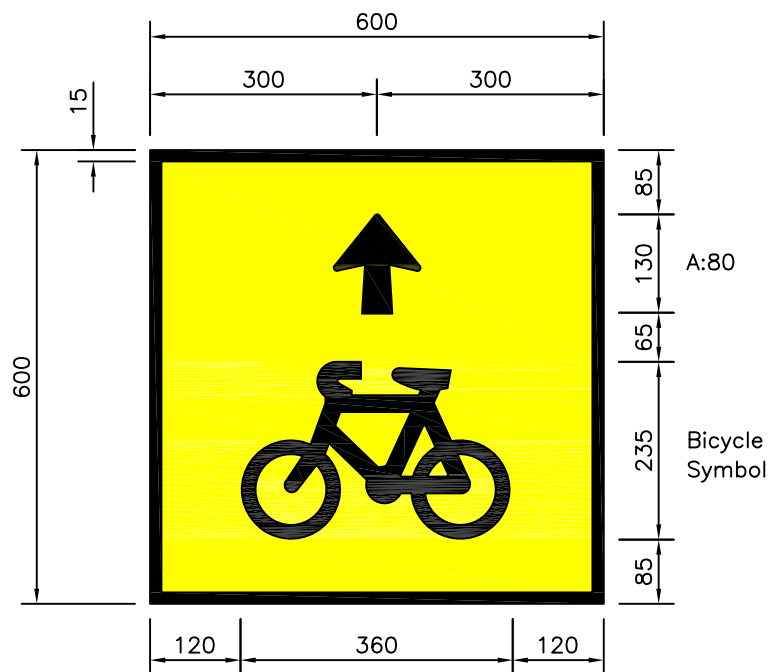

Black

Yellow class 1

Note: Letters & Numerals AS1744:2015.



Government of South Australia

Department of Planning,
Transport and Infrastructure

Road and Marine Services
Traffic Services, Traffic Solutions Unit

Drawn: A. Simister


Scale: 1:10

TEMPORARY WARNING SIGN
'Bicycle Detour (straight ahead)'

Authorisation:

Date: 9 January, 2020

TM5-SA102A

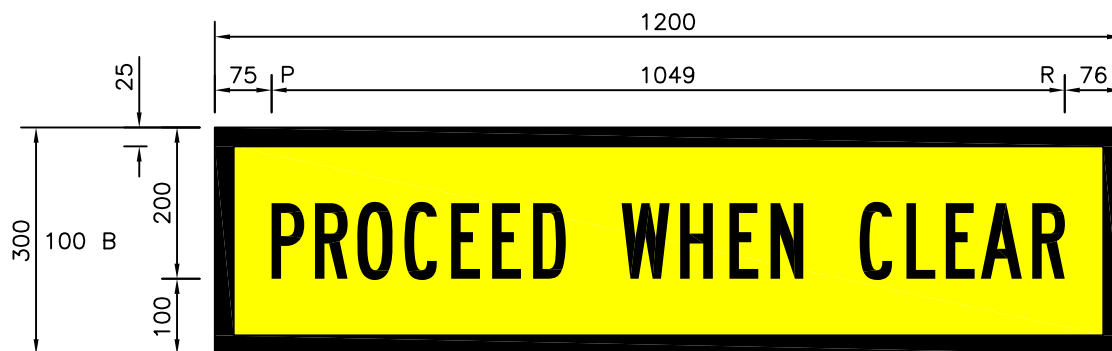

NOTE:

To be used in multi-message sign frames only.



Black

Yellow class 1

Note: Letters & Numerals AS1744:2015.



Government of South Australia
Department of Planning,
Transport and Infrastructure

Road and Marine Services
Traffic Services, Traffic Solutions Unit

Drawn: A. Simister


Scale: 1:10

Authorisation:

Date: 10 January, 2020

TEMPORARY WARNING SIGN
'Proceed When Clear'

TM5-SA103B

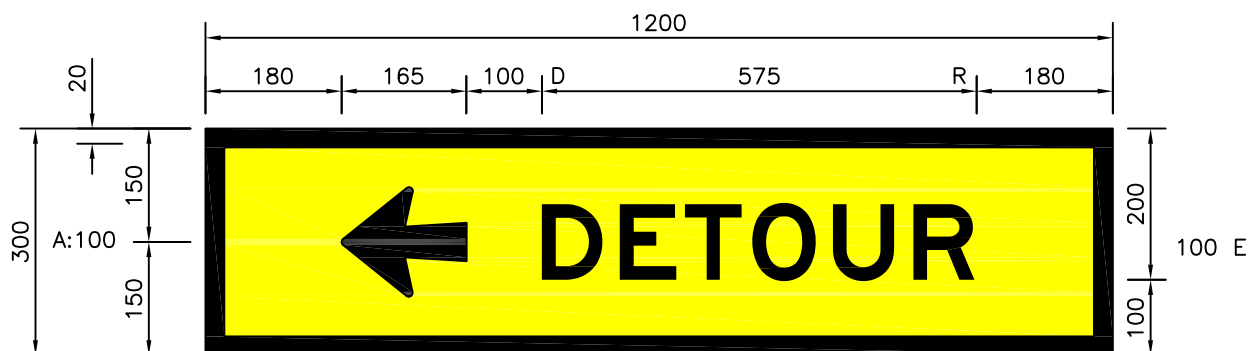

Dimensions apply to straight ahead, left or right construction.

NOTE:

To be used in multi-message sign frames only.



Black

Yellow class 1

Note: Letters & Numerals AS1744:2015.



Government of South Australia
Department of Planning,
Transport and Infrastructure

Road and Marine Services
Traffic Services, Traffic Solutions Unit

Drawn: A. Simister


Scale: 1:10

Authorisation:

Date: 10 January, 2020

TEMPORARY WARNING SIGN
'Detour'

TM5-SA1B
(SorLorR)

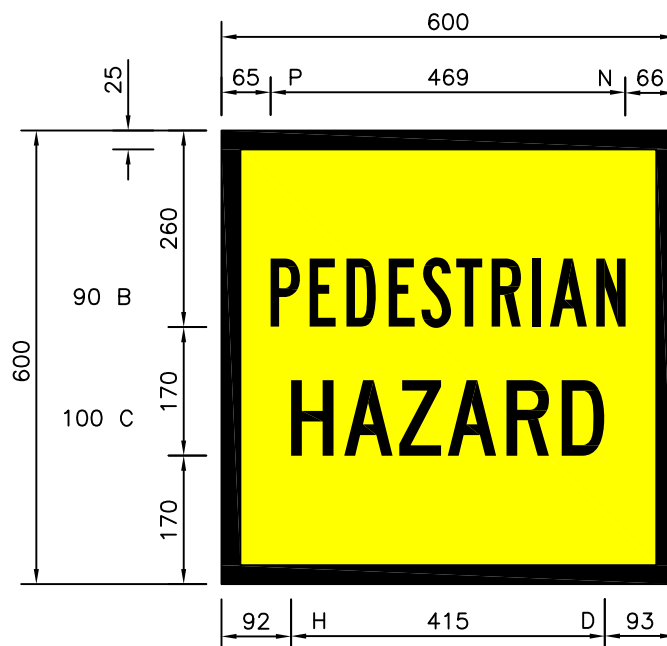

NOTE:

To be used in multi-message sign frames only.



Black

Yellow class 1

Note: Letters & Numerals AS1744:2015.



Government of South Australia
Department of Planning,
Transport and Infrastructure

Road and Marine Services
Traffic Services, Traffic Solutions Unit

Drawn: A. Simister


Scale: 1:10

Authorisation:

Date: 10 January, 2020

TEMPORARY WARNING SIGN
'Pedestrian Hazard'

TM8-13A

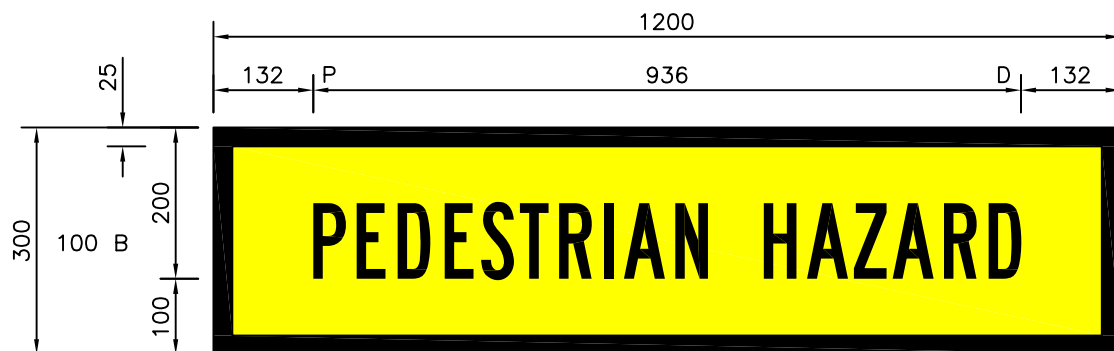

NOTE:

To be used in multi-message sign frames only.



Black

Yellow class 1

Note: Letters & Numerals AS1744:2015.



Government of South Australia
Department of Planning,
Transport and Infrastructure

Road and Marine Services
Traffic Services, Traffic Solutions Unit

Drawn: A. Simister


Scale: 1:10

Authorisation:

Date: 10 January, 2020

TEMPORARY WARNING SIGN
'Pedestrian Hazard'

TM8-13B

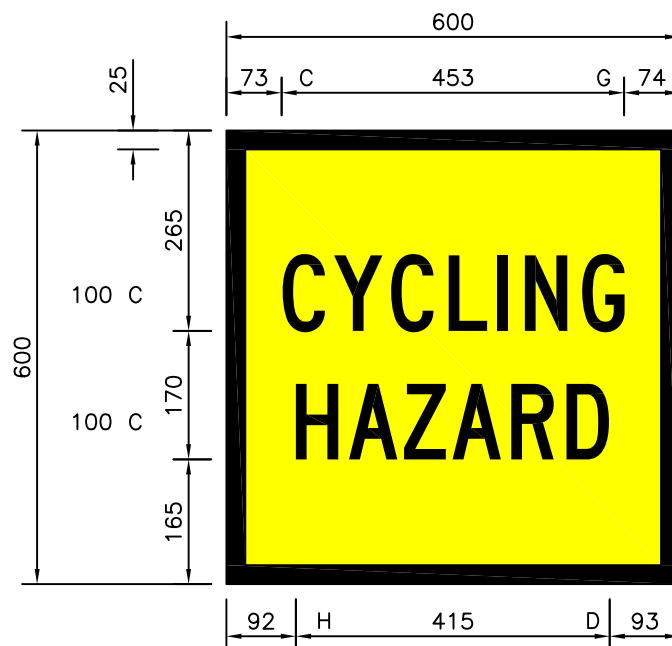

NOTE:

To be used in multi-message sign frames only.



Black

Yellow class 1

Note: Letters & Numerals AS1744:2015.



Government of South Australia
Department of Planning,
Transport and Infrastructure

Road and Marine Services
Traffic Services, Traffic Solutions Unit

Drawn: A. Simister


Scale: 1:10

Authorisation:

Date: 9 January, 2020

TEMPORARY WARNING SIGN
'Cycling Hazard'

TM8-14A

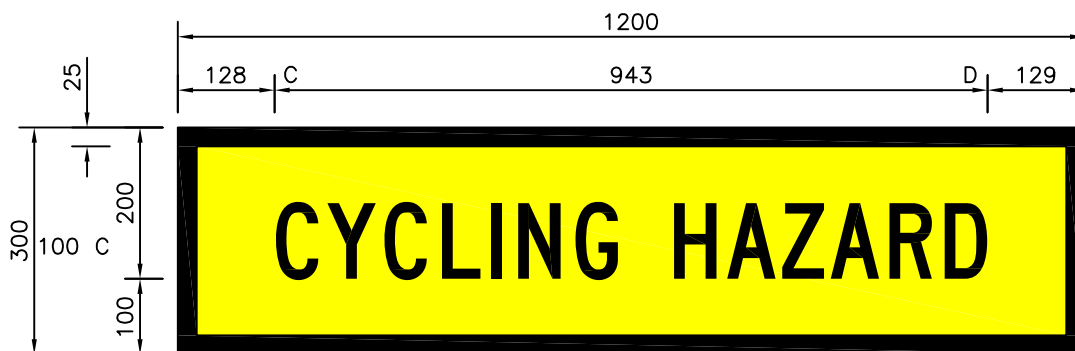

NOTE:

To be used in multi-message sign frames only.



Black

Yellow class 1

Note: Letters & Numerals AS1744:2015.



Government of South Australia
Department of Planning,
Transport and Infrastructure

Road and Marine Services
Traffic Services, Traffic Solutions Unit

Drawn: A. Simister

Scale: 1:10


Authorisation:

A handwritten signature in blue ink.

Date: 9 January, 2020

TEMPORARY WARNING SIGN
'Cycling Hazard'

TM8-14B

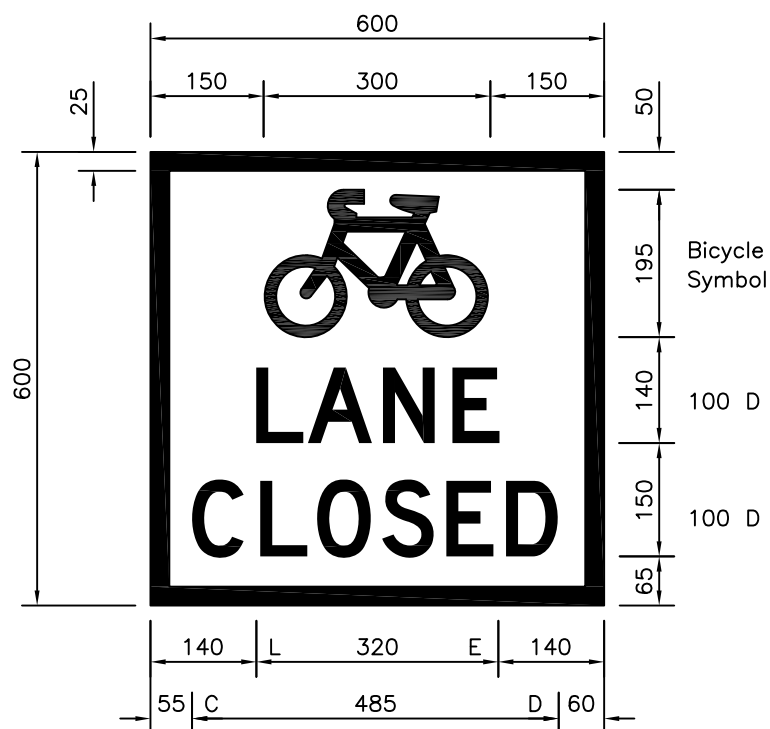

NOTE:
To be used in
multi-message sign frames
only.



Black

White class 1

Note: Letters & Numerals AS1744:2015.



Government of South Australia
Department of Planning,
Transport and Infrastructure

Road and Marine Services
Traffic Services, Traffic Solutions Unit

Drawn: A. Simister


Scale: 1:10

Authorisation:

Date: 9 January, 2020

TEMPORARY WARNING SIGN
'Bicycle Lane Closed'

TM8-16A

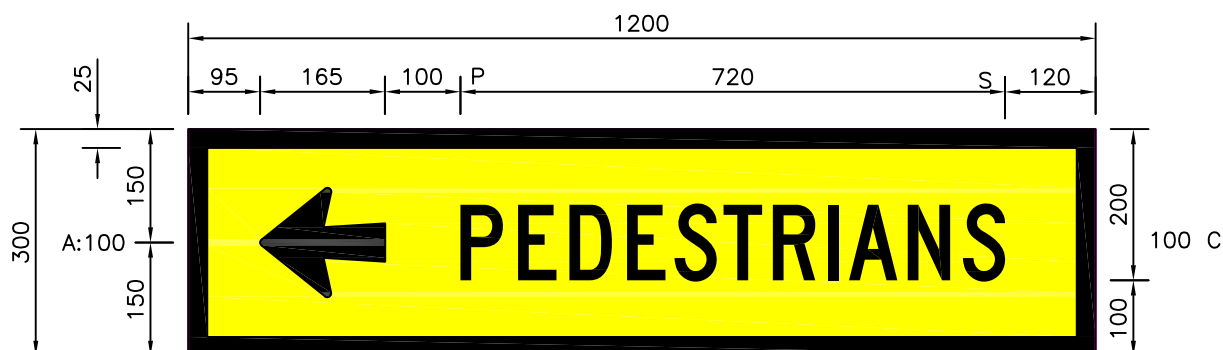

Dimensions apply for left or right construction.

NOTE:

To be used in multi-message sign frames only.

Right Construction



Black

Yellow class 1

Note: Letters & Numerals AS1744:2015.



Government of South Australia

Department of Planning,
Transport and Infrastructure

Road and Marine Services
Traffic Services, Traffic Solutions Unit

Drawn: A. Simister

Scale: 1:10


TEMPORARY WARNING SIGN

'Pedestrians'

Authorisation:

Date: 10 January, 2020

TM8-2B(LorR)

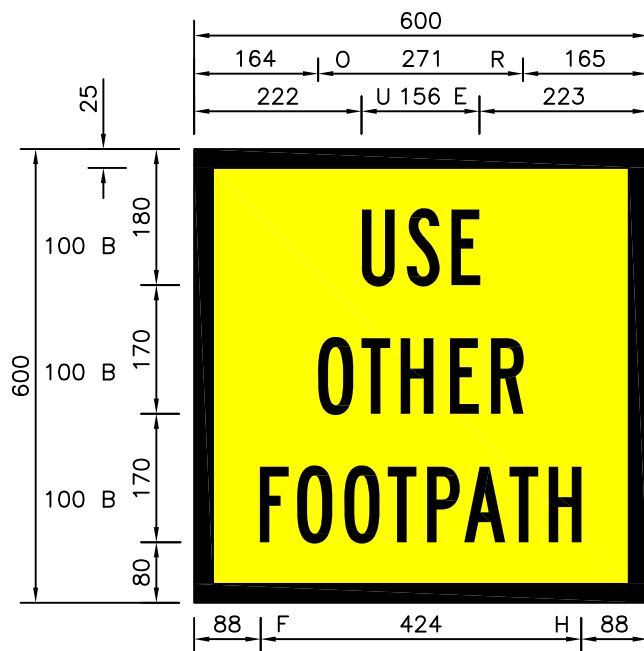

NOTE:

To be used in multi-message sign frames only.



Black

Yellow class 1

Note: Letters & Numerals AS1744:2015.



Government of South Australia

Department of Planning,
Transport and Infrastructure

Road and Marine Services
Traffic Services, Traffic Solutions Unit

Drawn: A. Simister


Scale: 1:10

Authorisation:

Date: 10 January, 2020

TEMPORARY WARNING SIGN
'Use Other Footpath'

TM8-3A

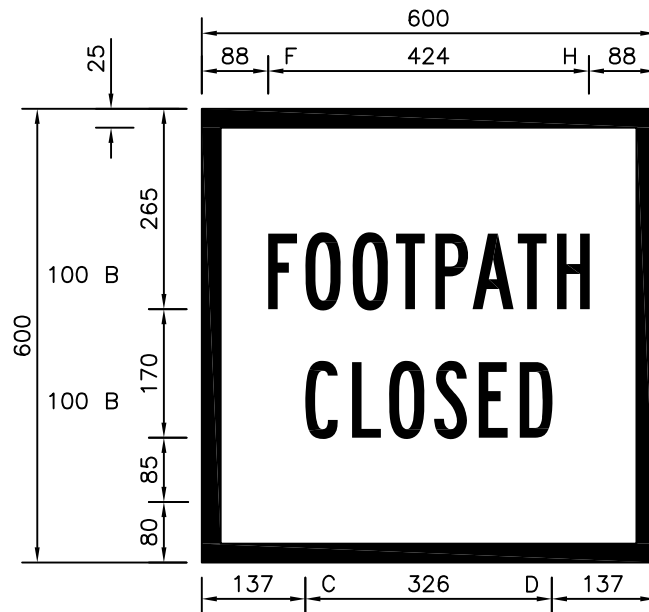

NOTE:

To be used in multi-message sign frames only.



Black

White class 1

Note: Letters & Numerals AS1744:2015.



Government of South Australia
Department of Planning,
Transport and Infrastructure

Road and Marine Services
Traffic Services, Traffic Solutions Unit

Drawn: A. Simister


Scale: 1:10

Authorisation:

Date: 20 December, 2019

TEMPORARY WARNING SIGN
'Footpath closed'

TM8-4A

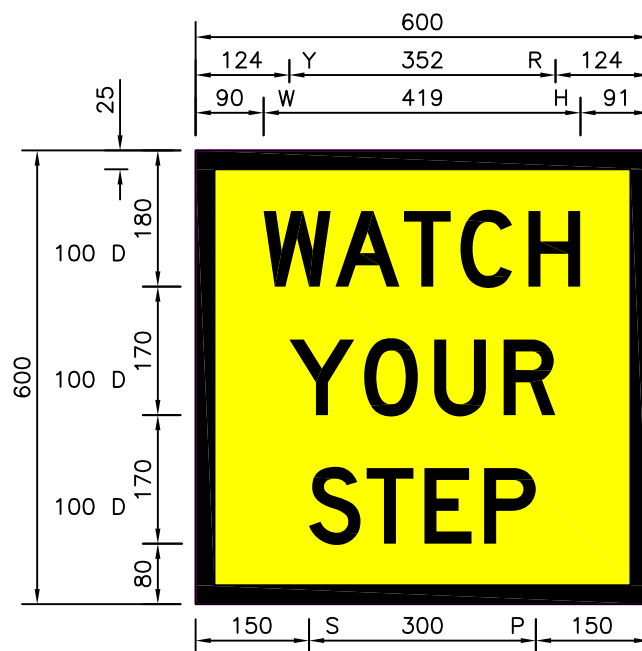

NOTE:

To be used in multi-message sign frames only.



Black

Yellow class 1

Note: Letters & Numerals AS1744:2015.



Government of South Australia

Department of Planning,
Transport and Infrastructure

Road and Marine Services
Traffic Services, Traffic Solutions Unit

Drawn: A. Simister

Scale: 1:10


TEMPORARY WARNING SIGN

'Watch Your Step'

Authorisation:


Date: 10 January, 2020

TM8-7A

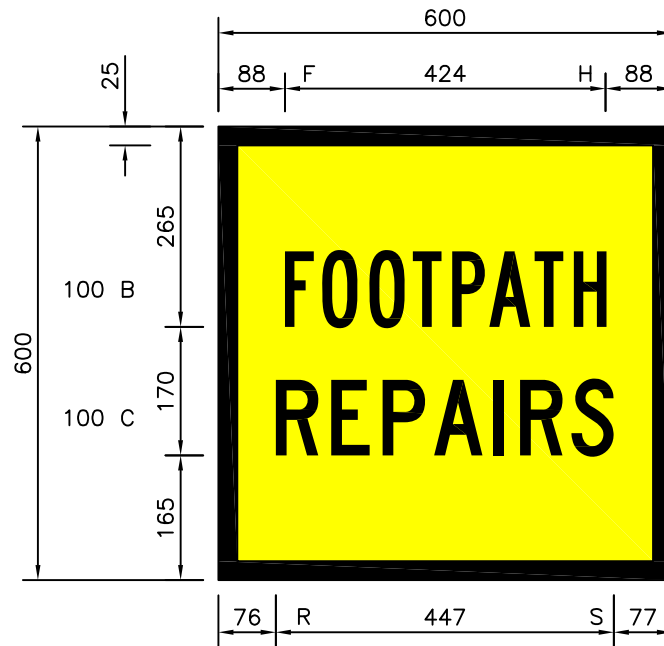

NOTE:

To be used in multi-message sign frames only.

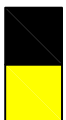

Black

Yellow class 1

Note: Letters & Numerals AS1744:2015.



Government of South Australia
Department of Planning,
Transport and Infrastructure

Road and Marine Services
Traffic Services, Traffic Solutions Unit

Drawn: A. Simister


Scale: 1:10

Authorisation:

Date: 10 January, 2020

TEMPORARY WARNING SIGN
'Footpath Repairs'

TM8-SA102A

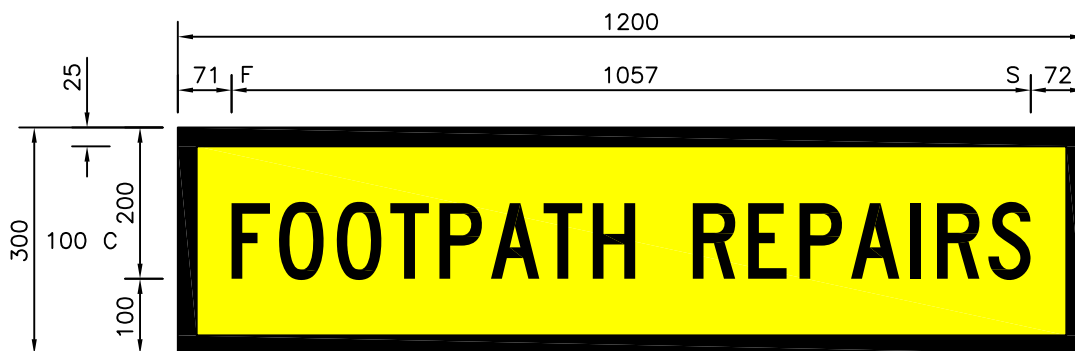

NOTE:

To be used in multi-message sign frames only.



Black

Yellow class 1

Note: Letters & Numerals AS1744:2015.



Government of South Australia
Department of Planning,
Transport and Infrastructure

Road and Marine Services
Traffic Services, Traffic Solutions Unit

Drawn: A. Simister



Scale: 1:10

Authorisation:

Date: 10 January, 2020



TEMPORARY WARNING SIGN
'Footpath Repairs'

TM8-SA102B

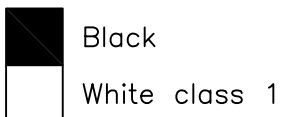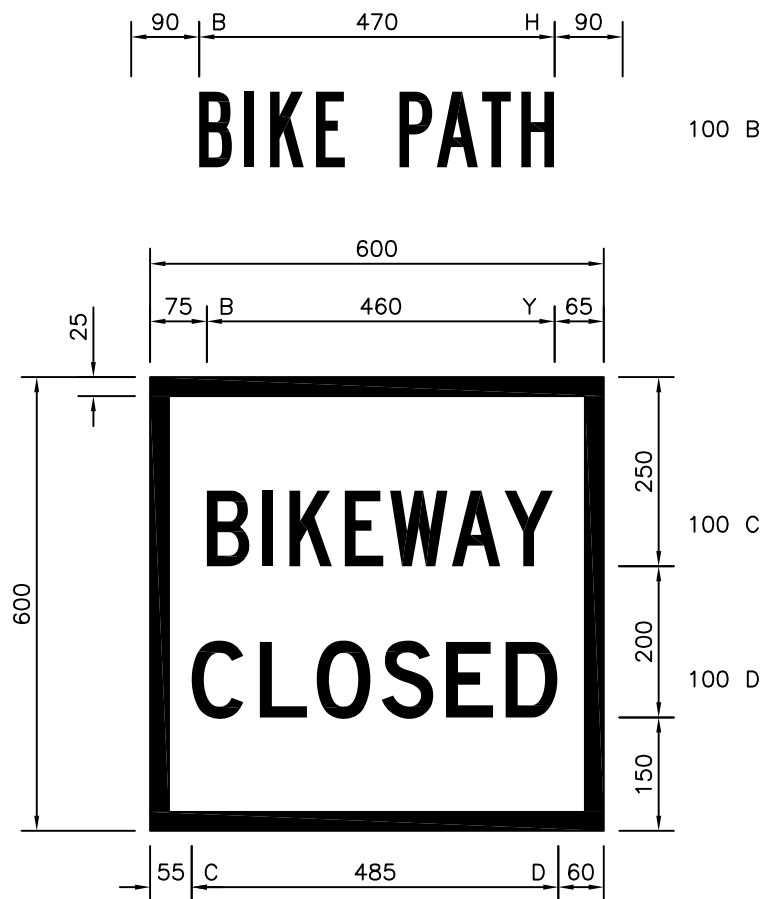

Note: Letters & Numerals AS1744:2015.

 Government of South Australia Department of Planning, Transport and Infrastructure		TEMPORARY WARNING SIGN 'Bikeway / Bike Path Closed'	
Road and Marine Services Traffic Services, Traffic Solutions Unit		Authorisation: 	TM8-SA110A
Drawn: A. Simister	Scale: 1:10	Date:	

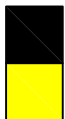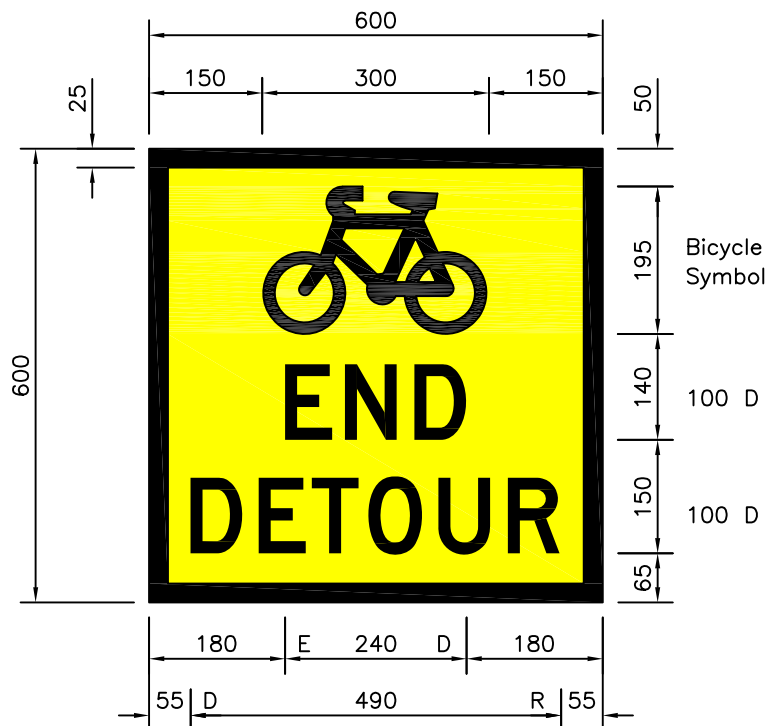

Black

Yellow class 1

Note: Letters & Numerals AS1744:2015.



Government of South Australia

Department of Planning,
Transport and Infrastructure

Road and Marine Services
Traffic Services, Traffic Solutions Unit

Drawn: A. Simister


Scale: 1:10

TEMPORARY WARNING SIGN
'End Bicycle Detour'

Authorisation:

Date: 9 January, 2020

TM8-SA111A

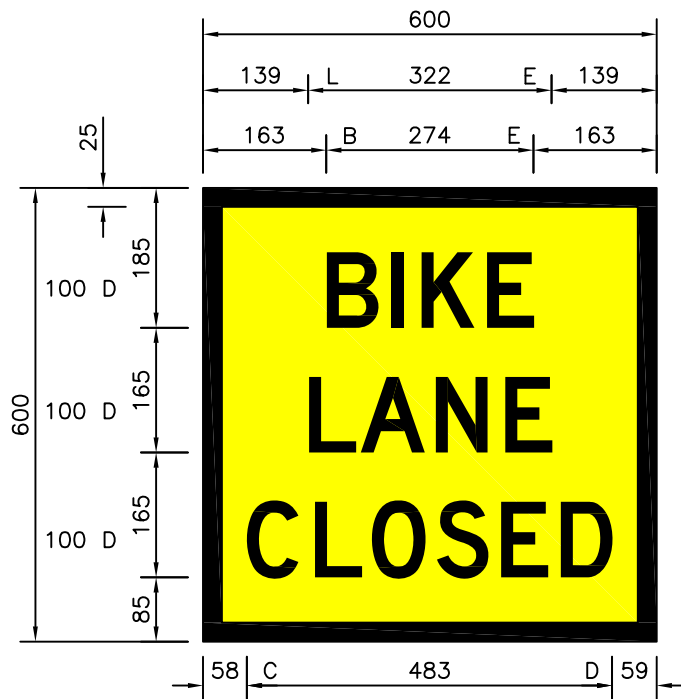

NOTE:

To be used in multi-message sign frames only.



Black

Yellow class 1

Note: Letters & Numerals AS1744:2015.



Government of South Australia
Department of Planning,
Transport and Infrastructure

Road and Marine Services
Traffic Services, Traffic Solutions Unit

Drawn: A. Simister


Scale: 1:10

Authorisation:

Date: 9 January, 2020

TEMPORARY WARNING SIGN
'Bike Lane Closed'

TM8-SA131A

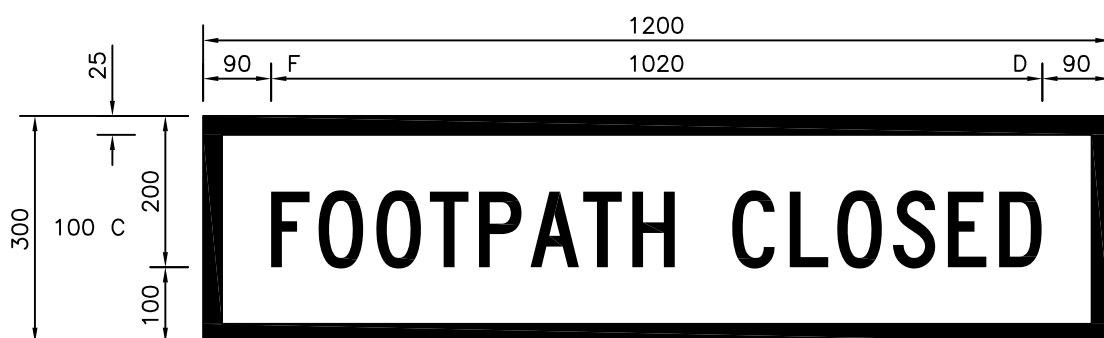

NOTE:

To be used in multi-message sign frames only.



Black

White class 1

Note: Letters & Numerals AS1744:2015.



Government of South Australia
Department of Planning,
Transport and Infrastructure

Road and Marine Services
Traffic Services, Traffic Solutions Unit

Drawn: A. Simister

Scale: 1:10


Authorisation:

A handwritten signature in blue ink.

Date: 20 December, 2019

TEMPORARY WARNING SIGN
'Footpath Closed'

TM8-SA4B

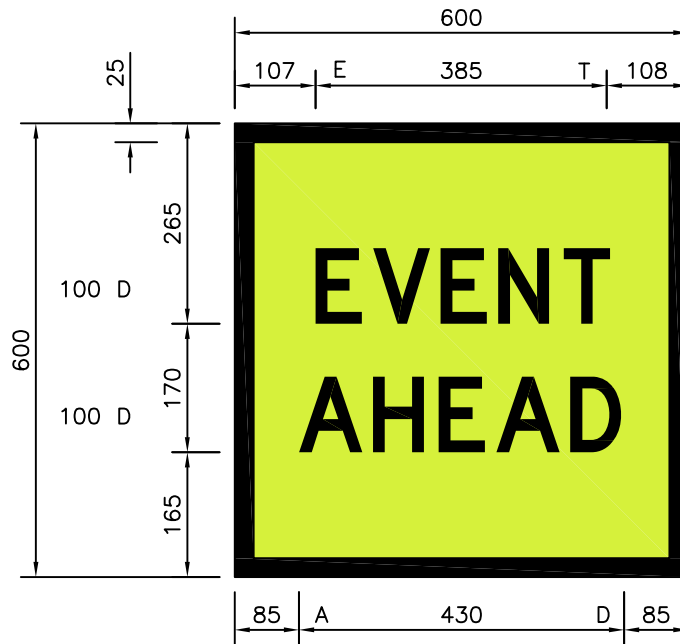

NOTE:

To be used in multi-message sign frames only.



Black

Fluorescent Yellow Green

Note: Letters & Numerals AS1744:2015.



Government of South Australia
Department of Planning,
Transport and Infrastructure

Road and Marine Services
Traffic Services, Traffic Solutions Unit

Drawn: A. Simister


Scale: 1:10

Authorisation:

Date: 9 January, 2020

TEMPORARY WARNING SIGN
'Event Ahead'

TM9-1A

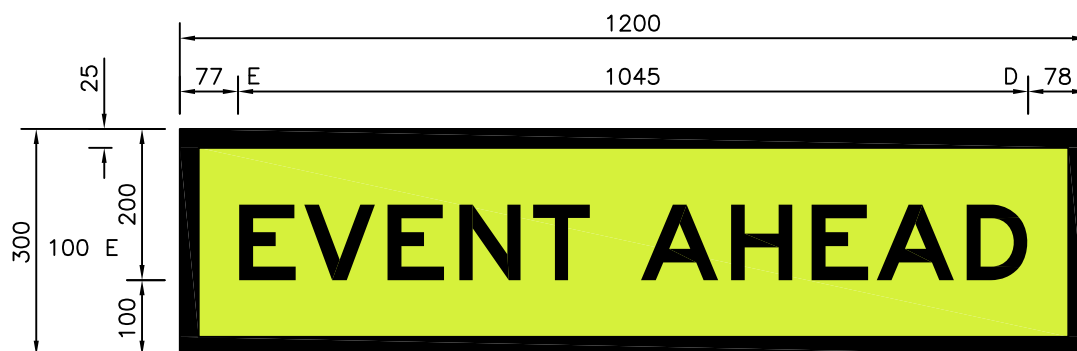

NOTE:

To be used in multi-message sign frames only.



Black

Fluroescent Yellow Green

Note: Letters & Numerals AS1744:2015.



Government of South Australia
Department of Planning,
Transport and Infrastructure

Road and Marine Services
Traffic Services, Traffic Solutions Unit

Drawn: A. Simister

Scale: 1:10


Authorisation:

A handwritten signature in blue ink.

Date: 9 January, 2020

TEMPORARY WARNING SIGN
'Event Ahead'

TM9-1B

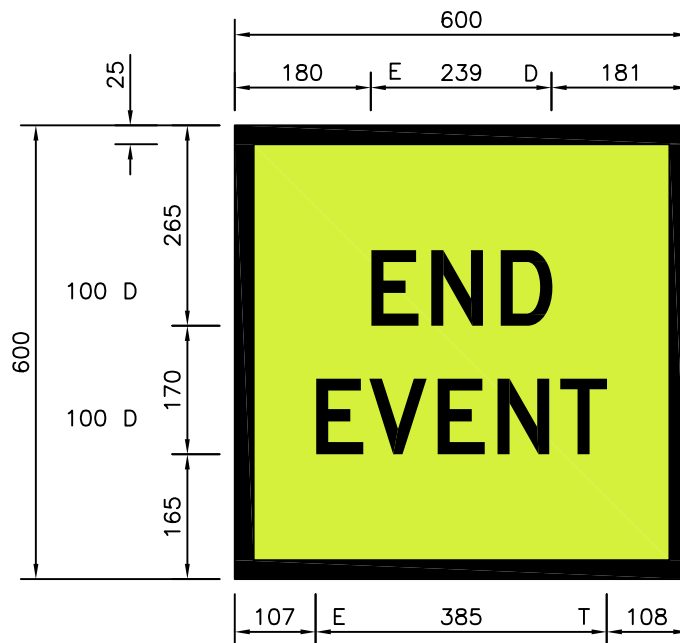

NOTE:
To be used in
multi-message sign frames
only.



Black

Fluorescent Yellow Green

Note: Letters & Numerals AS1744:2015.



Government of South Australia
Department of Planning,
Transport and Infrastructure

Road and Marine Services
Traffic Services, Traffic Solutions Unit

Drawn: A. Simister


Scale: 1:10

Authorisation:

Date: 9 January, 2020

TEMPORARY WARNING SIGN
'End Event'

TM9-2A

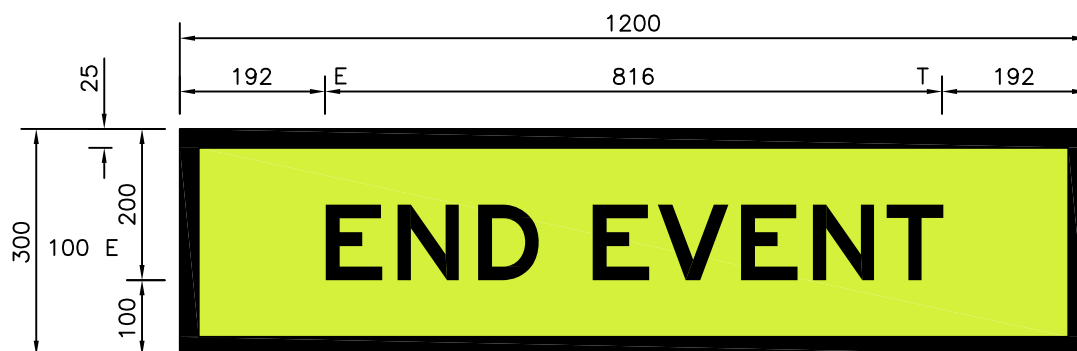

NOTE:

To be used in multi-message sign frames only.



Black

Fluorescent Yellow Green

Note: Letters & Numerals AS1744:2015.



Government of South Australia
Department of Planning,
Transport and Infrastructure

Road and Marine Services
Traffic Services, Traffic Solutions Unit

Drawn: A. Simister


Scale: 1:10

Authorisation:

Date: 9 January, 2020

TEMPORARY WARNING SIGN
'End Event'

TM9-2B

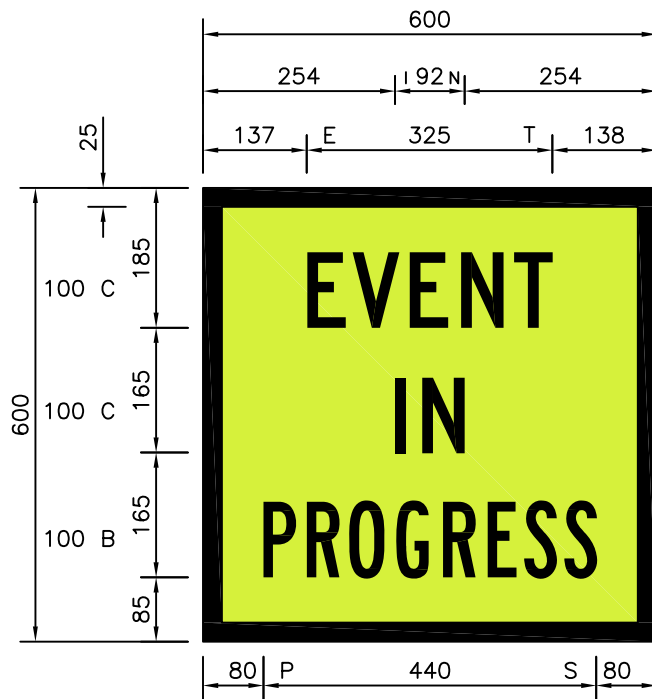

NOTE:

To be used in multi-message sign frames only.



Black

Fluorescent Yellow Green

Note: Letters & Numerals AS1744:2015.

 Government of South Australia Department of Planning, Transport and Infrastructure	TEMPORARY WARNING SIGN 'Event in Progress'	
Road and Marine Services Traffic Services, Traffic Solutions Unit	Authorisation: 	TM9-3A
Drawn: A. Simister	Scale: 1:10	
Date: 9 January, 2020		



NOTE:

To be used in multi-message sign frames only.



Black

Fluroescent Yellow Green

Note: Letters & Numerals AS1744:2015.



Government of South Australia
Department of Planning,
Transport and Infrastructure

Road and Marine Services
Traffic Services, Traffic Solutions Unit

Drawn: A. Simister

Scale: 1:10

Authorisation:

Date: 9 January, 2020

TEMPORARY WARNING SIGN
'Event in Progress'

TM9-3B



NOTE:

To be used in multi-message sign frames only.



Black

Fluorescent Yellow Green

Note: Letters & Numerals AS1744:2015.



Government of South Australia
Department of Planning,
Transport and Infrastructure

Road and Marine Services
Traffic Services, Traffic Solutions Unit

Drawn: A. Simister


Scale: 1:10

Authorisation:

Date: 9 January, 2020

TEMPORARY WARNING SIGN
'Community Event Ahead'

TM9-6C

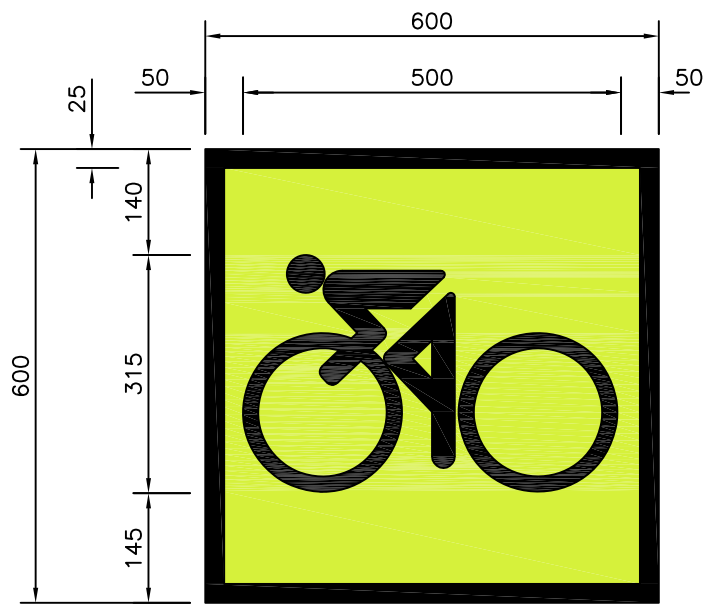

NOTE:

To be used in multi-message sign frames only.




Black

Fluorescent Yellow Green

Note: Letters & Numerals AS1744:2015.

 Government of South Australia Department of Planning, Transport and Infrastructure	TEMPORARY WARNING SIGN 'Event Bike'	
Road and Marine Services Traffic Services, Traffic Solutions Unit	Authorisation: 	TM9-7A
Drawn: A. Simister	Scale: 1:10	
Date: 9 January, 2020		

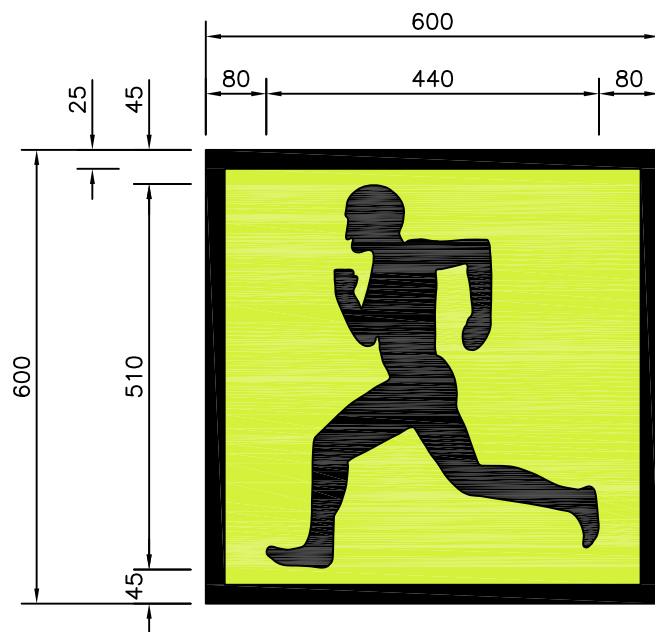

NOTE:

To be used in multi-message sign frames only.



Black

Fluorescent Yellow Green

Note: Letters & Numerals AS1744:2015.



Government of South Australia
Department of Planning,
Transport and Infrastructure

Road and Marine Services
Traffic Services, Traffic Solutions Unit

Drawn: A. Simister


Scale: 1:10

Authorisation:

Date: 9 January, 2020

TEMPORARY WARNING SIGN
'Event Runner'

TM9-8A

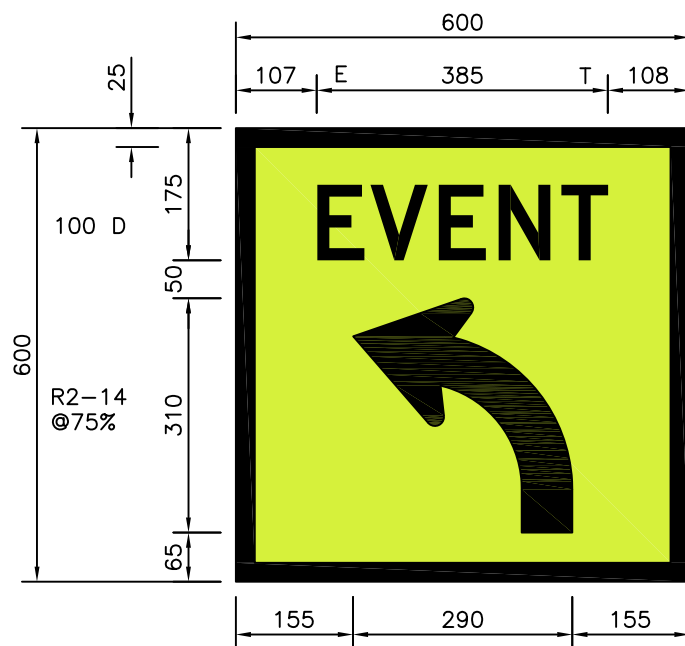

Right Construction



Black

Fluorescent Yellow Green

Note: Letters & Numerals AS1744:2015.



Government of South Australia
Department of Planning,
Transport and Infrastructure

Road and Marine Services
Traffic Services, Traffic Solutions Unit

Drawn: A. Simister


Scale: 1:10

Authorisation:

Date: 9 January, 2020


TEMPORARY WARNING SIGN
'Event Turn Left/Right'

TM9-SA107A

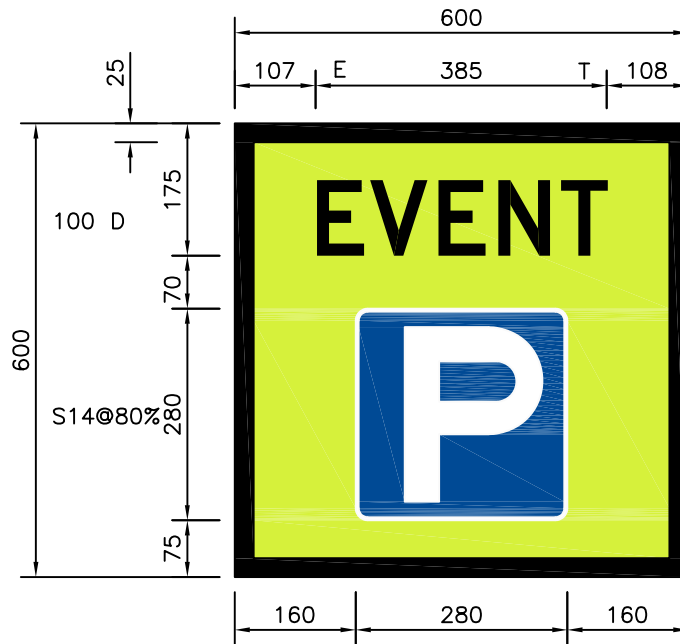


NOTE:

To be used in multi-message sign frames only.

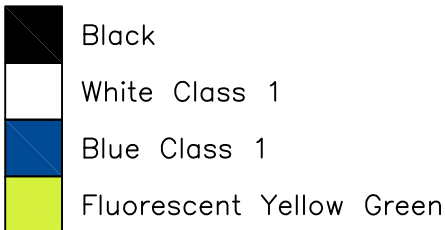

Note: Letters & Numerals AS1744:2015.

 Government of South Australia Department of Planning, Transport and Infrastructure	TEMPORARY WARNING SIGN 'Event Parking'	
Road and Marine Services Traffic Services, Traffic Solutions Unit	Authorisation:  Date: 9 January, 2020	TM9-SA108A
Drawn: A. Simister	Scale: 1:10	

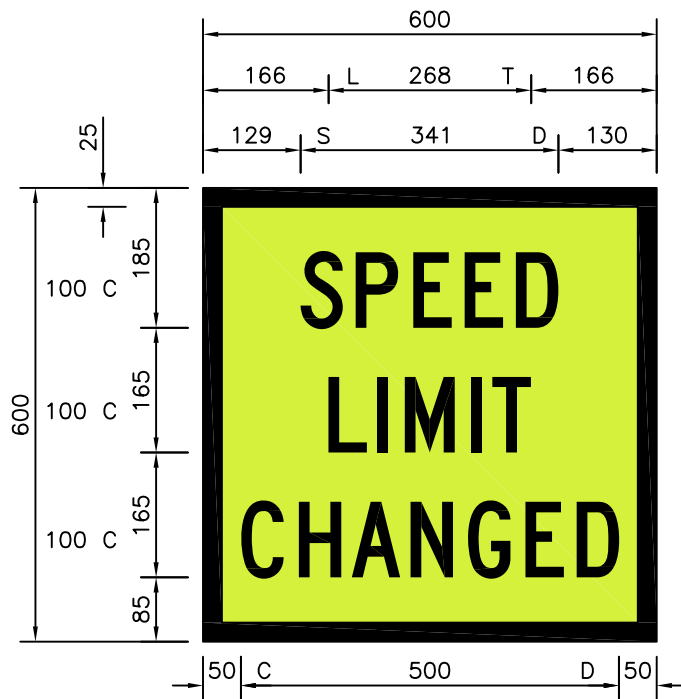

NOTE:

To be used in
multi-message sign frames
only.



Black

Fluorescent Yellow Green

Note: Letters & Numerals AS1744:2015.



Government of South Australia
Department of Planning,
Transport and Infrastructure

Road and Marine Services
Traffic Services, Traffic Solutions Unit

Drawn: A. Simister


Scale: 1:10

Authorisation:

Date: 9 January, 2020

TEMPORARY WARNING SIGN
'Speed Limit Changed'

TM9-SA109A

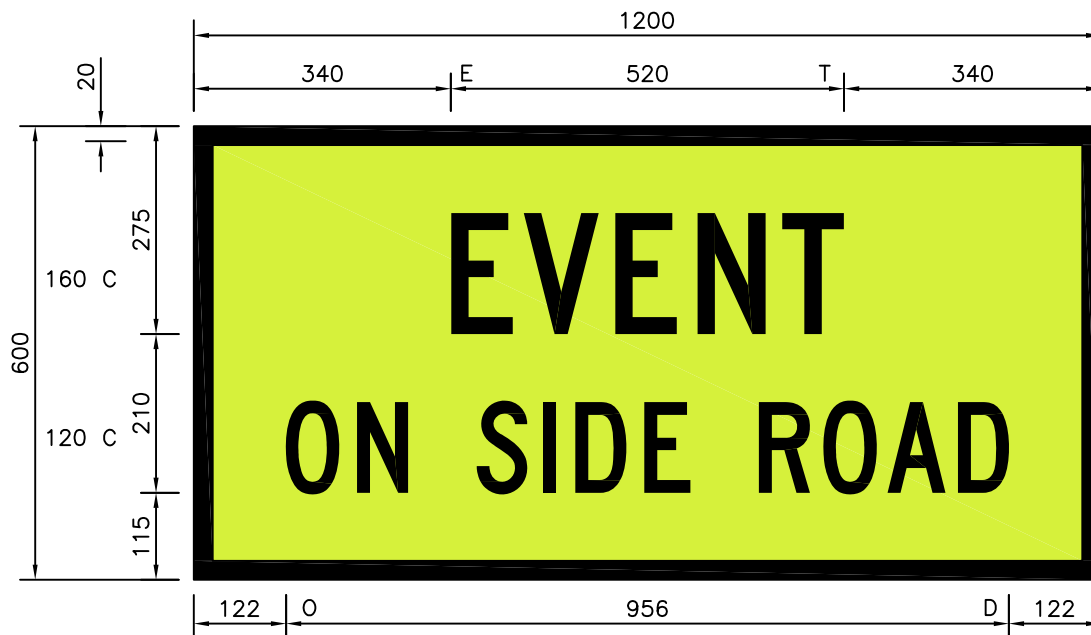

NOTE:

To be used in multi-message sign frames only.



Black

Fluorescent Yellow Green

Note: Letters & Numerals AS1744:2015.



Government of South Australia
Department of Planning,
Transport and Infrastructure

Road and Marine Services
Traffic Services, Traffic Solutions Unit

Drawn: A. Simister


Scale: 1:10

Authorisation:

Date: 9 January, 2020

TEMPORARY WARNING SIGN
'Event On Side Road'

TM9-SA125C

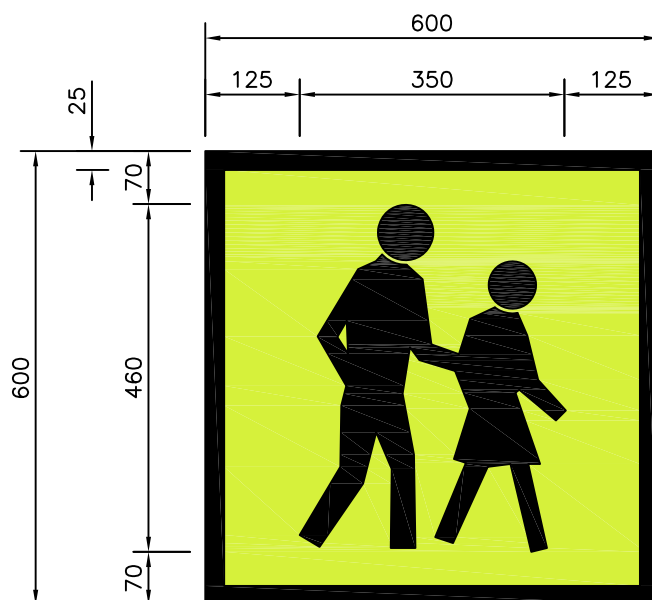

NOTE:

To be used in multi-message sign frames only.



Black

Fluorescent Yellow Green

Note: Letters & Numerals AS1744:2015.



Government of South Australia
Department of Planning,
Transport and Infrastructure

Road and Marine Services
Traffic Services, Traffic Solutions Unit

Drawn: A. Simister


Scale: 1:10

Authorisation:

Date: 9 January, 2020

TEMPORARY WARNING SIGN
'Event Pedestrian'

TM9-SA126A

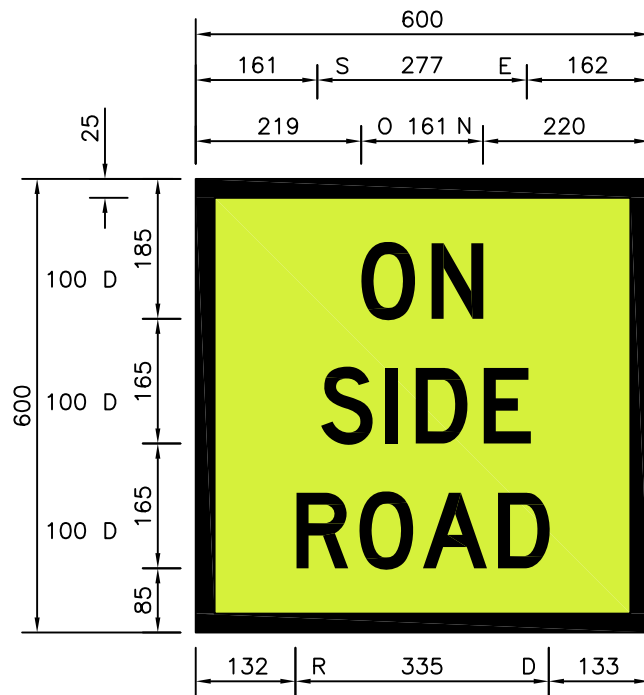

NOTE:

To be used in multi-message sign frames only.



Black

Fluorescent Yellow Green

Note: Letters & Numerals AS1744:2015.



Government of South Australia
Department of Planning,
Transport and Infrastructure

Road and Marine Services
Traffic Services, Traffic Solutions Unit

Drawn: A. Simister


Scale: 1:10

Authorisation:

Date: 9 January, 2020

TEMPORARY WARNING SIGN
'On Side Road'

TM9-SA25A

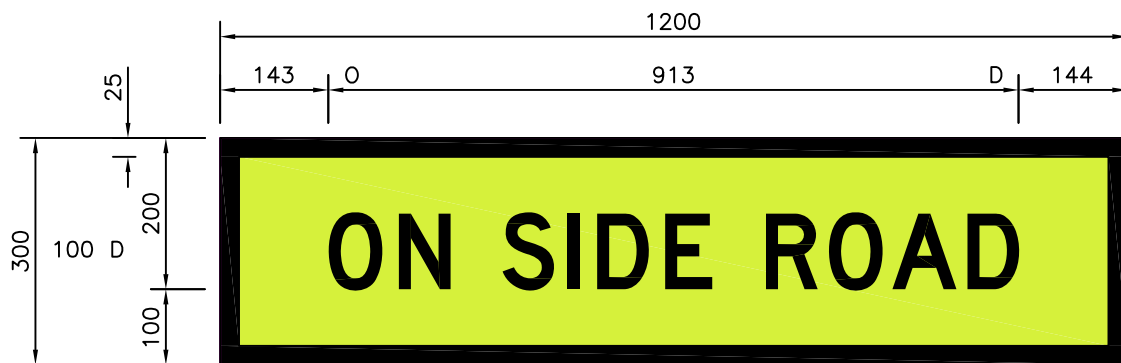

NOTE:

To be used in multi-message sign frames only.



Black



Fluorescent Yellow Green

Note: Letters & Numerals AS1744:2015.



Government of South Australia
Department of Planning,
Transport and Infrastructure

Road and Marine Services
Traffic Services, Traffic Solutions Unit

Drawn: A. Simister


Scale: 1:10

Authorisation:

Date: 9 January, 2020

TEMPORARY WARNING SIGN
'On Side Road'

TM9-SA25B

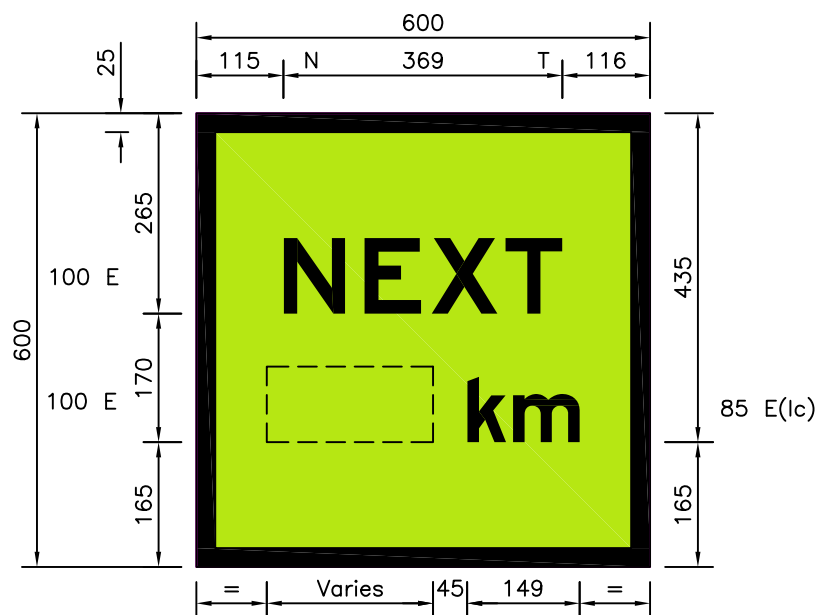

NOTE:

To be used in multi-message sign frames only.



Black

Fluorescent Yellow Green

Note: Letters & Numerals AS1744:2015.



Government of South Australia

Department of Planning,
Transport and Infrastructure

Road and Marine Services
Traffic Services, Traffic Solutions Unit

Drawn: A. Simister

Scale: 1:10


Authorisation:

Date: 9 January, 2020

TEMPORARY WARNING SIGN

'Next xx km'

TM9-SA28A

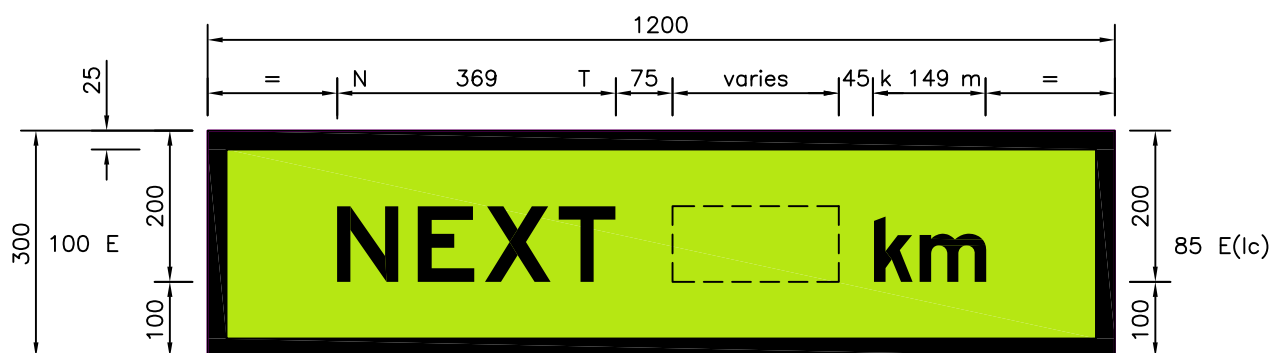

NOTE:

To be used in multi-message sign frames only.



Black

Fluorescent Yellow Green

Note: Letters & Numerals AS1744:2015.



Government of South Australia

Department of Planning,
Transport and Infrastructure

Road and Marine Services
Traffic Services, Traffic Solutions Unit

Drawn: A. Simister

Scale: 1:10

TEMPORARY WARNING SIGN

'Next xx km'

Authorisation:

Date: 9 January, 2020

TM9-SA28B