




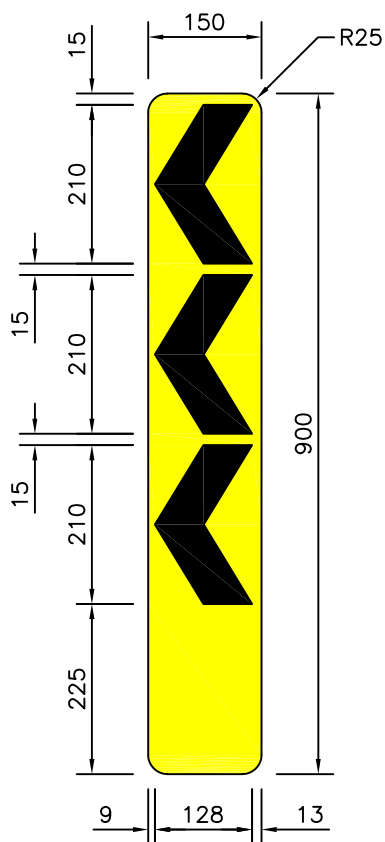

Left Construction

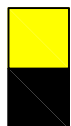

Right Construction

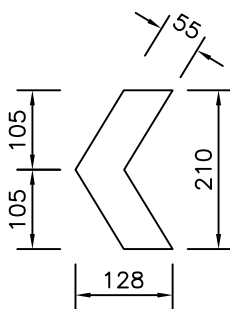

Yellow (retroreflective)

Black

Note: Letters & Numerals AS1744:2015.



Government of South Australia
Department of Planning,
Transport and Infrastructure

Road and Marine Services
Network Management Services, Traffic Solutions Unit

Drawn: A. Simister

Scale: 1:10

Authorisation:

Date: 12 May, 2020

TEMPORARY WARNING SIGN
'Vertical Chevron Marker'

T4-SA101(LorR)