


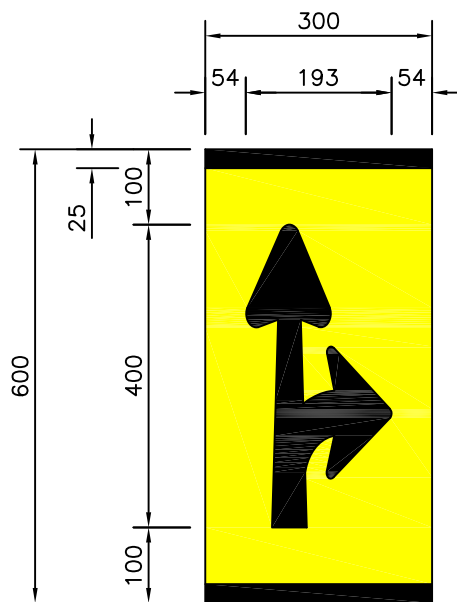

NOTES:

To be used in multi-message sign frames only.

Lane Status panels are to only be used in multi-message signs and not individually. Panels shall be placed in the top position of the frame on the side closest to the traffic.

Combinations should meet all other conditions of AS1742.3:2019, Section 4.2.2 "Multi-message signs".



Black

Yellow class 400

Note: Letters & Numerals AS1744:2015.



Government of South Australia
Department for Infrastructure
and Transport

Road and Marine Services
Network Management Services, Traffic Solutions Unit

Drawn: M. Douglas

Scale: 1:10

Authorisation:

Date: 26 May, 2022

TEMPORARY WARNING SIGN
'Lane Status – Through and Right'

TM10-SA121A