
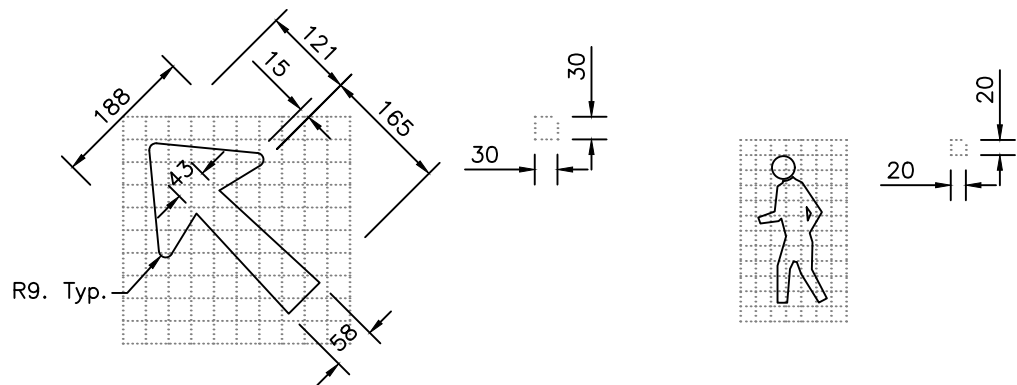


SIGN SIZE, mm

G9-SA141A(Illust.)
450x600

G9-SA141B
600x800

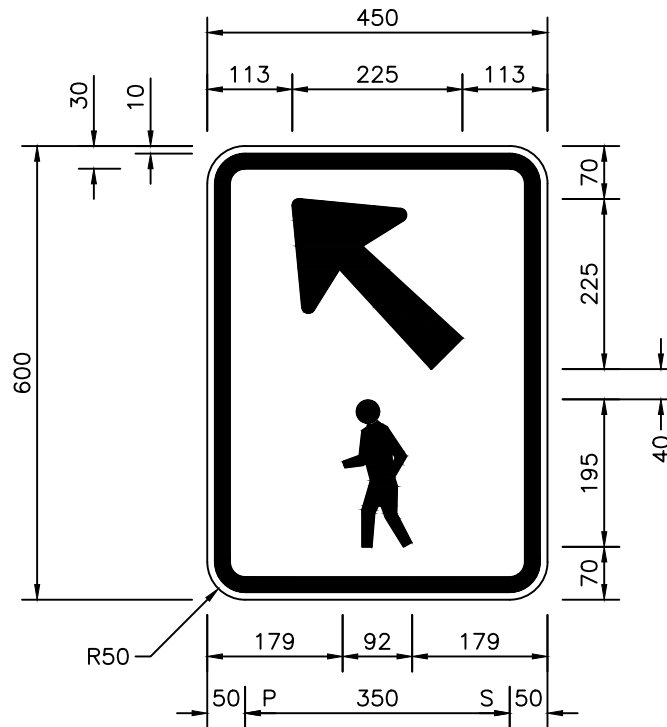

Black

White class 400

Note: Letters & Numerals AS1744:2015.



Government of South Australia
Department for Infrastructure and Transport

Road and Marine Services
Network Management Services, Traffic Solutions Unit

Drawn: M. Douglas

Scale: 1:10

Authorisation:

Date: 14 March, 2023

GUIDE SIGN
'All Pedestrians'

G9-SA141
(LorR)