


SIGN SIZE, mm
W8-SA114A(illustr.) 600x520
W8-SA114B 750x650
W8-SA114C 900x780

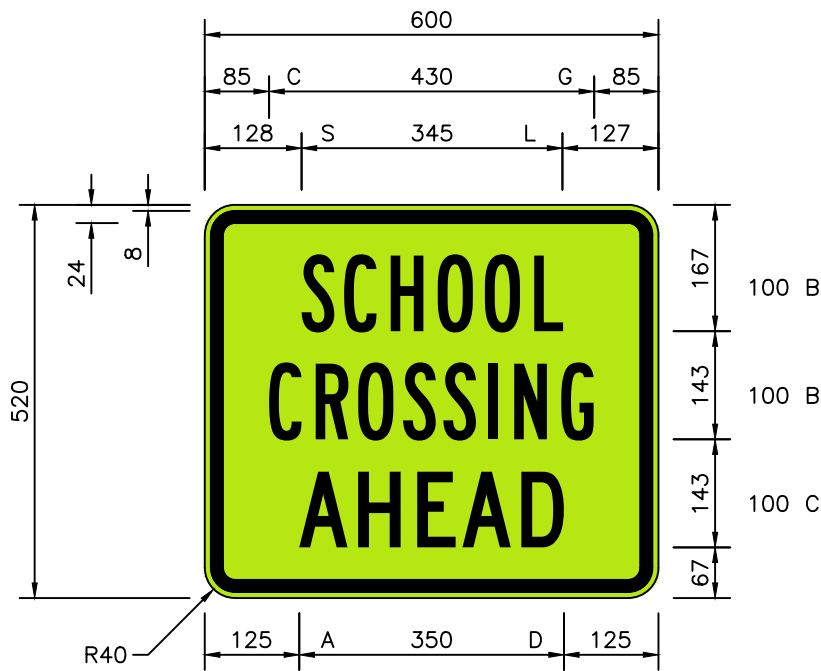

NOTE:

The sign may replace the W8-22 "Crossing ahead" sign in the W6-3/W8-22 assembly at koala crossings.

Approval required for use – refer to Manager, Traffic Services Section of DIT.

Black

Fluorescent Yellow Green (retroreflective)

Note: Letters & Numerals AS1744:2015.

 Government of South Australia Department for Infrastructure and Transport		Warning 'School Crossing Ahead'	
Road and Marine Services Network Management Services, Traffic Solutions Unit		Authorisation: 	W8-SA114
Drawn: M. Douglas	Scale: 1: 10	Date: 2 February, 2024	