
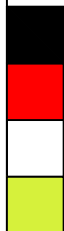


SIGN SIZE, mm
R3-SA57A(Illust.) 650x1400
R3-SA57B 800x1800

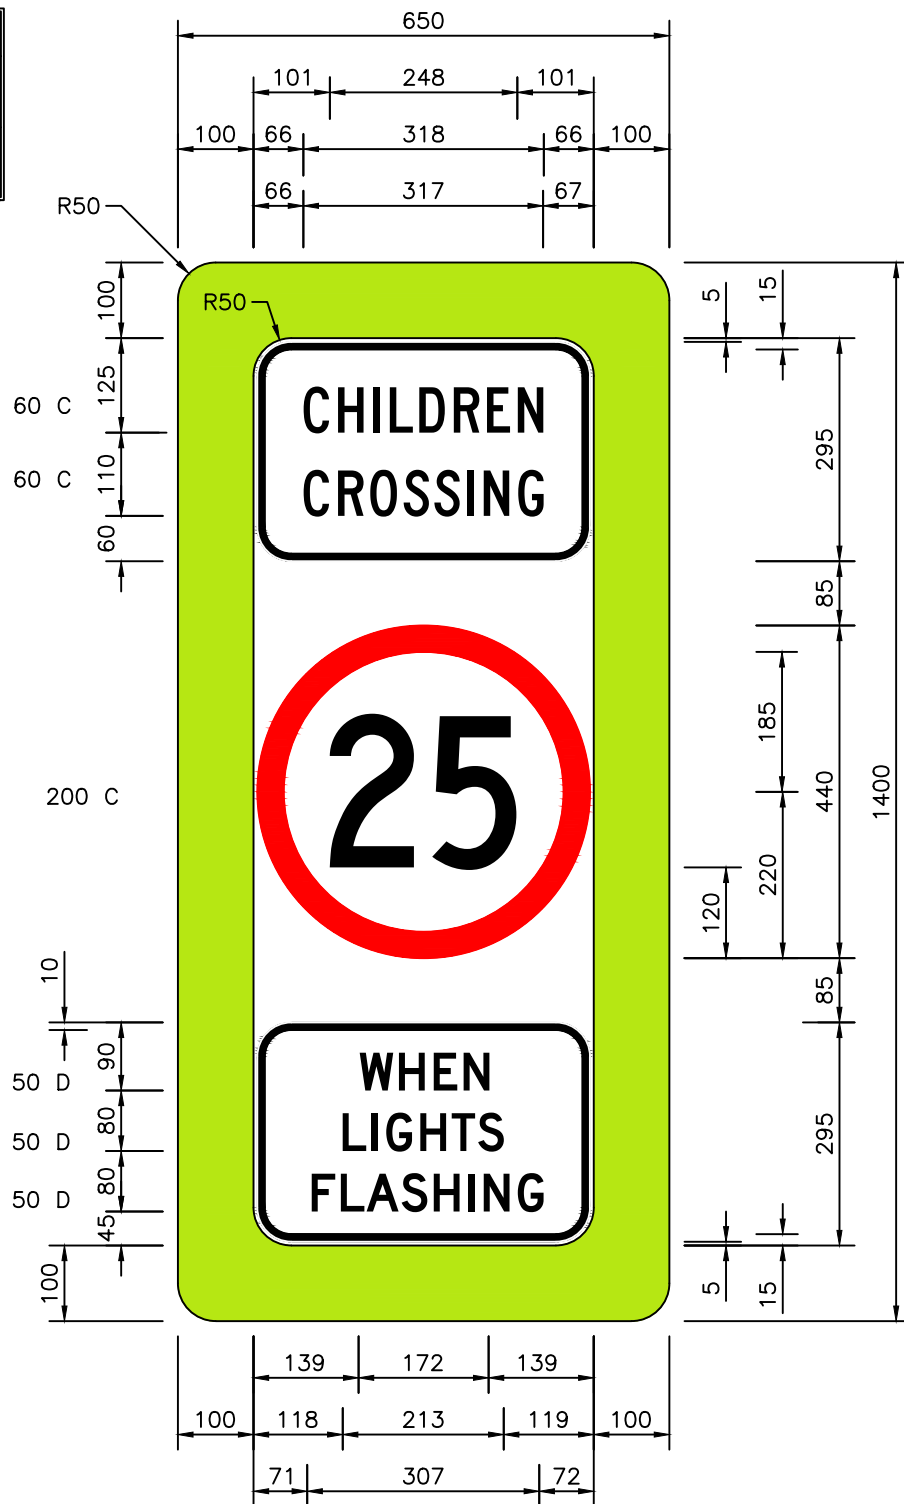

Black

Red (retro-reflective) Class 400

Formerly R4-SA56

White (retro-reflective) Class 400

Fluorescent Yellow Green (retroreflective)

Note: Letters & Numerals AS1744:2015.



Government of South Australia
Department for Infrastructure and Transport

Road and Marine Services
Network Management Services, Traffic Solutions Unit

Drawn: M. Douglas

Scale: 1: 10

Authorisation:

Date: 20 June, 2024

REGULATORY SIGN

"Koala" Pedestrian Crossing FYG Backing

R3-SA57