

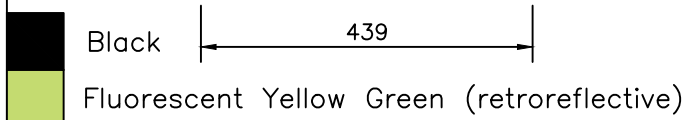
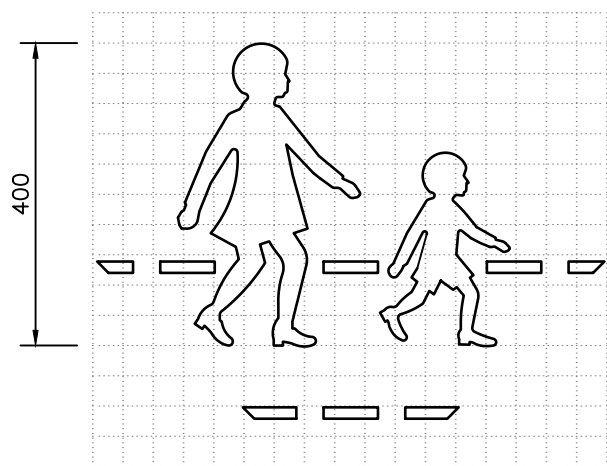


SIGN SIZE, mm
W6-5-2A 600 X 600
W6-5-2B (Illust.) 750 X 750
W6-5-2C 900 X 900

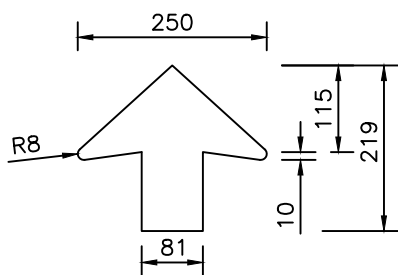

Note: Letters & Numerals AS1744:2015.

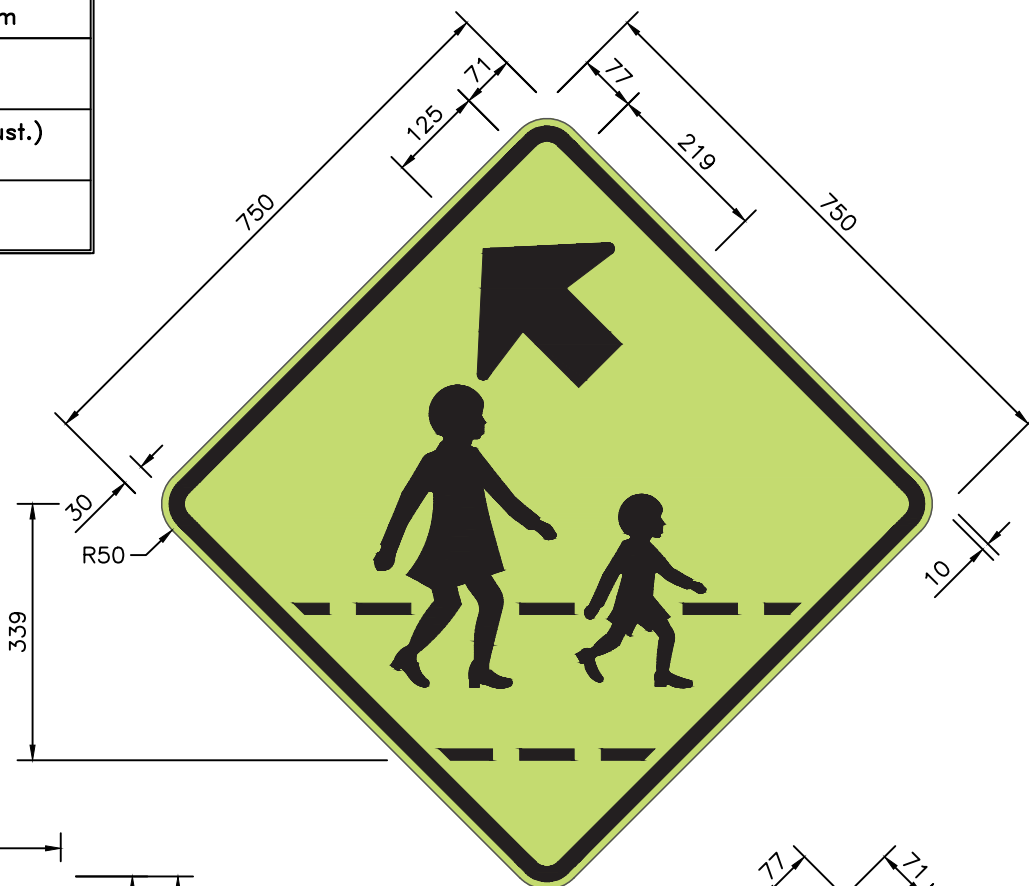

Government of South Australia
Department for Infrastructure
and Transport

Road and Marine Services
Network Management Services, Traffic Solutions Unit

Drawn: M. Douglas

Scale: 1: 10

Authorisation:

Date: 8 August, 2025

WARNING

'Children's Crossing Ahead 45 Deg'

W6-5-2
Left or Right