


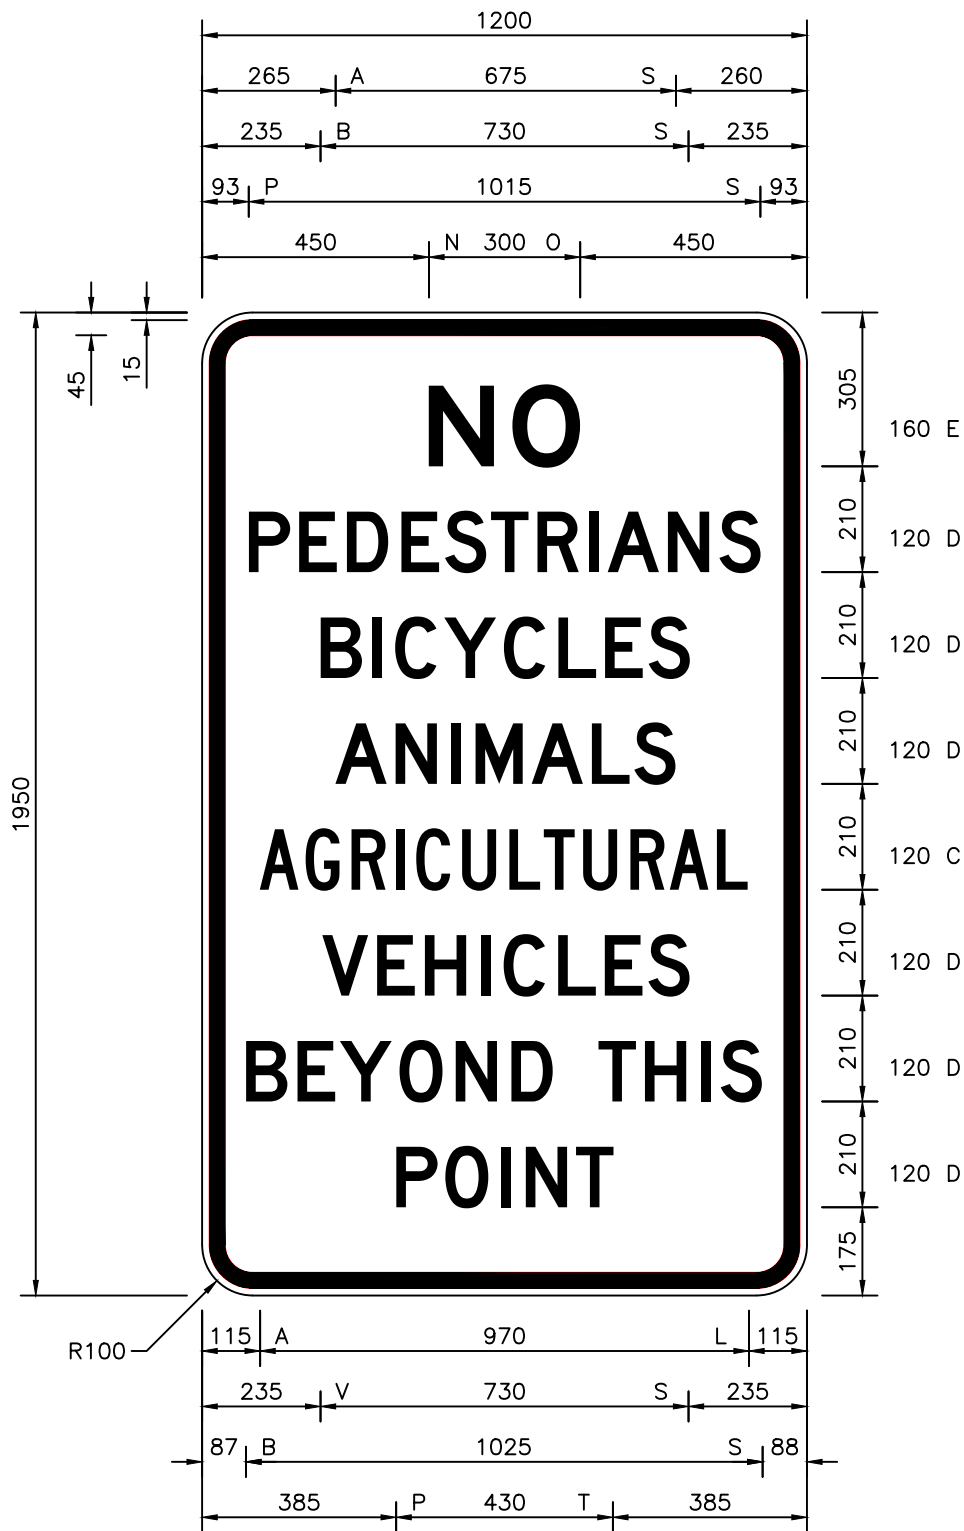

Also refer to R6-SA101 (Approval required for use Refer to Manager, Traffic Services Section, DTI) (ARR-97,229)

Black

White (retro-reflective) Class 400

Note: Letters & Numerals AS1744:2015.



Government of South Australia
Department for Infrastructure
and Transport

Road and Marine Services
Network Management Services, Traffic Solutions Unit

Drawn: M. Douglas

Scale: 1: 15

REGULATORY SIGN

'No Pedestrians Bicycles Animals Agricultural Vehicles Beyond This Point'

Authorisation:

Date: 5 August, 2026

R6-SA13