
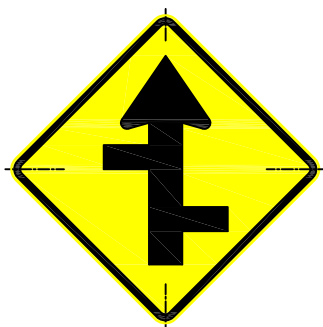



SIGN SIZE, mm
W2-8A 600x600
W2-8B(Illust.) 750x750
W2-8C 900x900
W2-8D 1200x1200

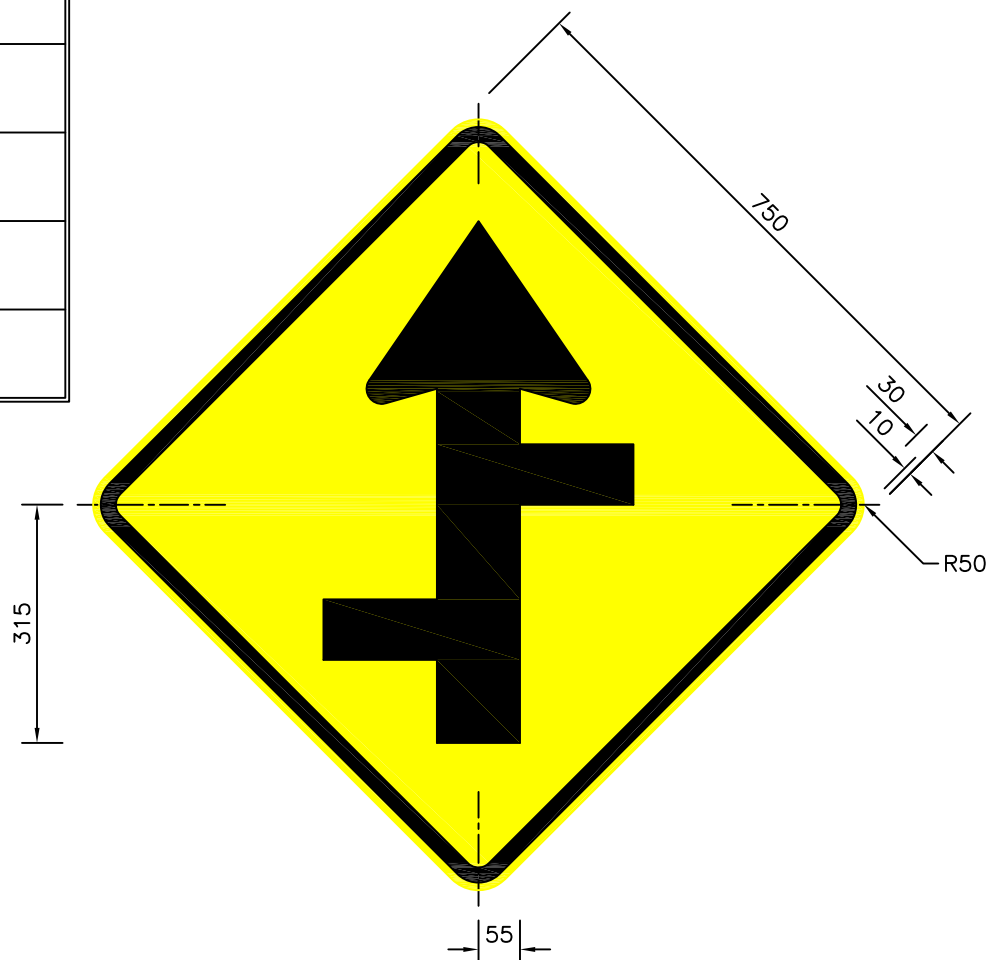

W2-8(R)

Yellow (retro-reflective)

Black

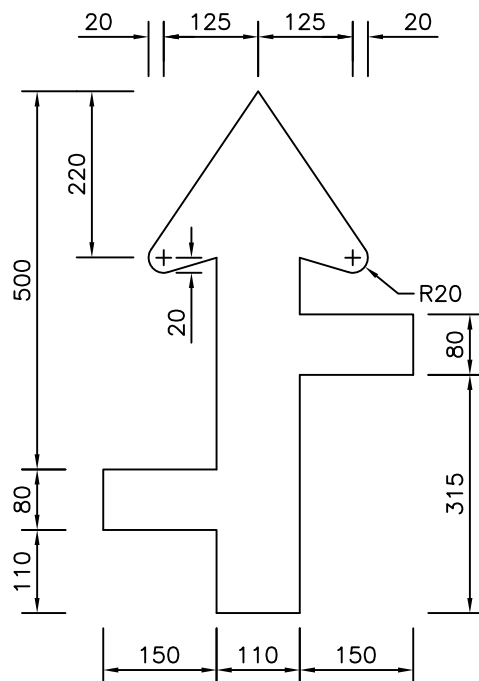

Note: Letters & Numerals AS1744.



Government of South Australia
Department of Planning,
Transport and Infrastructure

Traffic & Access Standards Section
Traffic Regulation & Standards

Drawn: A. Simister

Scale: 1:10

Authorisation:

A3Clark

Date: 7 December, 2012

WARNING SIGN
'Staggered Side Road Intersection, Straight'

W2-8(LorR)