
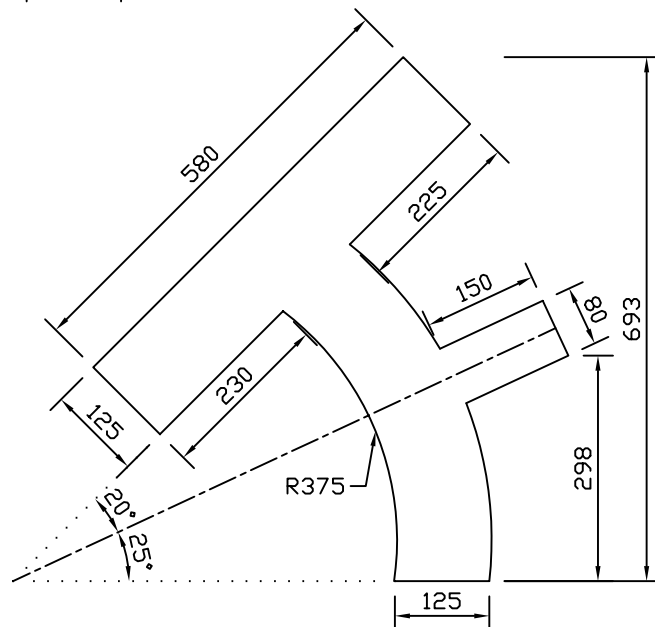


SIGN SIZE, mm

W1-SA65B (Illust.)  
750x750

W1-SA65C  
900x900

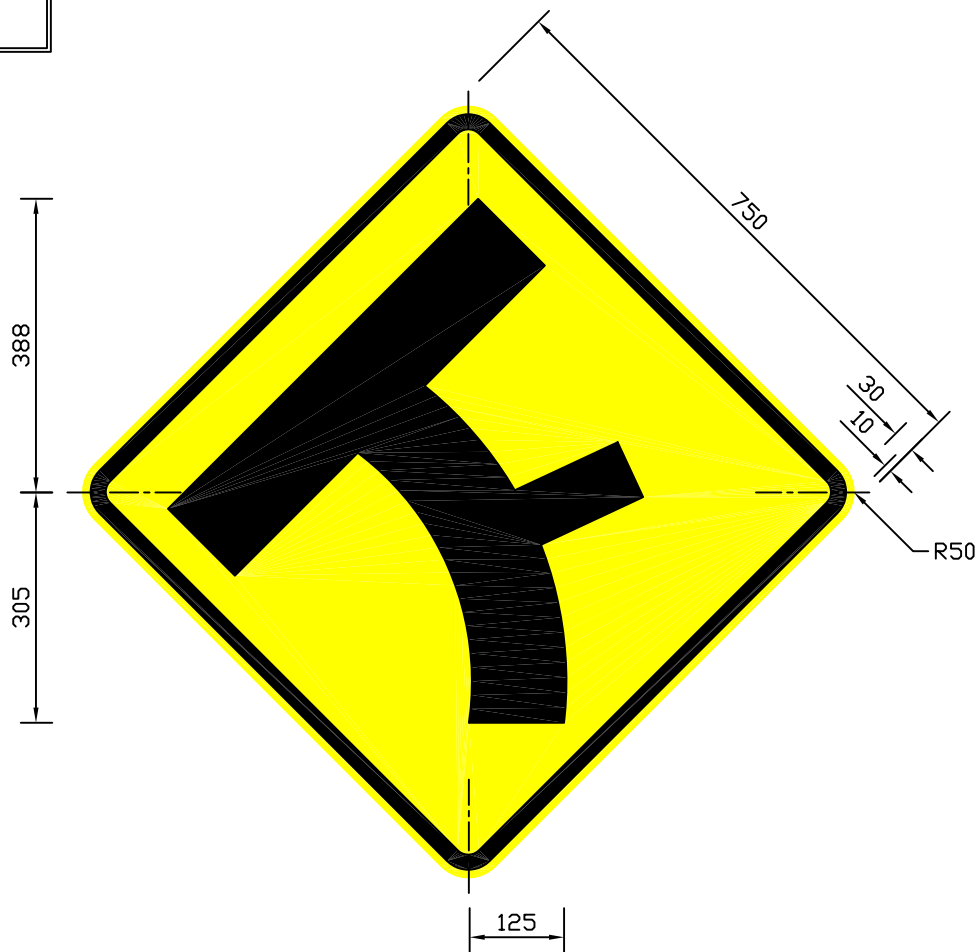

Yellow (retro-reflective)

Black

Note: Letters & Numerals AS1744.

**TRANSPORT SA**

WARNING SIGN

'T Junction on Bend with side Road on Outside of Curve (LorR)'

Statewide Operational Coordination Group  
Traffic Management Unit

Authorisation:

*A3 Clark*

Date: 23 August, 2001

**W2-SA65**  
**(LorR)**

Drawn: A. Watt

Scale: 1:10