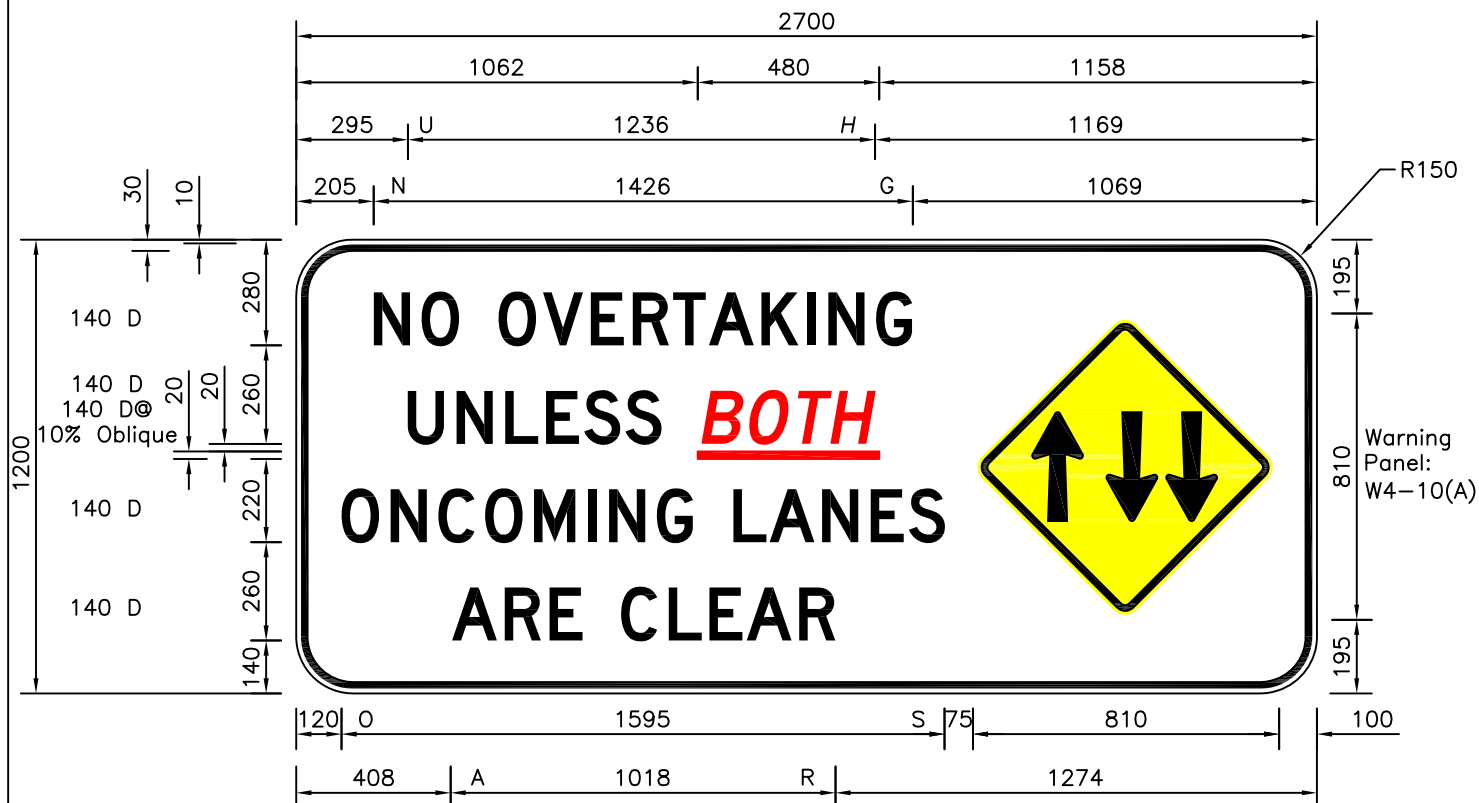


Note: Letters & Numerals AS1744:2015.

 Government of South Australia Department of Planning, Transport and Infrastructure	WARNING SIGN 'No Overtaking Unless Both Oncoming Lanes are Clear'		
Technical Services Safety and Service Division	Authorisation: 	W4-SA52	
	Drawn: A. Simister		

Scale: 1:20

Date: 22 April, 2015