


|                               |
|-------------------------------|
| SIGN SIZE, mm                 |
| W4-SA101B(Illust.)<br>750x750 |
| W4-SA101C<br>900x900          |
| W4-SA101D<br>1200x1200        |

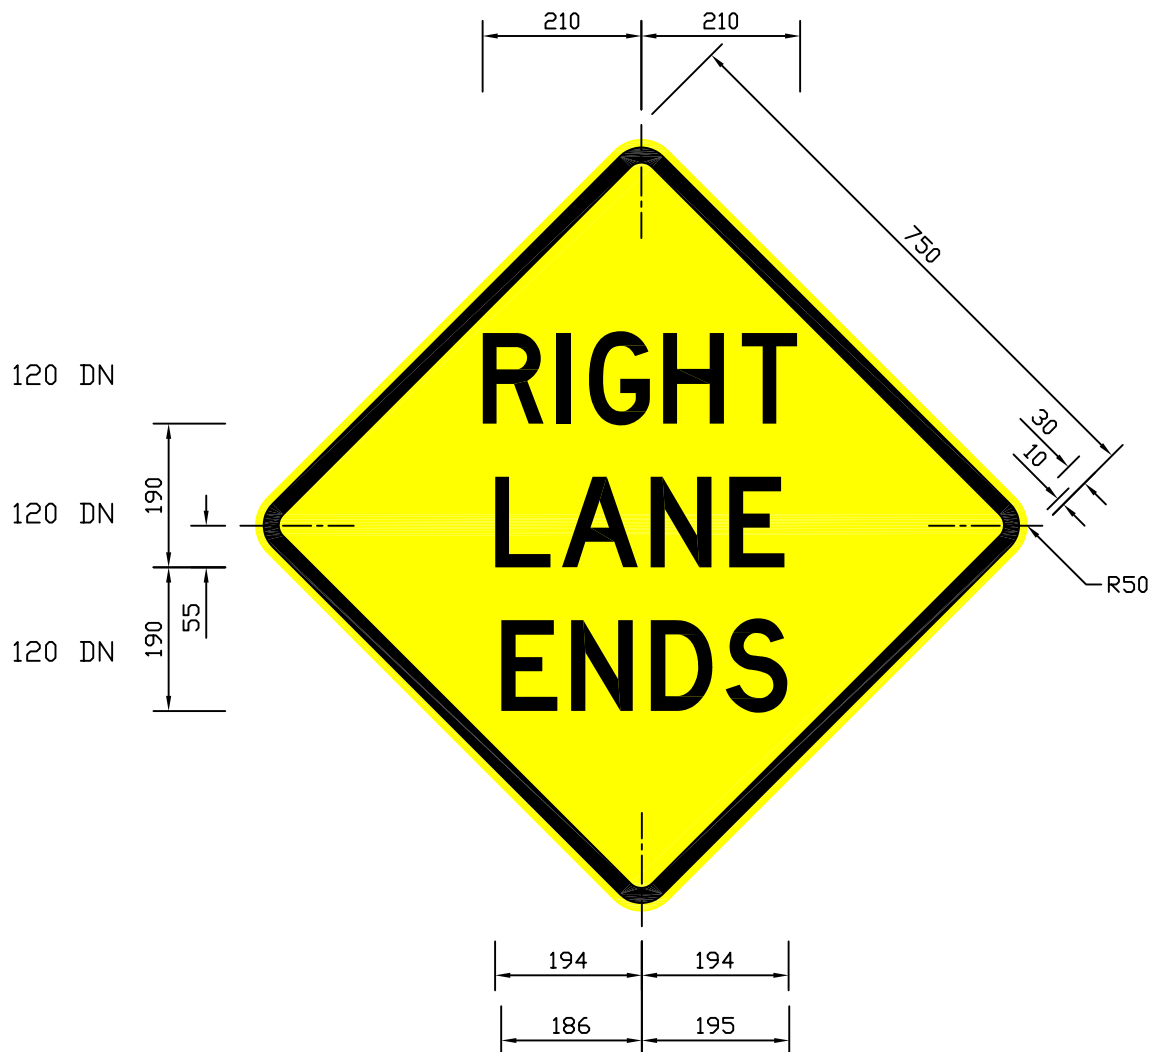

 Yellow (retro-reflective)

 Black

Note: Letters & Numerals AS1744.

 **TRANSPORT SA**

WARNING SIGN  
'Right Lane Ends'

Statewide Operational Coordination Group  
Traffic Management Unit

Authorisation:

*A. B. Clark*

Date: 29 April, 2002

Drawn: G.Roberts

Scale: 1:10

**W4-SA101**