


| SIGN SIZE, mm                 |
|-------------------------------|
| W8-SA101B(Illust.)<br>750x500 |
| W8-SA101C<br>900x600          |
| W8-SA101D<br>1200x800         |

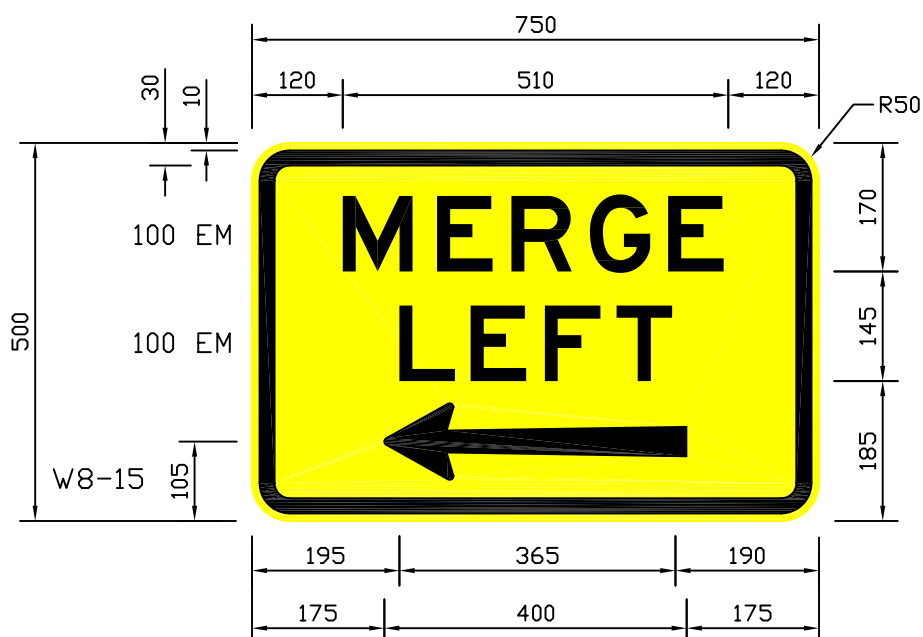

 Yellow (retro-reflective)

 Black

Note: Letters & Numerals AS1744.

 **TRANSPORT SA**

WARNING SIGN  
'Merge Left'

Statewide Operational Coordination Group  
Traffic Management Unit

Authorisation:

*A. B. Clark*

Date: 19 June, 2002

**W8-SA101**

Drawn: G.Roberts

Scale: 1:10