


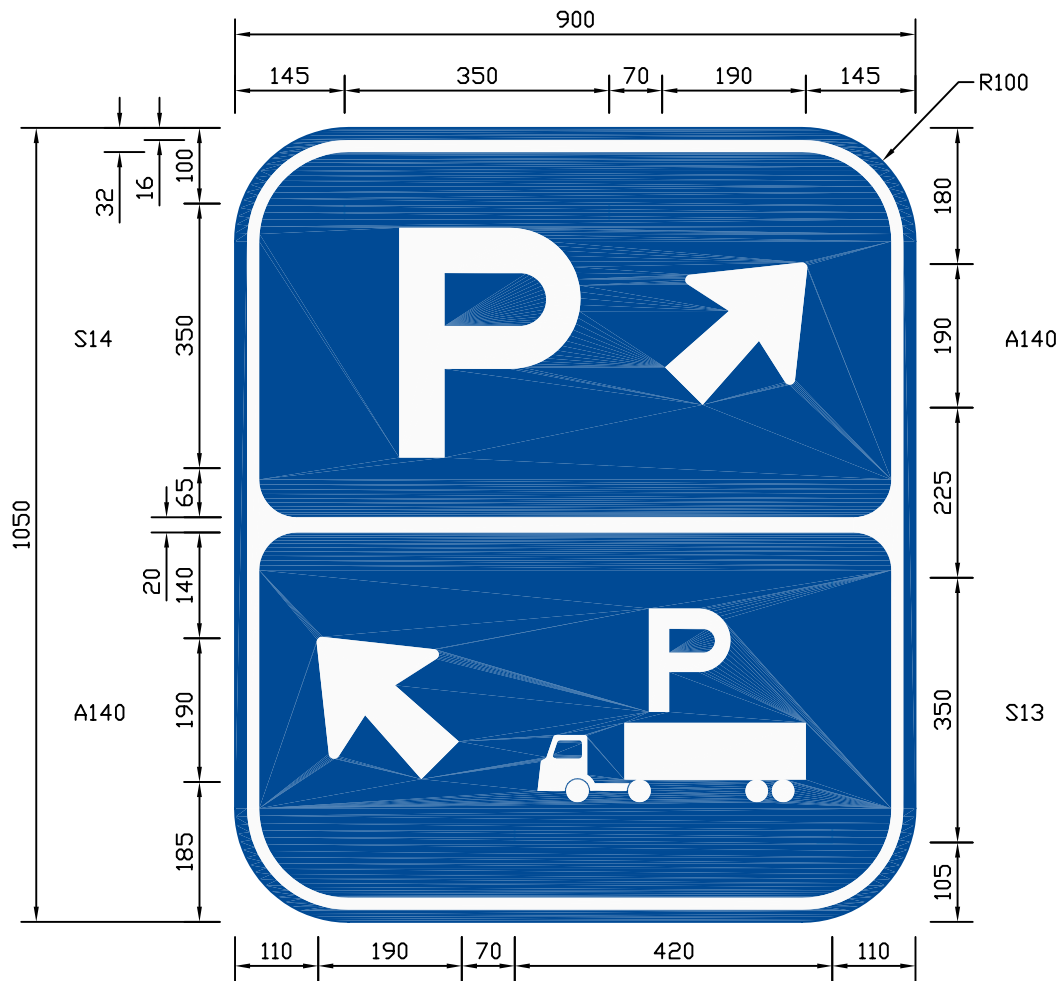

Blue (retro-reflective)

White (retro-reflective)

Note: Letters & Numerals AS1744.

TRANSPORT SA

GUIDE SIGN
'Location/Position Sign – Car Parking / \'
Truck Parking Rest Area Complex'

Statewide Operational Coordination Group
Traffic Management Unit

Authorisation:

A3 Clark

Date: 23 April, 2002

Drawn: A. Watt

Scale: 1:10

G7-SA124-2