


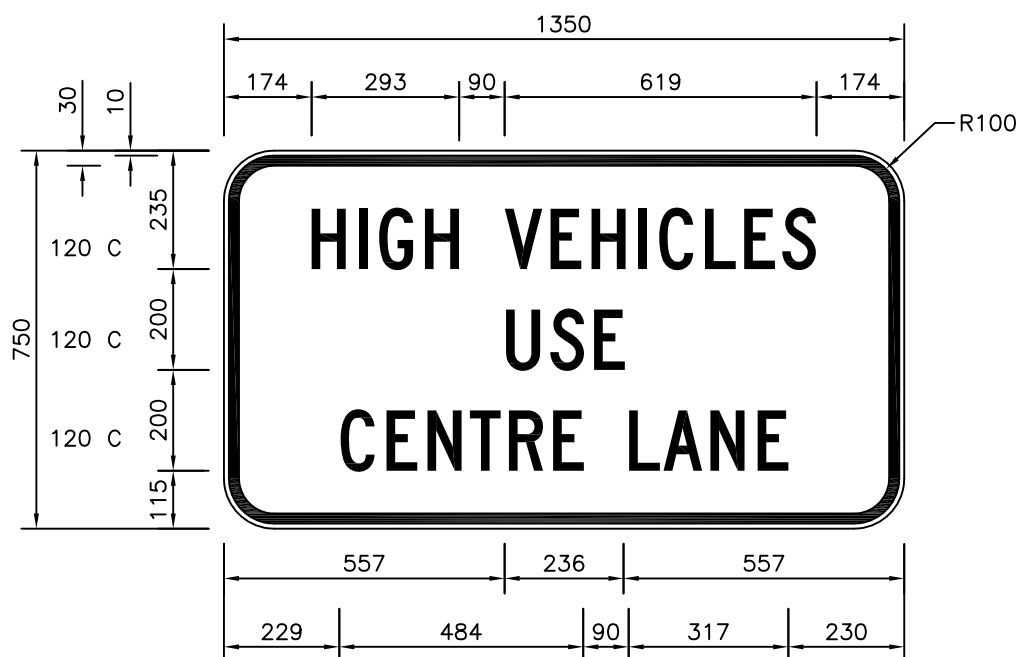

NOTE: Formally G9—SA69.

White (retro-reflective)

Black

Note: Letters & Numerals AS1744:2015.



Government of South Australia
Department of Planning,
Transport and Infrastructure

Technical Services
Safety and Service Division

Drawn: A. Simister

Scale: 1:15

Authorisation:

Date: 13 May, 2015

GUIDE SIGN

'High Vehicles Use Centre Lane'

G9-SA125