


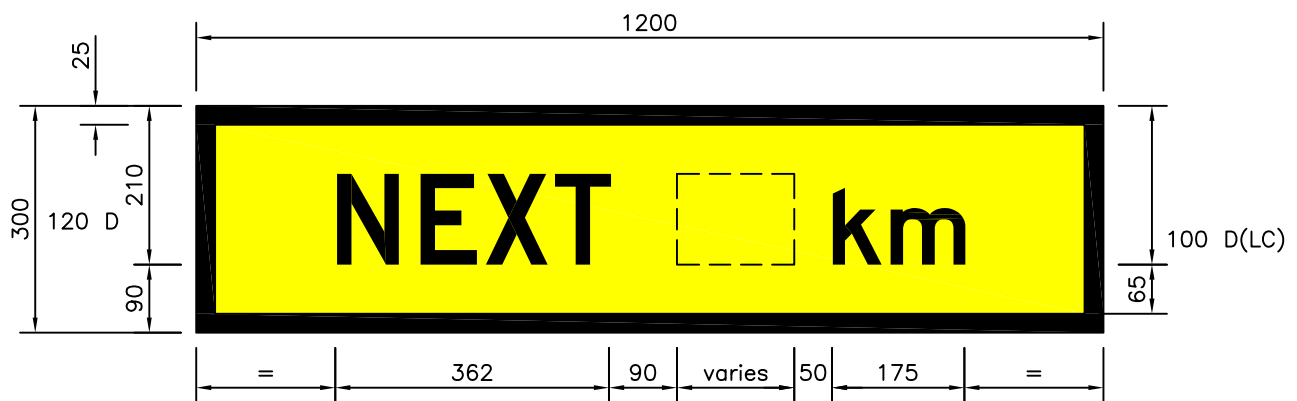

 Yellow (retro-reflective)

 Black

Note: Letters & Numerals AS1744:2015.

 Government of South Australia Department of Planning, Transport and Infrastructure	TEMPORARY WARNING SIGN 'Next Xkm'	
Technical Services Safety and Service Division	Authorisation: 	T1-SA102
Drawn: A. Simister	Scale: 1:10	Date: 23 April, 2015