


|                                       |
|---------------------------------------|
| <b>SIGN SIZE, mm</b>                  |
| <b>T1-SA104A(Illust.)</b><br>1200x600 |
| <b>T1-SA104B</b><br>1500x750          |

Border width 25 for both sizes.

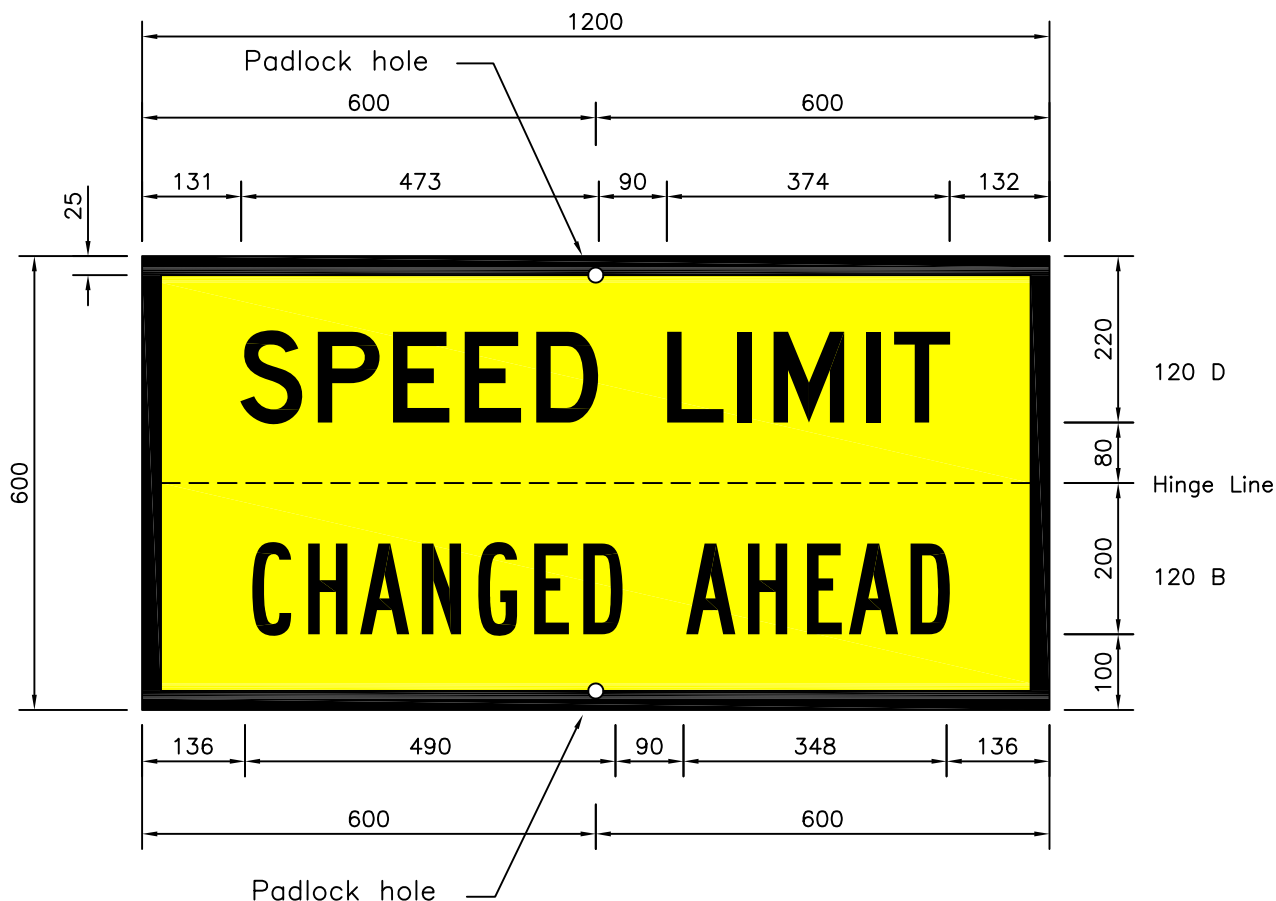

**Note:** Panel to be hinged along dotted line.  
Hinge to be constructed of non-corrosive material; either brass or stainless steel.  
Any hinge face to be covered in reflective material.  
10R padlock holes in positions shown, for sign fastening when not in use.  
For special use only. Use T1-SA103(AorB) for normal purposes.

 Yellow (retro-reflective)

 Black

Note: Letters & Numerals AS1744:2015.

|   |   |                      |  |
|---|---|----------------------|--|
|  <b>Government of South Australia</b><br>Department of Planning,<br>Transport and Infrastructure | TEMPORARY WARNING SIGN<br>'Speed Limit Changed Ahead (hinged, 2 lines)'                                |                      |  |
| Technical Services<br>Safety and Service Division   | Authorisation:<br> | <b>T1-SA104</b>      |  |
| Drawn: A. Simister   | Scale: 1:10                                                                                            | Date: 29 April, 2015 |  |