



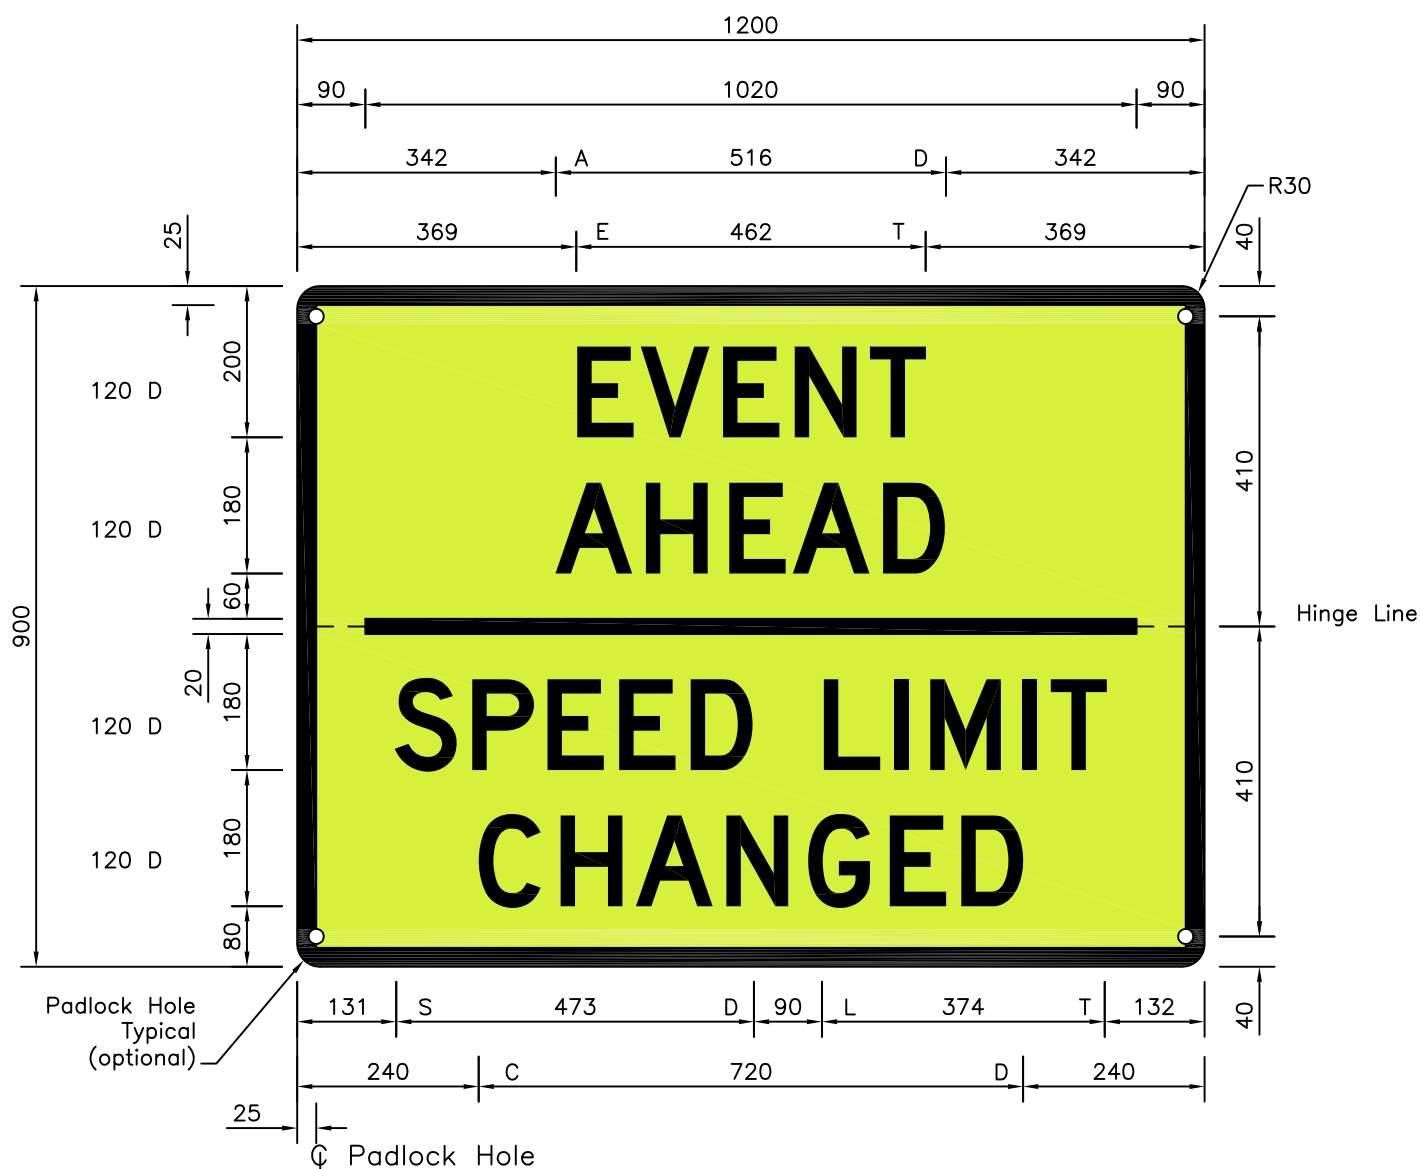

Optional: Panel to be hinged along dotted line.
Hinge to be constructed of non-corrosive material; either brass or stainless steel.
Any hinge face to be covered in reflective material.
10R padlock holes in positions shown, for sign fastening when not in use.

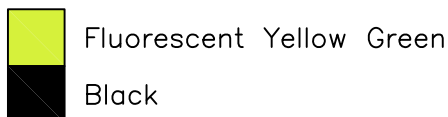

Note: Letters & Numerals AS1744:2015.

 Government of South Australia Department of Planning, Transport and Infrastructure	TEMPORARY WARNING SIGN 'Community Event – Speed Limit Changed'		
Technical Services Safety and Service Division Drawn: A. Simister	Authorisation:  Date: 29 April, 2015	T1-SA106	
	Scale: 1:10		