



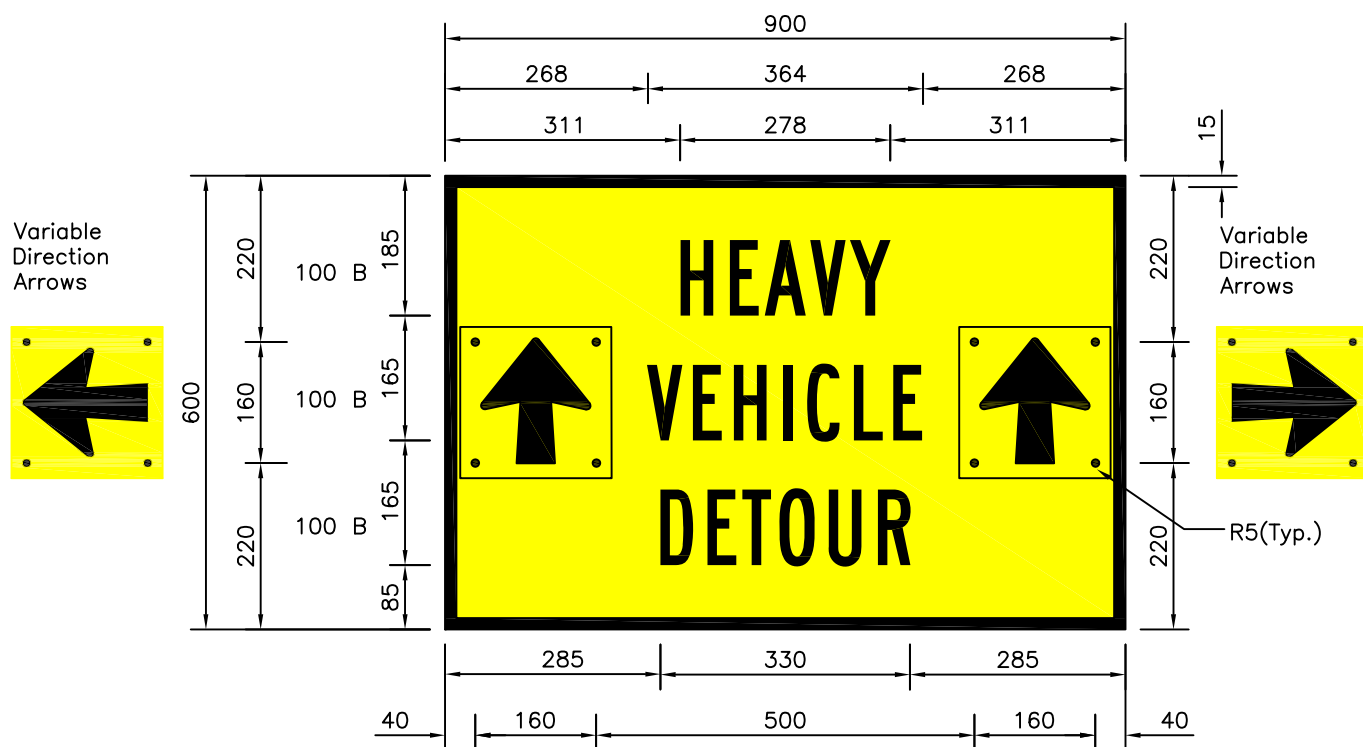

#### CHANGEABLE PLATE DETAILS

(2 No. Required)

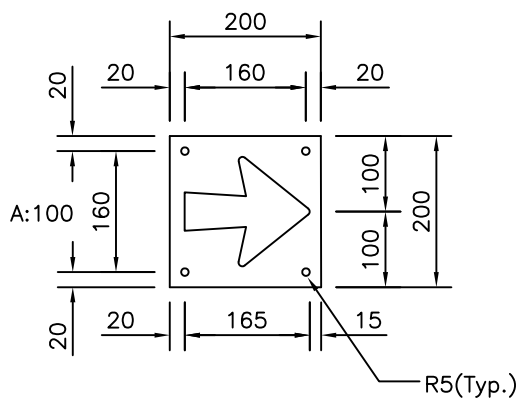

 Yellow (retro-reflective)

 Black

Note: Letters & Numerals AS1744:2015.



**Government of South Australia**  
Department of Planning,  
Transport and Infrastructure

Technical Services  
Safety and Service Division

Drawn: A. Simister

Scale: 1:10

Authorisation:

Date: 29 April, 2015

TEMPORARY WARNING SIGN

'Heavy Vehicle Detour (variable direction arrows)

**T1-SA113**