


SIGN SIZE, mm
T1-SA119A(Illust.) 900x675
T1-SA119B 1200x900

Border width 25mm
for both size signs.

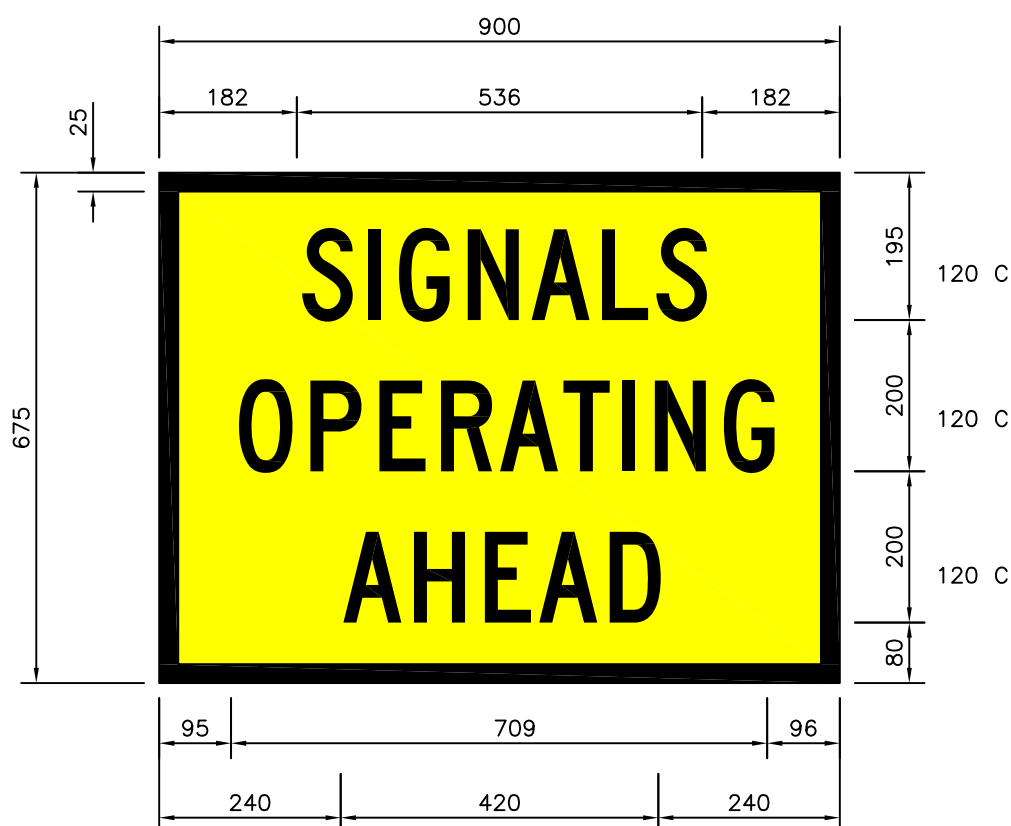

 Yellow (retro-reflective)

 Black

Note: Letters & Numerals AS1744:2015.



Government of South Australia
Department of Planning,
Transport and Infrastructure

Technical Services
Safety and Service Division

Drawn: A. Simister

Scale: 1:10

Authorisation:

Date: 30 April, 2015

TEMPORARY WARNING SIGN

'Signals Operating Ahead'

T1-SA119