


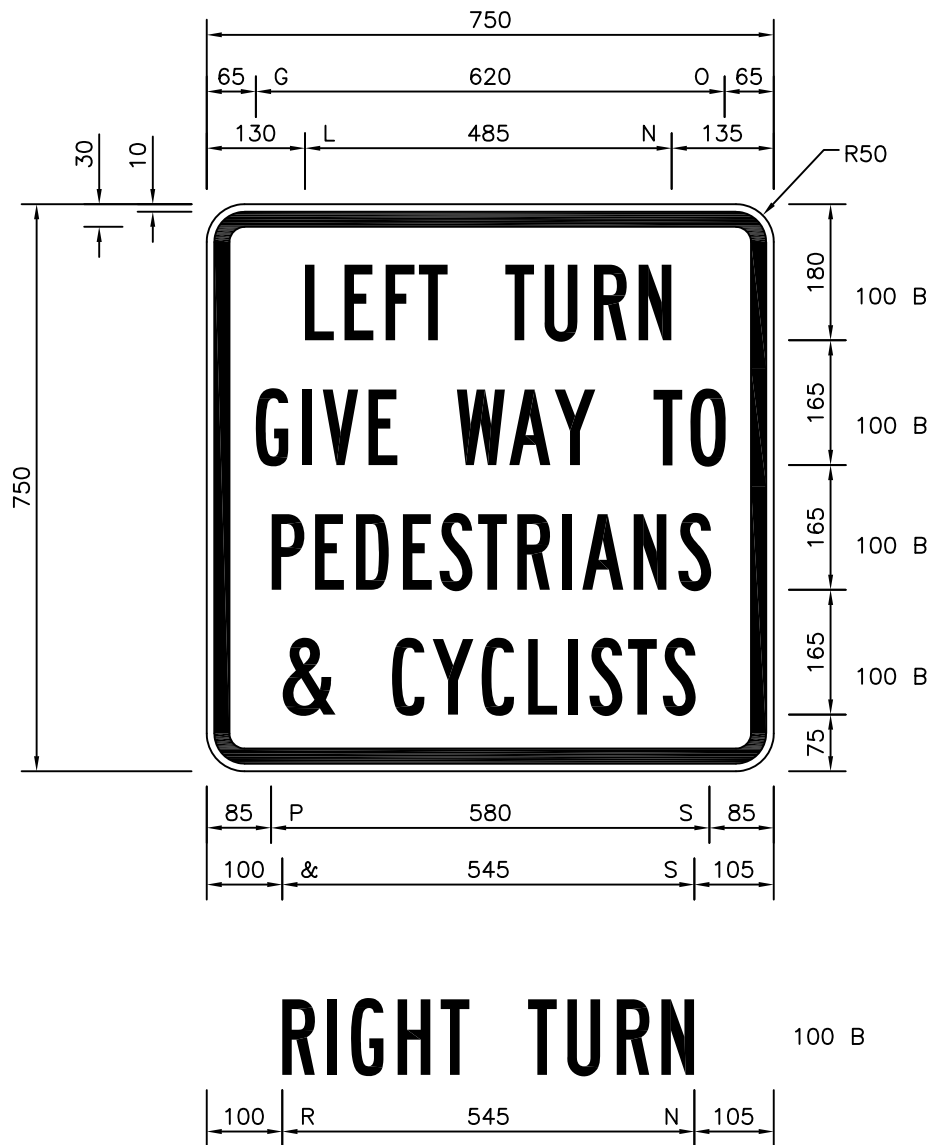

White (retro-reflective)

Black

Note: Letters & Numerals AS1744:2015.



Government of South Australia
Department of Planning,
Transport and Infrastructure

Road and Marine Services
Traffic Services, Traffic Solutions Unit

Drawn: A. Simister

Scale: 1:10

Authorisation:

Date: 23 April, 2019

REGULATORY SIGN

'Left or Right Turn Give Way To Pedestrians & Cyclists'

R2-SA102
(LorR)