


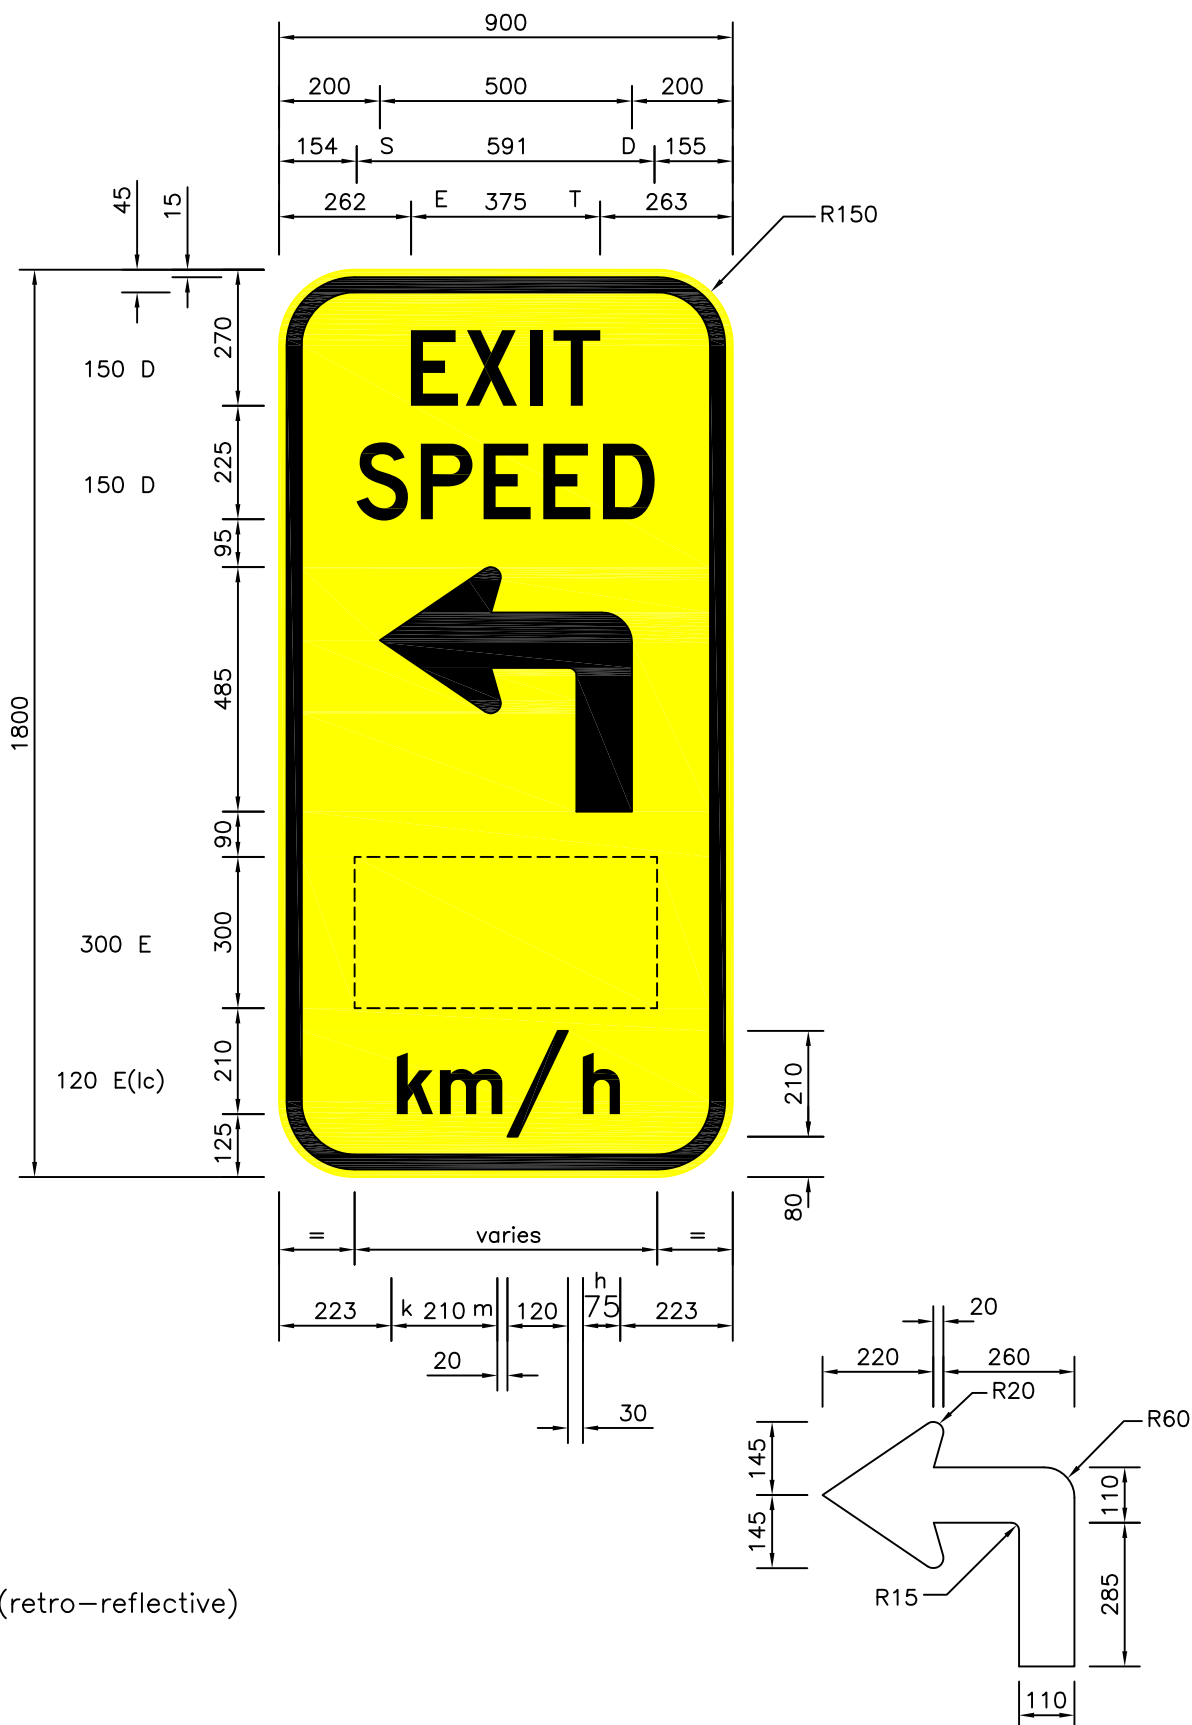

**Government of South Australia**  
 Department of Planning,  
 Transport and Infrastructure

Safety & Service Division  
 Technical Services Section

Drawn: A. Simister

Scale: 1:15

Authorisation:

Date: 19 May, 2015

WARNING SIGN  
 'Exit Speed Turn ...km/h'

**W1-9-3AA**  
**(LorR)**