


Safety & Service Division

Traffic Operations, Traffic Solutions Unit

Specific Road Signs - Specifications, South Australia

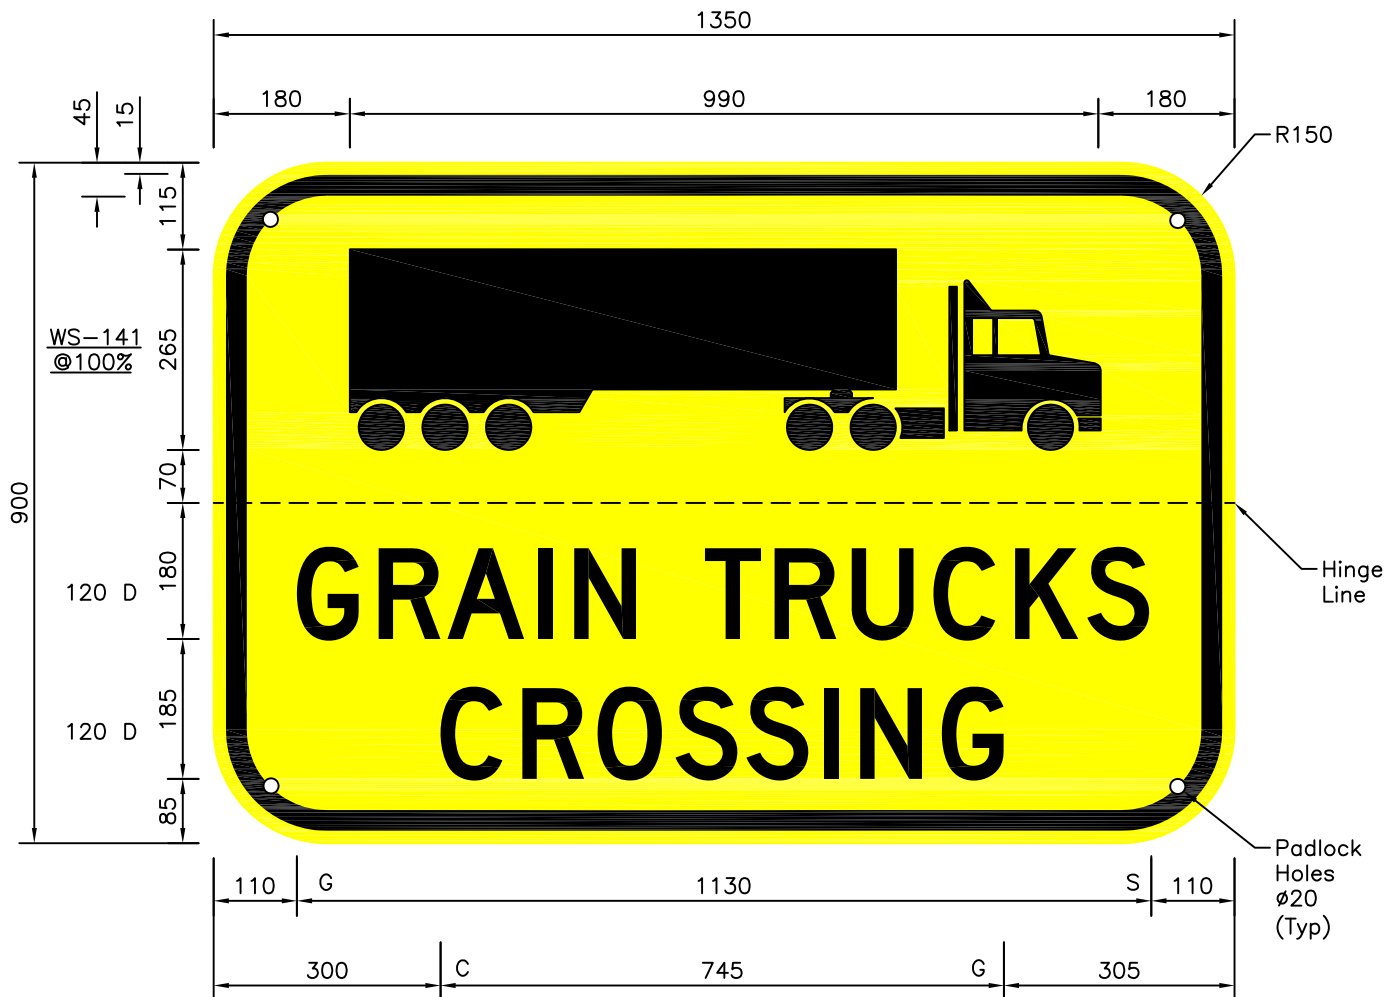

ADDITIONAL REFERENCE NOTES:

WS141 – Refer to TES14016

Hinge: To be constructed of non-corrosive material;
refer to Master Specification R48.
Any hinge face to be covered in retroreflective material.



Black

Yellow class 1

Scale: 1:10

ALL DIMENSIONS ARE IN MILLIMETRES

Total Sign Area: 1.20 sqm

Sign Type: Warning

Location: Various

Drawn: A. Simister
Edition: A Rev: 5
Date: 14 September, 2016

Authorisation:
Date:

TES 9899