



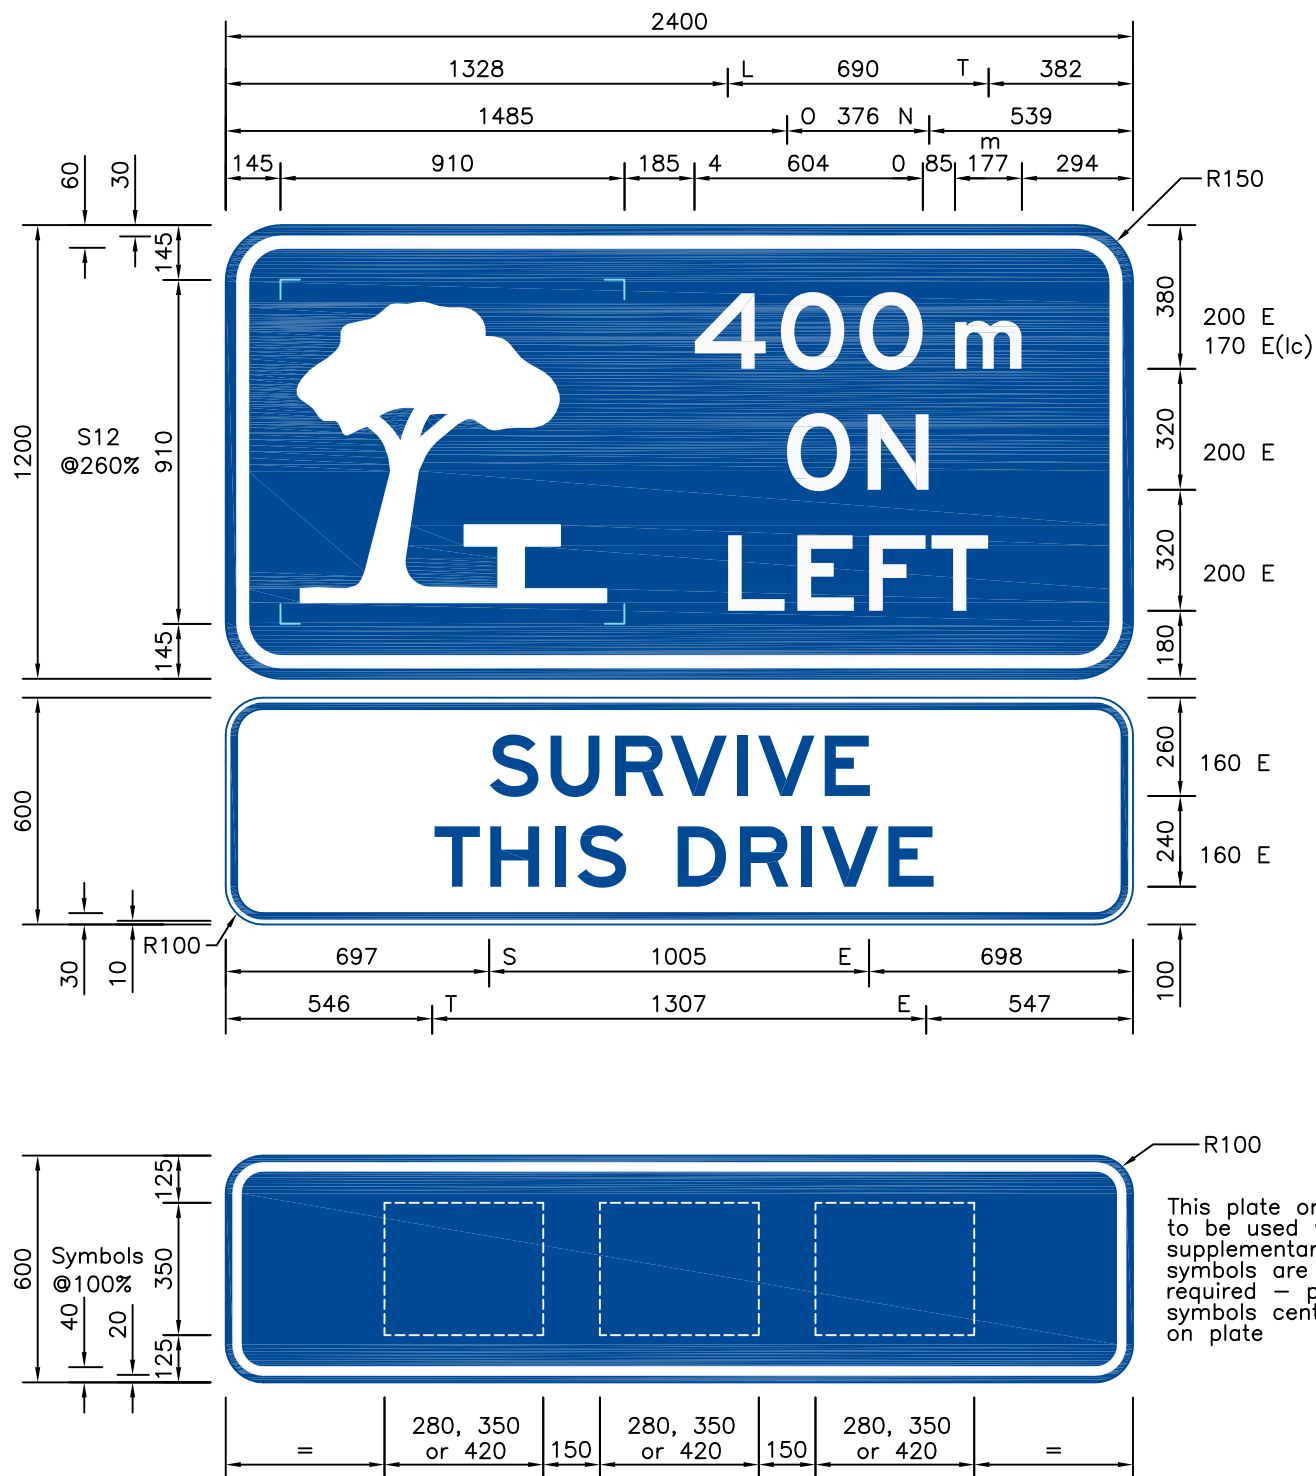

ADDITIONAL REFERENCE NOTES:
TES 14016 – Symbol Detail Sheet.

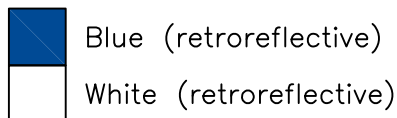

Note: Letters & Numerals AS1744:2015.

 Government of South Australia Department of Planning, Transport and Infrastructure	GUIDE SIGN Rest Area 400m on Left – Survive This Drive	
Technical Services Safety and Service Division	Authorisation:  Date: 12 May, 2015	G7-SA130-5
Drawn: A. Simister	Scale: 1:20	