


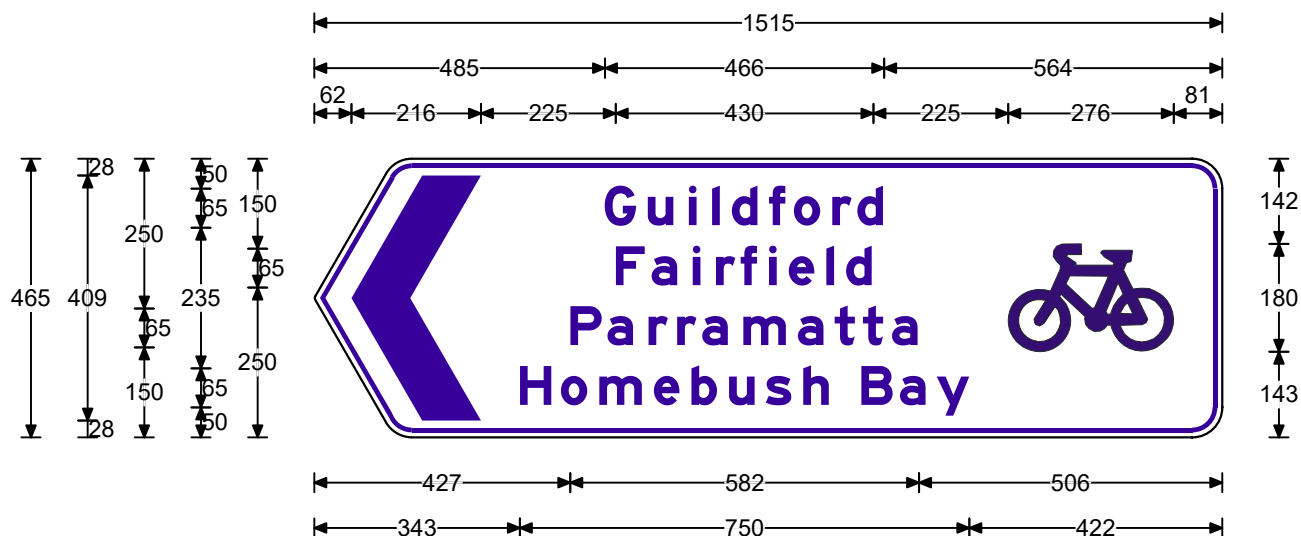

Legend

Guildford
Fairfield
Parramatta
Homebush Bay

Font Type


FHWA Series Em2000EX
FHWA Series Em2000EX
FHWA Series Em2000EX
FHWA Series Em2000EX

Font Size

65
65
65
65


Specifications:
ALUMINIUM SIGN:
Cl.400 Blue refl legend, symbol, chevron and
border(AS1906.1).
Cl.400 White refl ground(AS1906.1).

Size:	465 x 1515	Date:	17/2/21
Area:	0.7 sq.m	Scale:	1:12.6
Border:	8 x 8	Drawn:	casselm
Cnr Rad:	50	Checked:	
Patch CR:	NA	File:	g2-204-4n_L
 		Path:	\\panda01.rta.nsw.gov.au\DATA\Signs\Signs\TTT\DRAWINGS\GUI\DE\TraSiCAD
Prepared using TraSiCAD Product of QMR		Marty Cassell - 0268611656 Guidance & Delineation	G2-204-4n_L

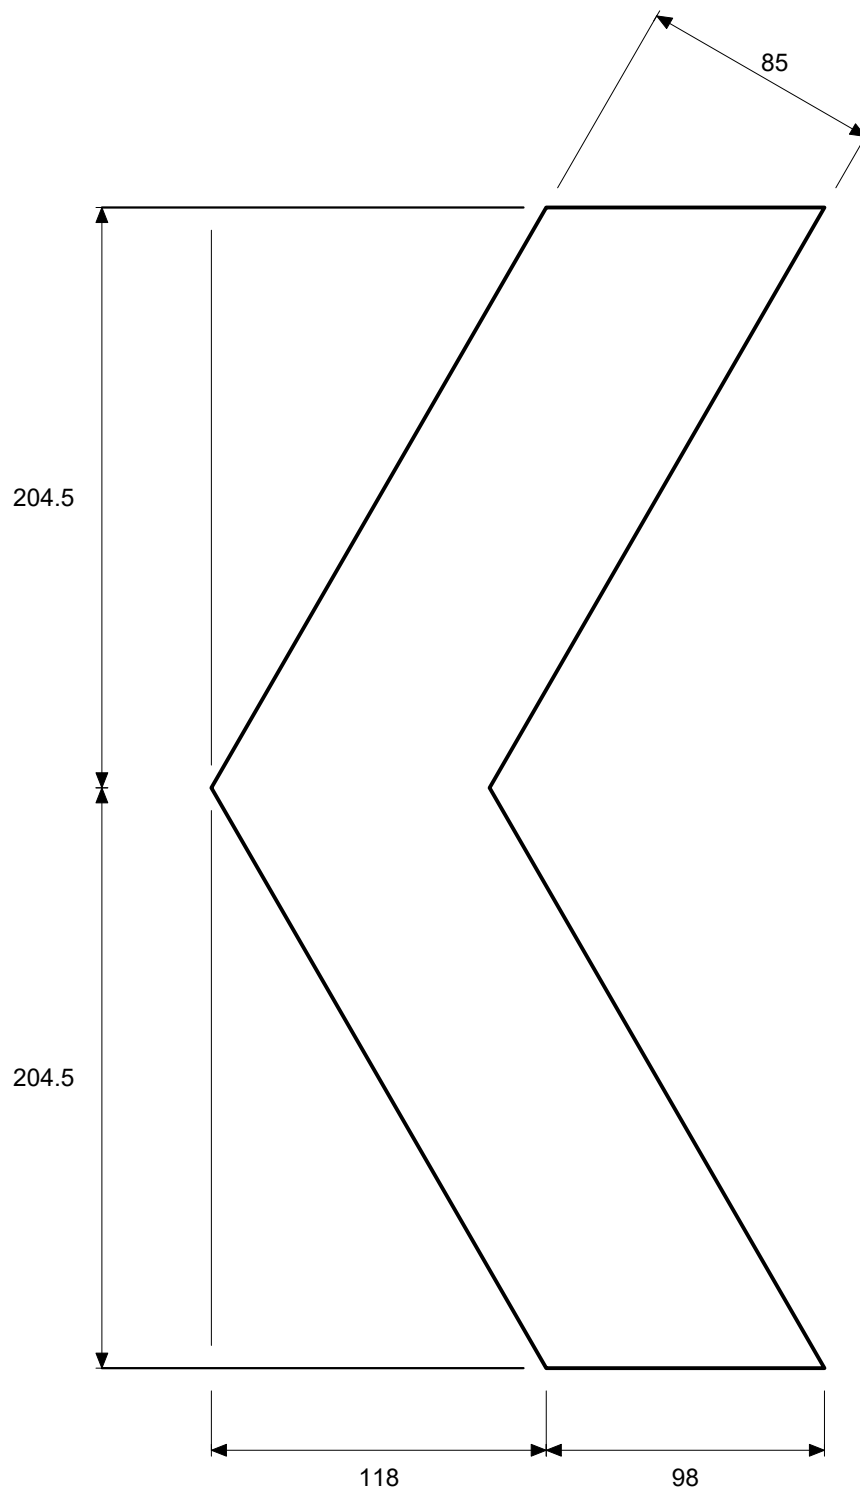

Details of Sign Face Symbols

Size:	465 x 1515	Date:	17/2/21
Area:	0.7 sq.m		
Border:	8 x 8	Drawn:	casselm
Cnr Rad:	50	Checked:	
		File:	g2-204-4n_l
 		Path:	\\panda01.rfa.nsw.gov.au\DATA\Signs\Signs\TTT\DRAWINGS\GUI\DEV\TrasCAD
Prepared using TraSICAD Product of QMR		Marty Cassell - 0268611656 Guidance & Delineation	G2-204-4n_L

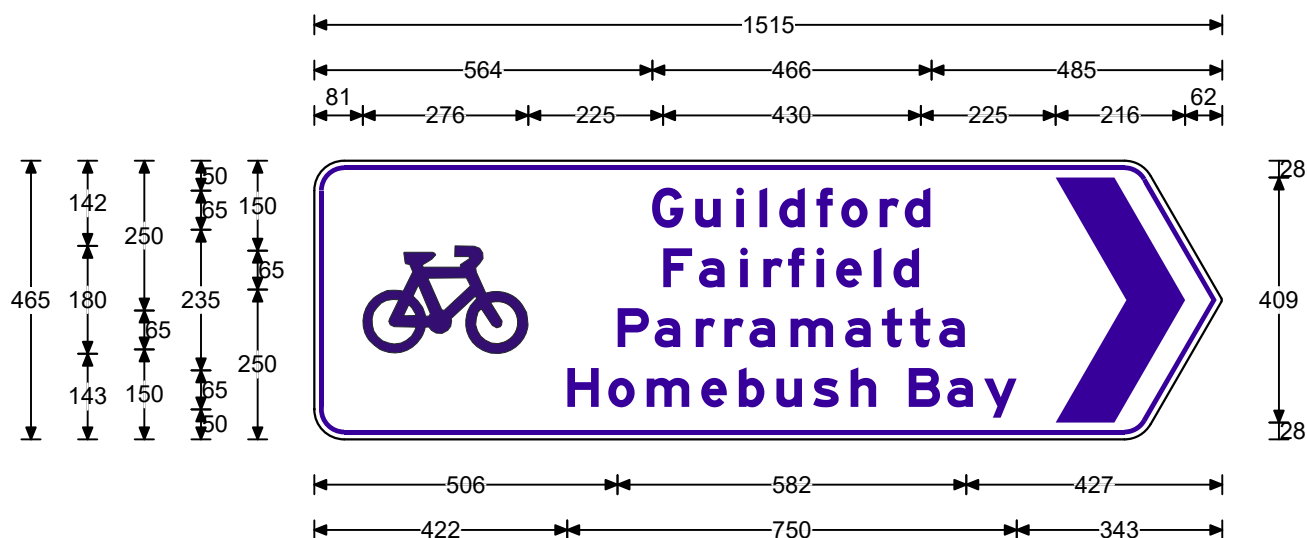

Legend

Guildford
Fairfield
Parramatta
Homebush Bay

Font Type


FHWA Series Em2000EX
FHWA Series Em2000EX
FHWA Series Em2000EX
FHWA Series Em2000EX

Font Size

65
65
65
65

Specifications:
ALUMINIUM SIGN:
Cl.400 Blue refl legend, symbol, chevron and
border(AS1906.1).
Cl.400 White refl ground(AS1906.1).

Size:	465 x 1515	Date:	17/2/21
Area:	0.7 sq.m	Scale:	1:12.6
Border:	8 x 8	Drawn:	casselm
Cnr Rad:	50	Checked:	
Patch CR:	NA	File:	g2-204-4n_r
 Transport for NSW	Path: \\panda01.rta.nsw.gov.au\DATA\Signs\Signs\TTT\DRAWINGS\GUI\DEV\TraSICAD		
	Marty Cassell - 0268611656 Guidance & Delineation		
Prepared using TraSICAD Product of QMR		G2-204-4n_R	

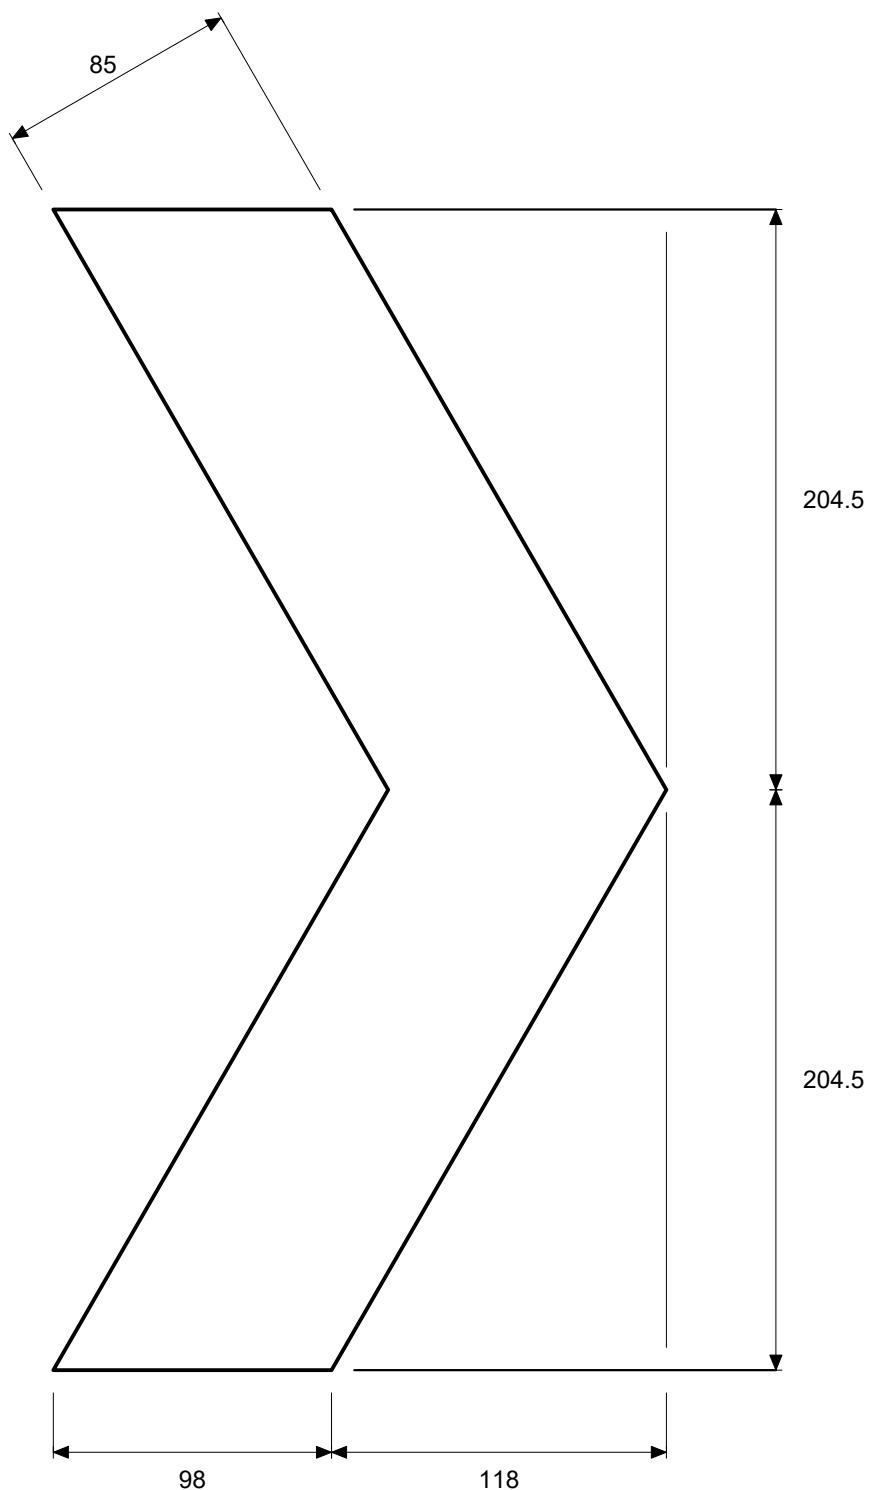

Details of Sign Face Symbols

Size:	465 x 1515	Date:	17/2/21
Area:	0.7 sq.m		
Border:	8 x 8	Drawn:	casselm
Cnr Rad:	50	Checked:	
		File:	g2-204-4n_r
		Path:	\\panda01.rfa.nsw.gov.au\DATA\Signs\Signs\TTT\DRAWINGS\GUI\DEV\TraSiCAD
		Marty Cassell - 0268611656 Guidance & Delineation	
Prepared using TraSiCAD Product of QMR		G2-204-4n_R	