


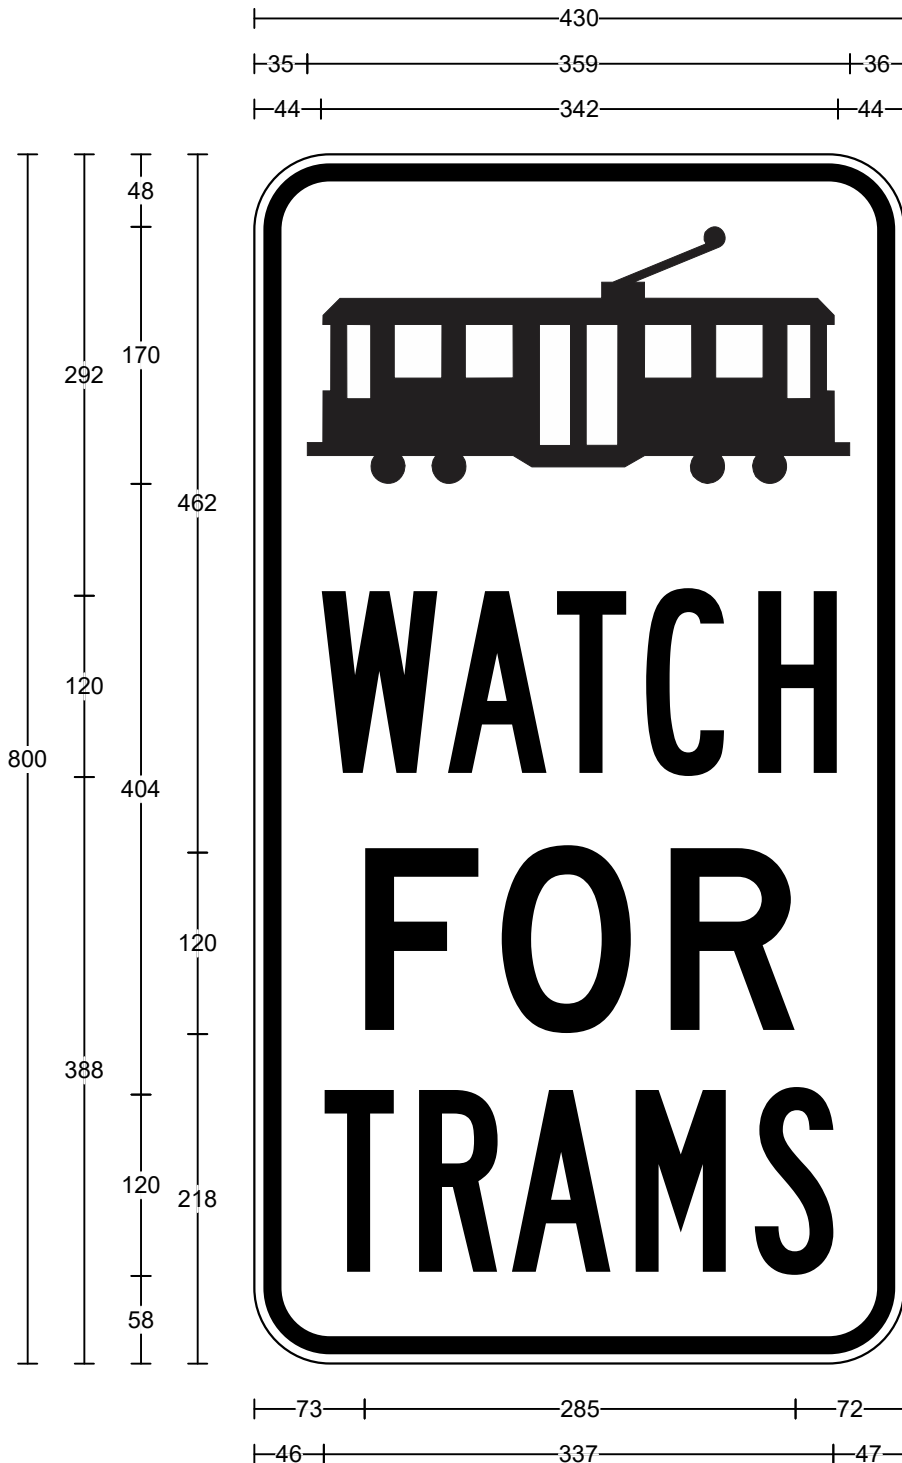

<u>Legend</u>	<u>Font Type</u>	<u>Font Size</u>
WATCH	FHWA Series B2000EX	120
FOR	FHWA Series D2000EX	120
TRAMS	FHWA Series B2000EX	120

Specifications:
Aluminium Sign
Black lgd
Cl.400 White refl grd(AS1906.1)

Size:	800 x 430	Date:	15/12/21
Area:	0.34 sq.m	Scale:	1:5
Border:	6 x 12	Drawn:	rozsoj
Cnr Rad:	50	Checked:	
Patch CR:	NA	File:	g5-204n
 Transport for NSW		Path: H:\Signs\TTT\DRAWINGS\GUIDE\TrasiCAD	
Prepared using TraSICAD Product of QMR		Guidance & Delineation Team Advanced Technical Services Infrastructure & Place 99 Phillip St Parramatta NSW 2150	G5-204n