



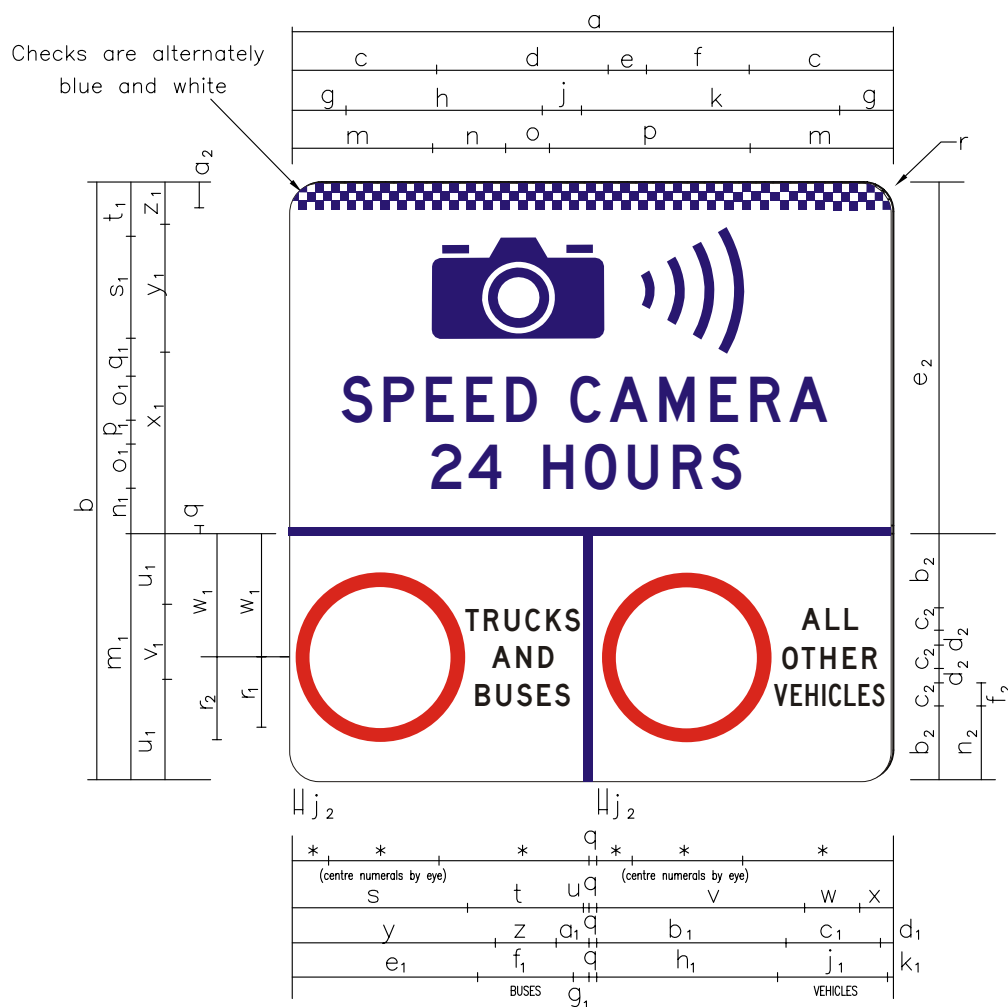

	a	b	c	d	e	f	g	h	j	k	m	n	o	p	q	r	r ₁	r ₂	s	t	u
G6-327-3 B	1590	1582	380	454	101	275	145	517	103	680	458	382	102	190	22	80	185	220	465	304	15
G6-327-3 C	2650	2630	635	756	168	456	241	862	172	1134	764	636	170	316	36	130	237	297	738	510	60

v	w	x	y	z	a ₁	b ₁	c ₁	d ₁	e ₁	f ₁	g ₁	h ₁	i ₁	k ₁	m ₁	n ₁	o ₁	p ₁	q ₁
549	146	89	536	162	86	508	250	26	490	254	40	475	294	15	648	120	120 DM	60	101
867	242	197	860	266	182	781	414	111	781	424	103	748	480	78	1080	200	200 DM	100	164

s ₁	t ₁	u ₁	v ₁	w ₁	x ₁	y ₁	z ₁	a ₂	b ₂	c ₂	d ₂	e ₂	f ₂	g ₂
270	143	224	2 numerals 3 numerals 200 DN	324	495	336	109	66	193	60DM	40	934	60CN	24
448	238	420	2 numerals 3 numerals 240 DN	540	818	560	182	108	320	100DM	70	1550	100CN	40

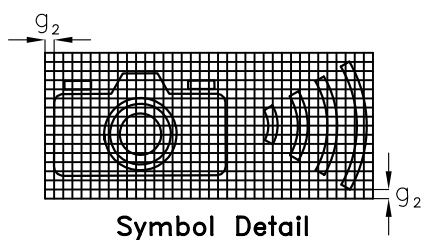

SCALE:1:20

TITLE

GUIDE SIGN

G6-327-3

Drawn: FR

18-06-15

CHKD:



GUIDANCE AND DELINEATION UNIT
 27-31 ARGYLE ST, PARRAMATTA 2150

H:\SIGNS\TTT\DRAWINGS\PLOT\ GUIDE \ G6-327-3.DWG

Revision: ...