



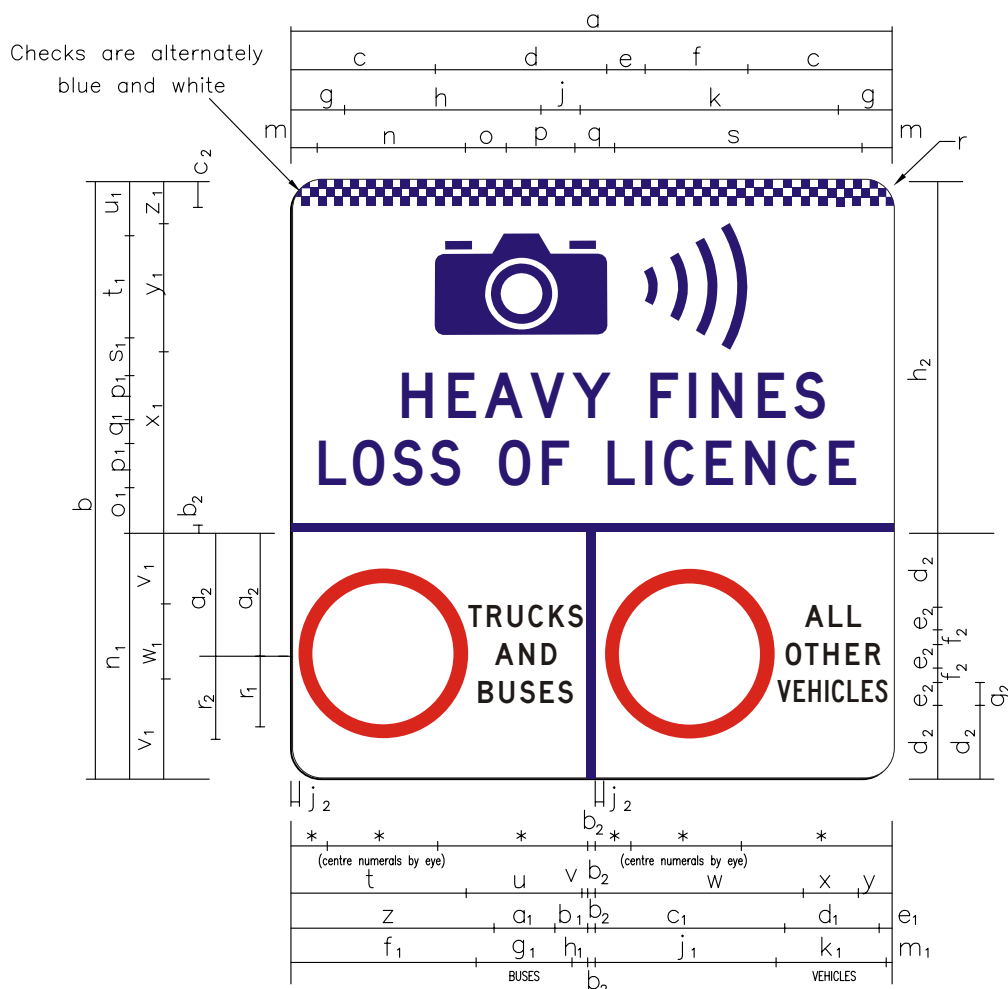

	a	b	c	d	e	f	g	h	j	k	m	n	o	p	q	r	r ₁	r ₂	s	t
G6-329-3 B	1590	1582	380	454	101	275	145	517	103	680	67	382	102	190	110	80	237	297	672	465
G6-329-3 C	2650	2630	635	756	168	456	241	862	172	1134	112	636	170	316	183	130	365	445	1120	737

u	v	w	x	y	z	a ₁	b ₁	c ₁	d ₁	e ₁	f ₁	g ₁	h ₁	j ₁	k ₁	m ₁	n ₁	o ₁	p ₁
304	15	549	146	89	536	162	86	508	250	37	490	254	40	475	294	15	648	120	120 DM
510	60	868	242	197	838	268	181	781	414	111	782	424	103	749	480	78	1080	200	200 DM

q ₁	s ₁	t ₁	u ₁	v ₁	w ₁	x ₁	y ₁	z ₁	a ₂	b ₂	c ₂	d ₂	e ₂	f ₂	g ₂	h ₂	j ₂
60	101	270	143	224	2 numerals 200 DN	489	336	109	324	22	66	194	60DM	40	60CN	934	20
100	164	448	238	420	2 numerals 240 DN	808	560	182	540	36	108	320	100DM	70	100CN	1550	70

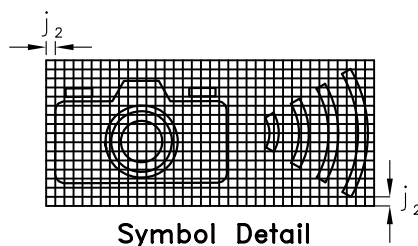

SCALE:1:20

TITLE

GUIDE SIGN

G6-329-3

Drawn: FR

18-06-15

CHKED:



GUIDANCE AND DELINEATION UNIT
27-31 ARGYLE ST, PARRAMATTA 2150

H:\SIGNS\TTT\DRAWINGS\PLT\ GUIDE \ G6-329-3.DWG

Revision: ...