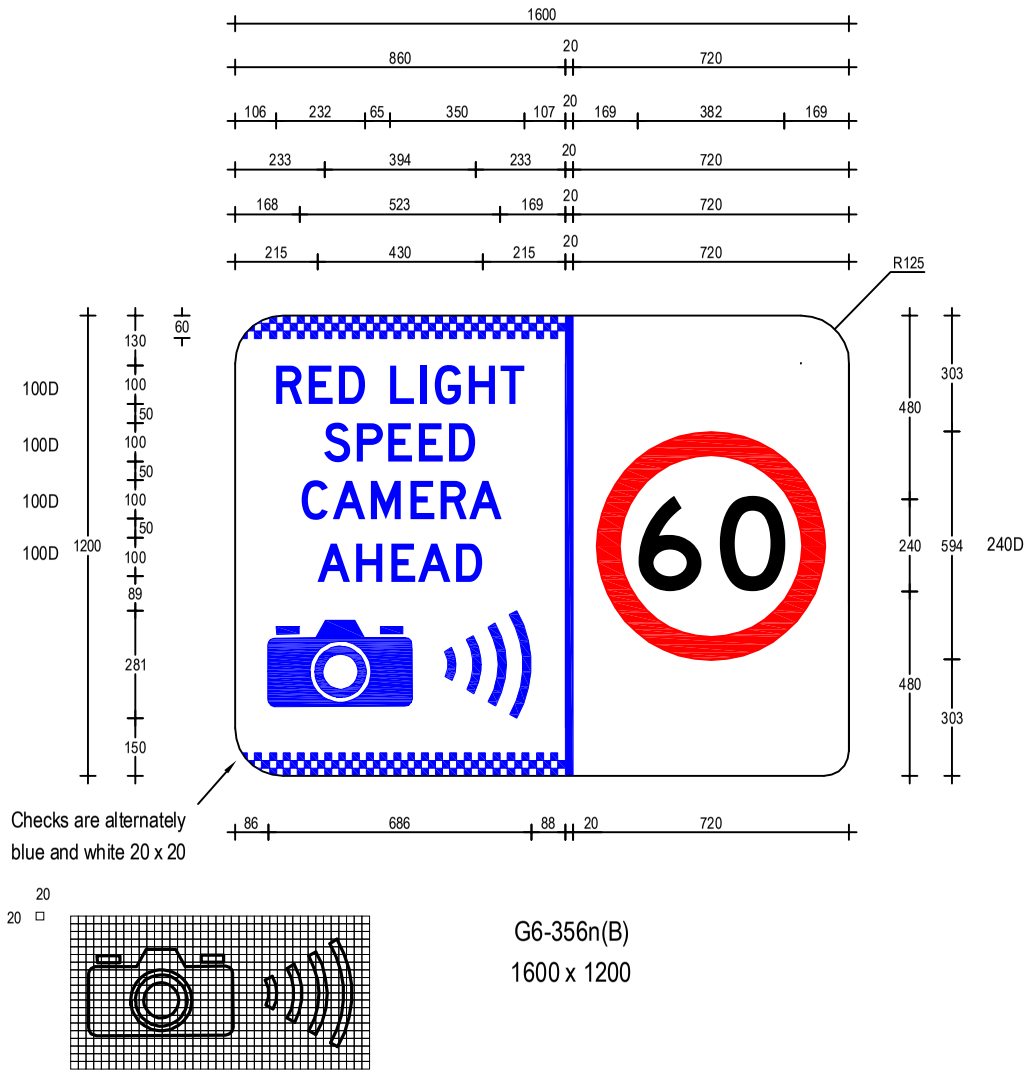

G6-356n(B)
1600 x 1200

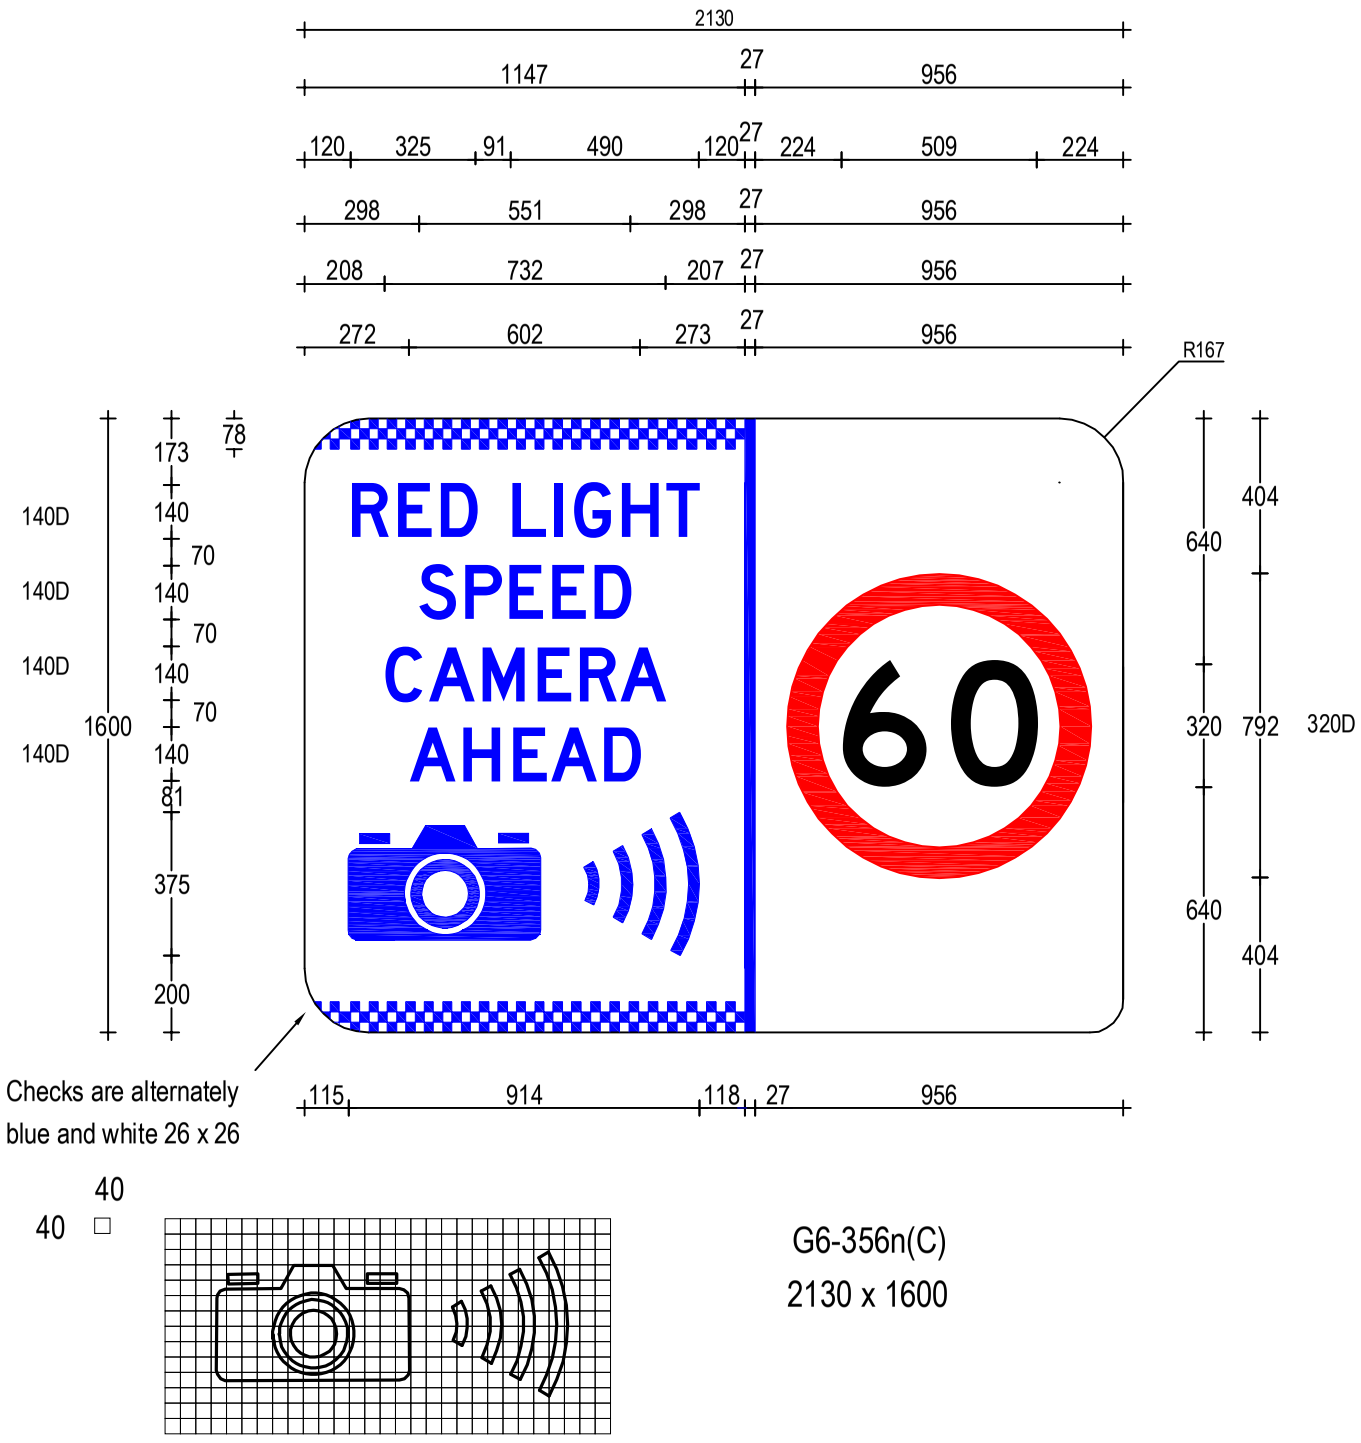

G6-356n(C)
2130 x 1600

ACCEPTED FOR CONSTRUCTION

QR CODE / Scan to Check Document Version	REV	DATE	AMENDMENT / REVISION DESCRIPTION	APPROVAL
	01	23-08-18	AS Fonts & material classification revised	P.Oliver

DRAWING FILE LOCATION / NAME: H:\SIGNS\TTT\DRAWINGS\PLOT\TEMP\T1-11N.DWG

MATERIALS: ALUMINIUM SIGN
LEFT PANEL:- AS1906.1 CL.400 BLUE REFL LEGEND
CHECKS AND SYMBOL ON CL.400 WHITE REFL GROUND
RIGHT PANEL:- BLACK NUMERAL., AS1906.1 CL.400 RED
REFL ANNULUS ON AS1906.1 WHITE REFL GROUND

ALL DIMENSIONS ARE IN MILLIMETRES UNLESS OTHERWISE SPECIFIED

SIGN TO BE MANUFACTURED IN ACCORDANCE WITH RMS QA SPECIFICATION 3400

DESIGNED
SIGNED
NAME M.Davies
DATE 31-07-19

REVIEWED
SIGNED
NAME J.Rozos
DATE 31-07-19

VERIFIED
SIGNED
NAME P.Oliver
TITLE Manager Guidance & Delineation
DATE 31-07-19

NSW GOVERNMENT Transport Roads & Maritime Services

PREPARED BY
GUIDANCE AND DELINEATION UNIT
TRAFFIC ENGINEERING SERVICES
TECHNICAL AND PROJECT SERVICES

GUIDE SIGN
G6-356N
RED LIGHT SPEED CAMERA AHEAD

A

SHEET 1 OF 1

SCALE: 1:20 | EDMS No. XXXXXXXXXX | SHEET No. 1 | ISS 0

© Roads and Maritime Servic

THIS DRAWING MAY BE PREPARED IN COLOUR AND MAY BE INCOMPLETE IF COPIED
50mm ON A3 SIZE ORIGINAL