



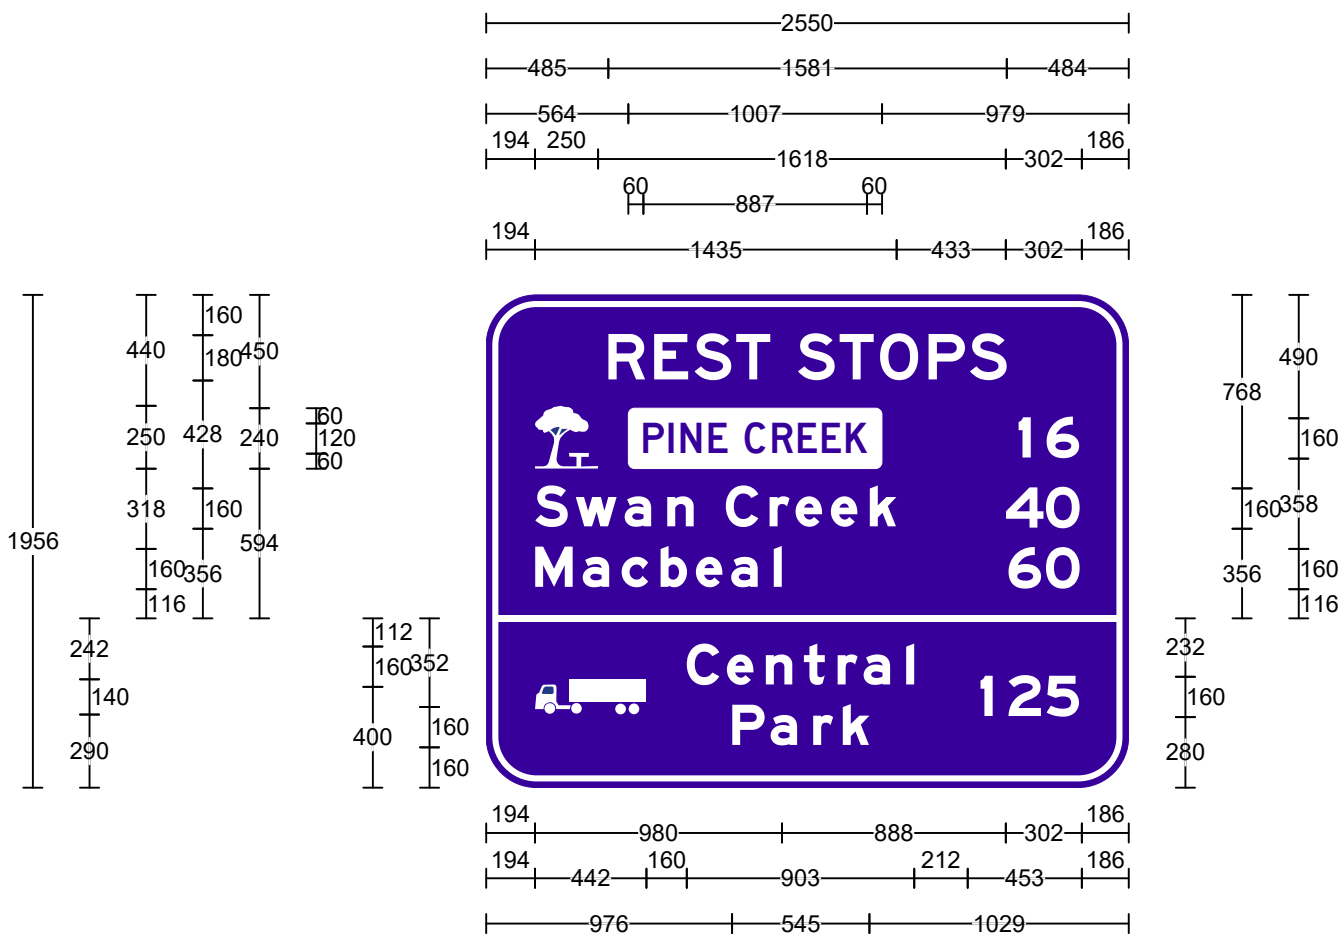

Specifications:
 Aluminium Sign
 Cl.400 White refl lgd(AS1906.1)
 Cl.400 Blue refl grd(AS1906.1)
 Patch:- Cl.400 Blue refl lgd on Cl.400 White refl grd


Size:	1956 x 2550	Date:	26/9/22
Area:	4.99 sq.m	Scale:	1:30
Border:	24 x 24	Drawn:	
Cnr Rad:	200	Checked:	
Patch CR:	25	File:	g7-259-2n_a
		Path:	H:\Signs\TTT\DRAWINGS\GUIDE\TrasiCAD
Prepared using TraSiCAD Product of QMR		G7-259-2n(A) Example Only	

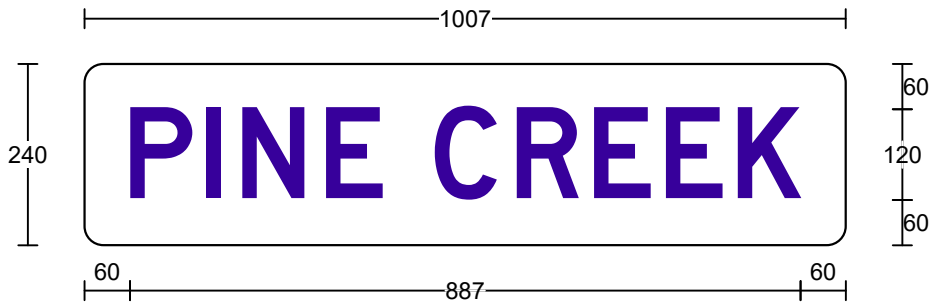

<u>Legend</u>	<u>Font Type</u>	<u>Font Size</u>
PINE CREEK	FHWA Series D2000EX	120

Patch Detail


Size:	240 x 1007	Date:	26/9/22
Area:	0.24 sq.m	Scale:	1:10
Border:	0 x 0	Drawn:	
Cnr Rad:	25	Checked:	
Patch CR:	NA	File:	g7-259-2n_a
		Path:	H:\Signs\TTT\DRAWINGS\GUIDE\TrasiCAD
Prepared using TraSiCAD Product of QMR		G7-259-2n(A) Example Only	

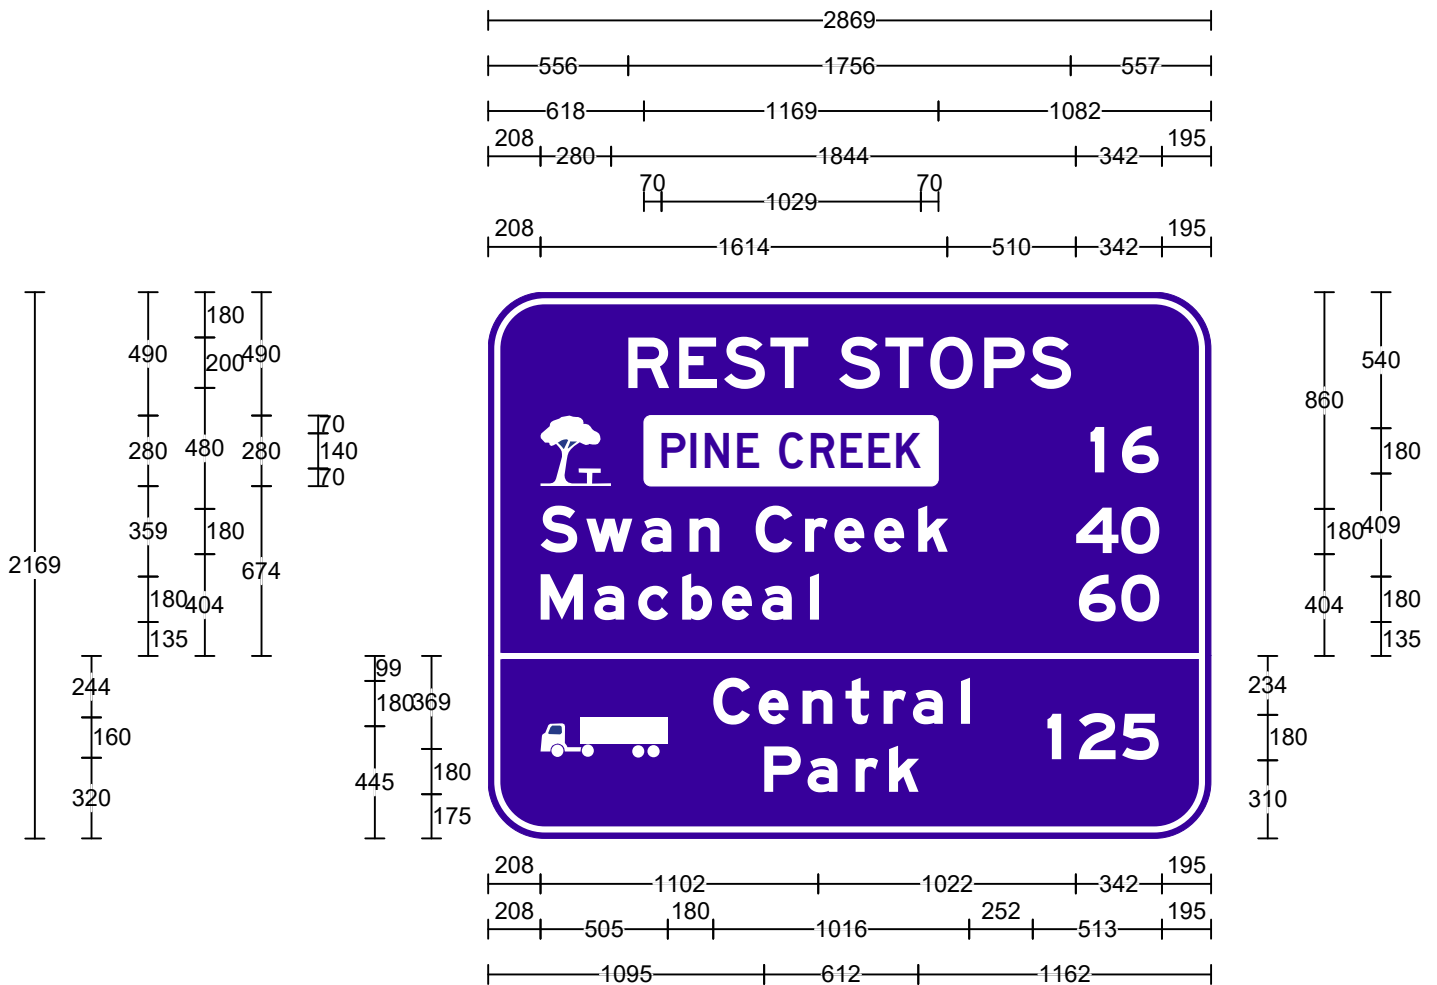

<u>Legend</u>	<u>Font Type</u>	<u>Font Size</u>
REST STOPS	FHWA Series E2000EX	200
16	FHWA Series E2000EX	180
PINE CREEK	FHWA Series D2000EX	140
40	FHWA Series E2000EX	180
Swan Creek	FHWA Series Em2000EX	180
60	FHWA Series E2000EX	180
Macbeal	FHWA Series Em2000EX	180
Central	FHWA Series Em2000EX	180
125	FHWA Series E2000EX	180
Park	FHWA Series Em2000EX	180

Specifications:
 Aluminium Sign
 Cl.400 White refl lgd(AS1906.1)
 Cl.400 Blue refl grd(AS1906.1)
 Patch: Cl.400 Blue refl lgd on Cl.400 White refl grd

Size:	2169 x 2869	Date:	26/9/22
Area:	6.22 sq.m	Scale:	1:30
Border:	24 x 24	Drawn:	
Cnr Rad:	225	Checked:	
Patch CR:	28	File:	g7-259-2n_b
		Path:	H:\Signs\TTT\DRAWINGS\GUIDE\TrasiCAD
Prepared using TraSiCAD Product of QMR		G7-259-2n(B) EXAMPLE ONLY	

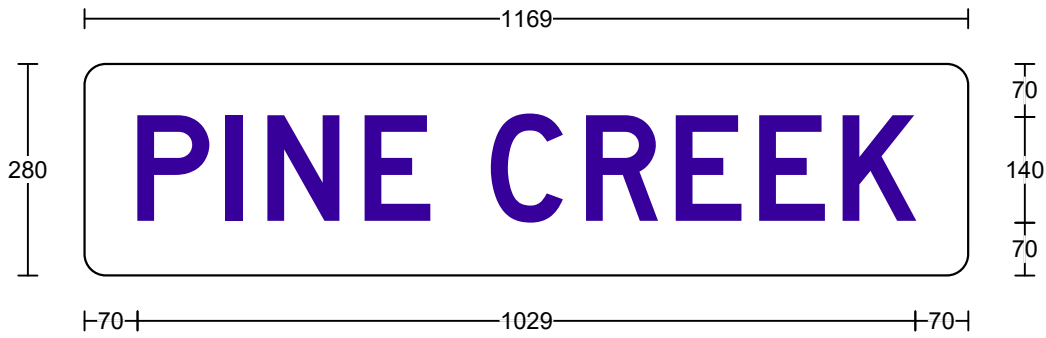

<u>Legend</u>	<u>Font Type</u>	<u>Font Size</u>
PINE CREEK	FHWA Series D2000EX	140

Patch Detail

Size:	280 x 1169	Date:	26/9/22
Area:	0.33 sq.m	Scale:	1:10
Border:	0 x 0	Drawn:	
Cnr Rad:	28	Checked:	
Patch CR:	NA	File:	g7-259-2n_b
		Path:	H:\Signs\TTT\DRAWINGS\GUIDE\TrasiCAD
Prepared using TraSiCAD Product of QMR		G7-259-2n(B) EXAMPLE ONLY	