
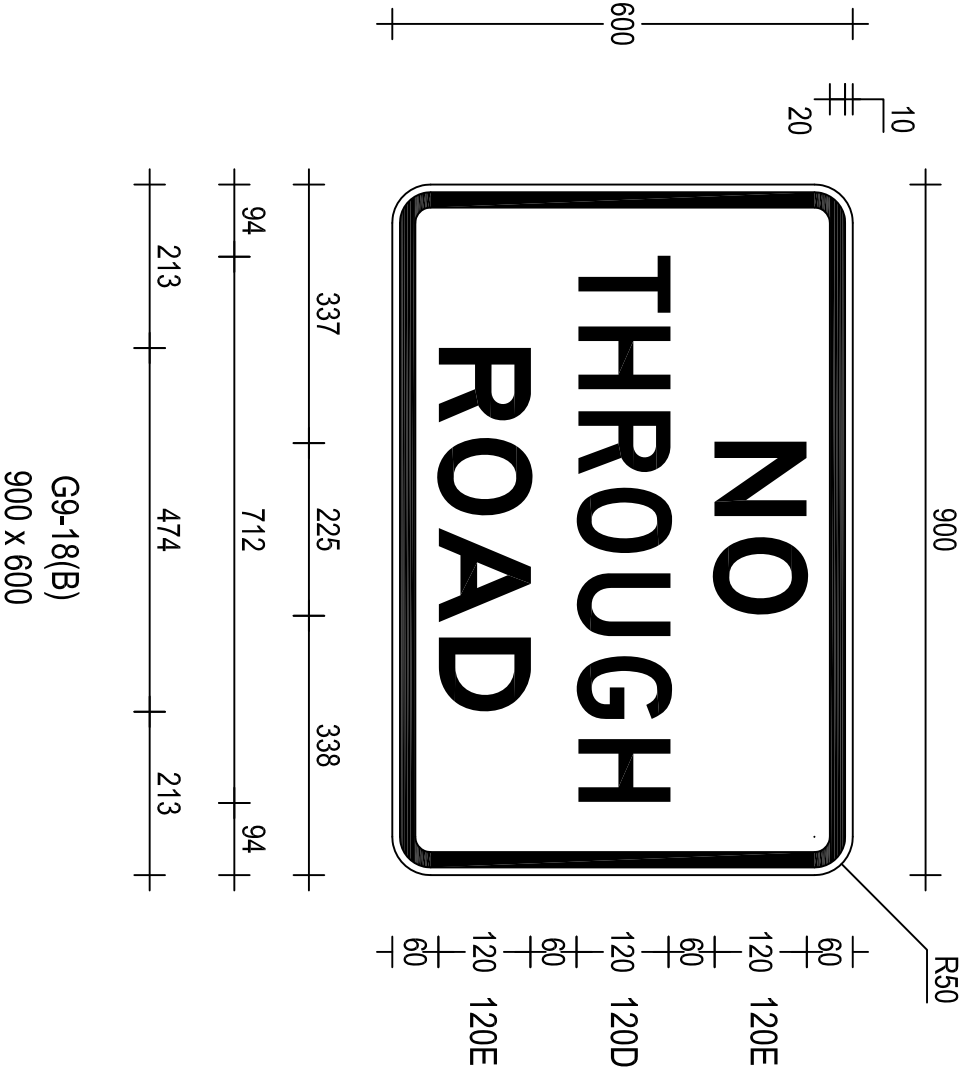


OR CODE	Scan to Check Document Version	REV	DATE	AMENDMENT / REVISION DESCRIPTION	APPROVAL	DRAWING FILE LOCATION / NAME: H:\SIGN\TTT\DRAWINGS\PLOT\GUIDE\G9-18.DWG	DESIGNED	VERIFIED	PREPARED BY	GUIDE SIGN	A3
		01	23-03-18	AS Forms & material classification revised	P. Oliver		NAME: M. Davies DATE: 24-3-21	NAME: P. Oliver TITLE: Manager, Guidance & Delineation DATE: 24-03-21	NSW GOVERNMENT Transport Roads & Maritime Services	G9-18 NO THROUGH ROAD	
ALL DIMENSIONS ARE IN MILLIMETRES UNLESS OTHERWISE SPECIFIED						SIGN TO BE MANUFACTURED IN ACCORDANCE WITH RMS QA SPECIFICATION 3400	NAME: J. Rozos DATE: 24-03-21		GUIDANCE AND DELINEATION UNIT ADVANCED TECHNICAL SERVICES INFRASTRUCTURE AND PLACE	SHEET 1 OF 1 SCALE: 1:10	
										EDMS No. XXXXXXXXXX SHEET No. 1 ISSUE 01	

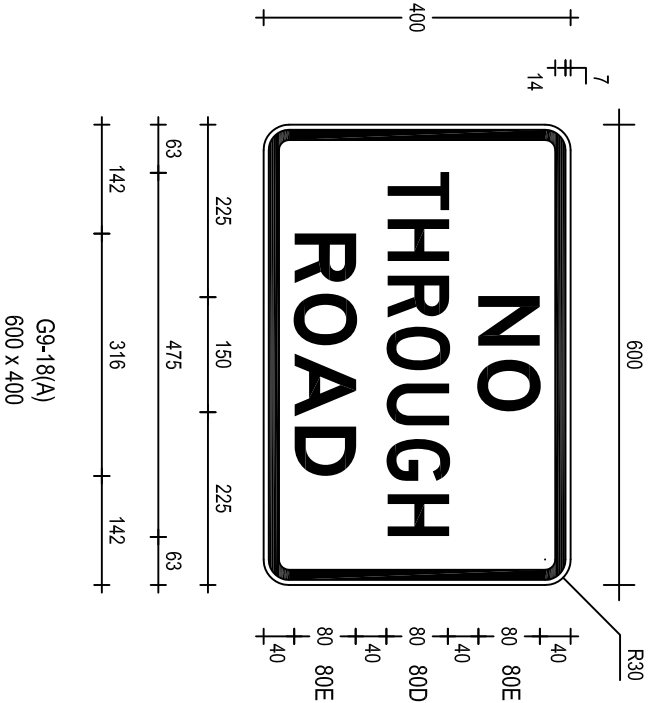

ACCEPTED FOR CONSTRUCTION