


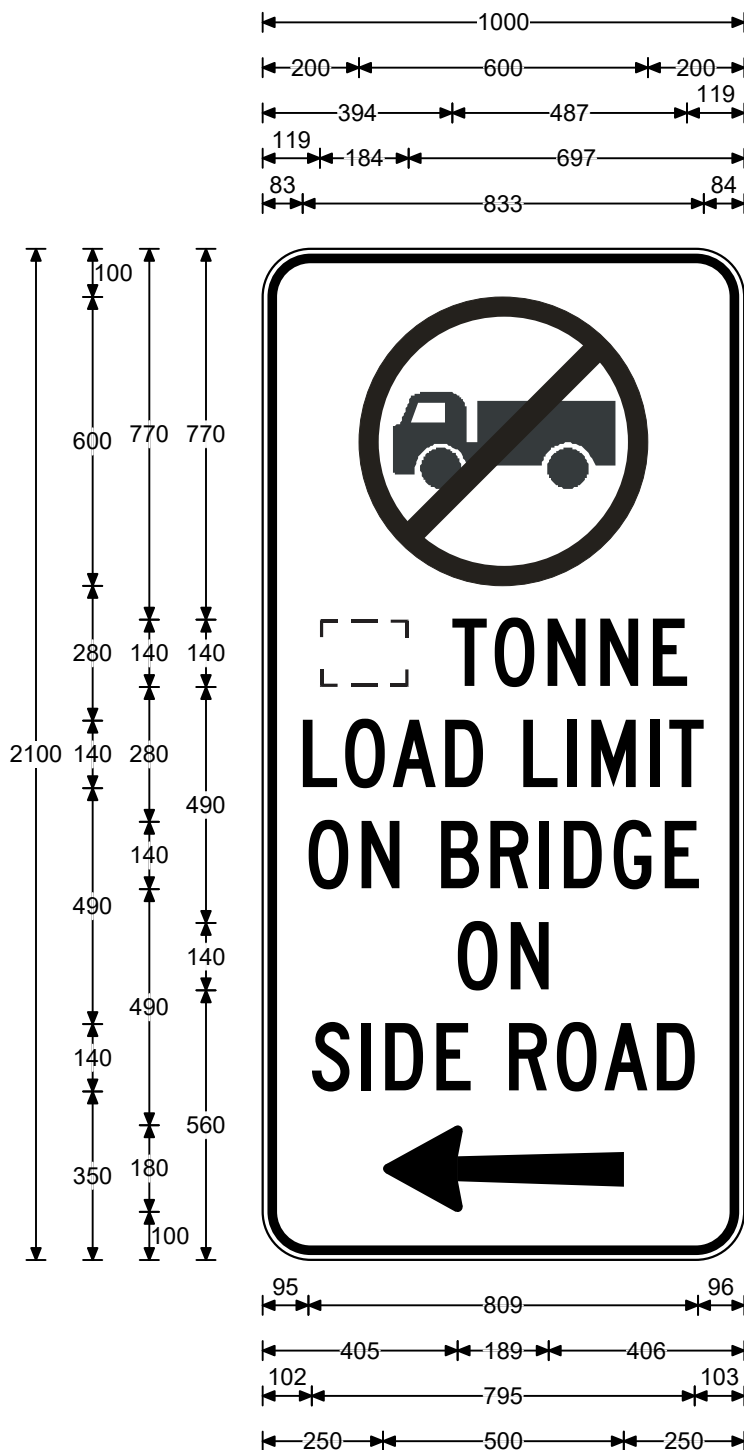

Legend

TONNE
LOAD LIMIT
ON BRIDGE
ON
SIDE ROAD

Font Type

FHWA Series C2000EX
FHWA Series C2000EX
FHWA Series C2000EX
FHWA Series C2000EX
FHWA Series C2000EX

Font Size

140
140
140
140
140

1st line of text is variable in width dependant on numeral text used & centred in available space.


Specifications:

ALUMINIUM SIGN:

Black legend, arrow & border.

Cl.400 White refl ground(AS1906.1).

Size:	2100 x 1000	Date:	13/5/21
Area:	2.1 sq.m	Scale:	1:15.7
Border:	10 x 20	Drawn:	casselm
Cnr Rad:	100	Checked:	
Patch CR:	NA	File:	g9-322n_a_l
		Path: \\panda01.rta.nsw.gov.au\DATA\Signs\Signs\111\DRAWINGS\GUI\DE\TrasCAD Marty Cassell - 0268611656 Guidance & Delineation	
		G9-322n_A_L	
Prepared using TraSICAD Product of QMR			

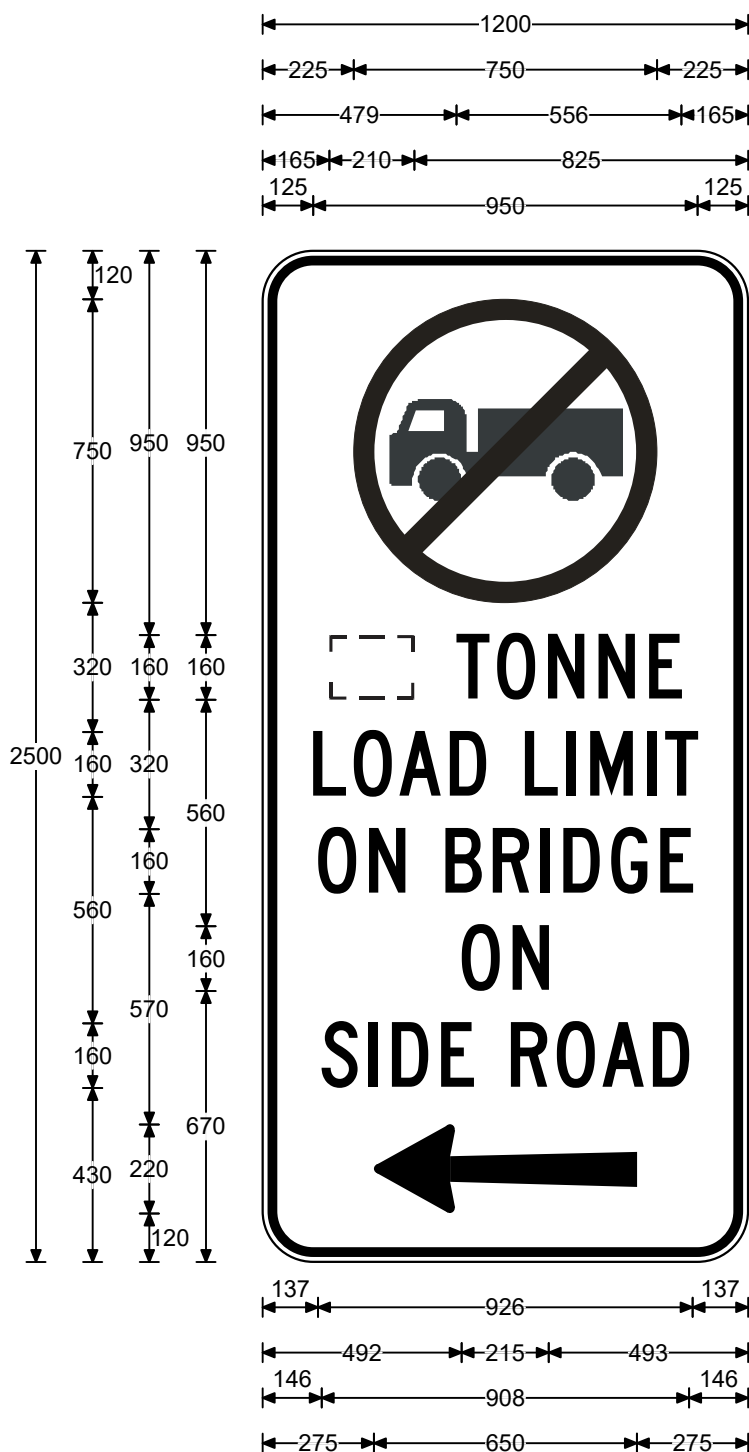

Legend

TONNE
LOAD LIMIT
ON BRIDGE
ON
SIDE ROAD

Font Type

FHWA Series C2000EX
FHWA Series C2000EX
FHWA Series C2000EX
FHWA Series C2000EX
FHWA Series C2000EX

Font Size

160
160
160
160
160

1st line of text is variable in width dependant on numeral text used & centred in available space.

Specifications: ALUMINIUM SIGN: Black legend, arrow & border. Cl.400 White refl ground(AS1906.1).	Size:	2500 x 1200	Date:	13/5/21
	Area:	3 sq.m	Scale:	1:18.7
	Border:	12 x 24	Drawn:	casselm
	Cnr Rad:	125	Checked:	
	Patch CR:	NA	File:	g9-322n_b_l
 		Path: \\panda01.rta.nsw.gov.au\DATA\Signs\Signs\111\DRAWINGS\GUI DE\TrasCAD Marty Cassell - 0268611656 Guidance & Delineation		
Prepared using TraSICAD Product of QMR		G9-322n_B_L		