


05101520253035404550mm ON A3 SIZE ORIGINAL

QR CODE	Scan to Check Document Version	REV	DATE	AMENDMENT / REVISION DESCRIPTION	APPROVAL	DRAWING FILE LOCATION / NAME: H:\SIGNS\TTT\DRAWINGS\PI\OT\GUIDE\G9-328\DWG	DESIGNED	VERIFIED	PREPARED BY	GUIDE SIGN	EDMS No.	SHEET No.	ISS
		01	23-08-18	AS Fonts & material classification revised	P Oliver		SIGNED: M Davies NAME: M Davies DATE: 31-07-19	SIGNED: P Oliver NAME: P Oliver TITLE: Manager, Guidance & Delineation DATE: 31-07-19	NSW GOVERNMENT Transport Roads & Maritime Services	G9-328N_R	XXXXXXXXXX	1	0
ALL DIMENSIONS ARE IN MILLIMETRES UNLESS OTHERWISE SPECIFIED							SHEET 1 OF 1						
SIGN TO BE MANUFACTURED IN ACCORDANCE WITH RMS QA SPECIFICATION 3400							SCALE: 1:10						

MATERIALS: ALUMINIUM SIGN
BLACK LEGEND CHEVRON AND BORDER
ON AS1906.1 CL.400 YELLOW REFLECTORISED GROUND

G9-328n_R
975 x 450

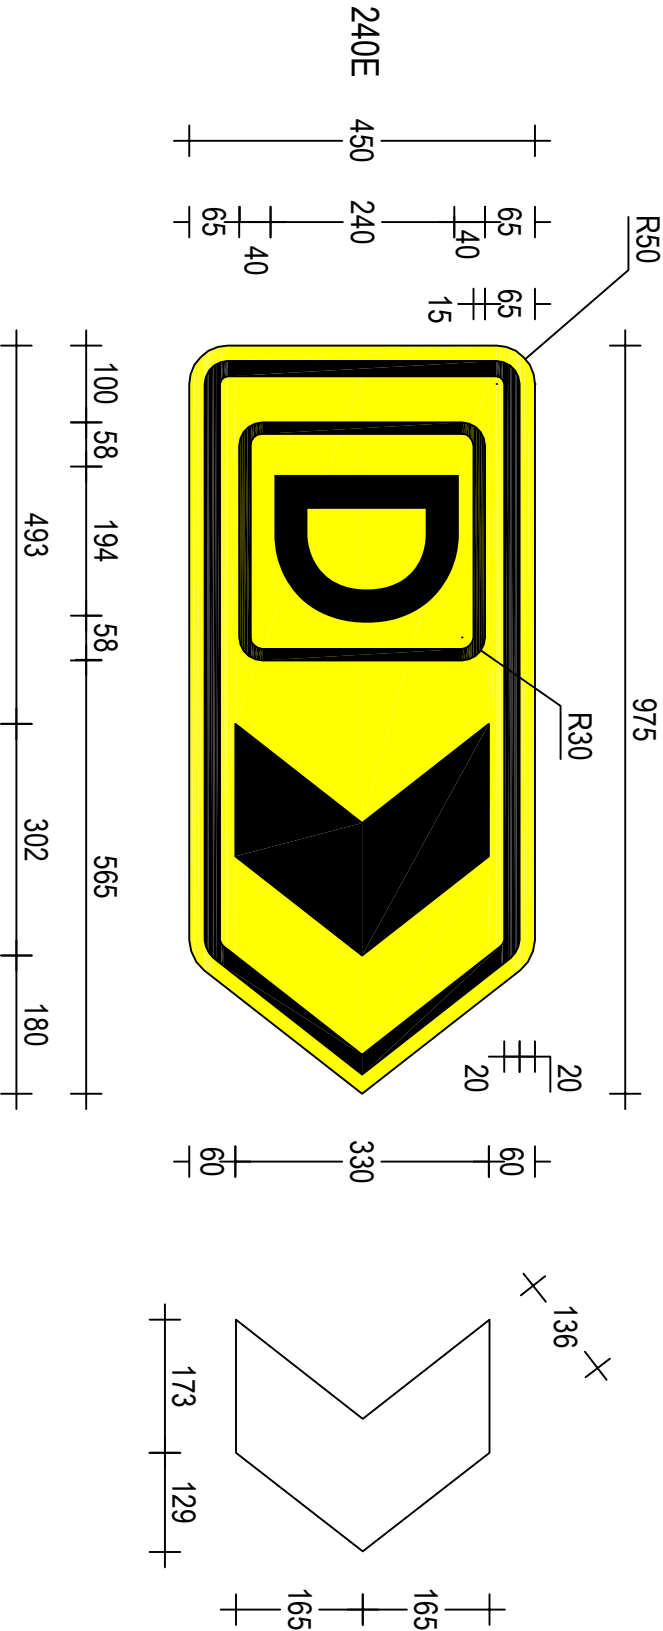

ACCEPTED FOR CONSTRUCTION