


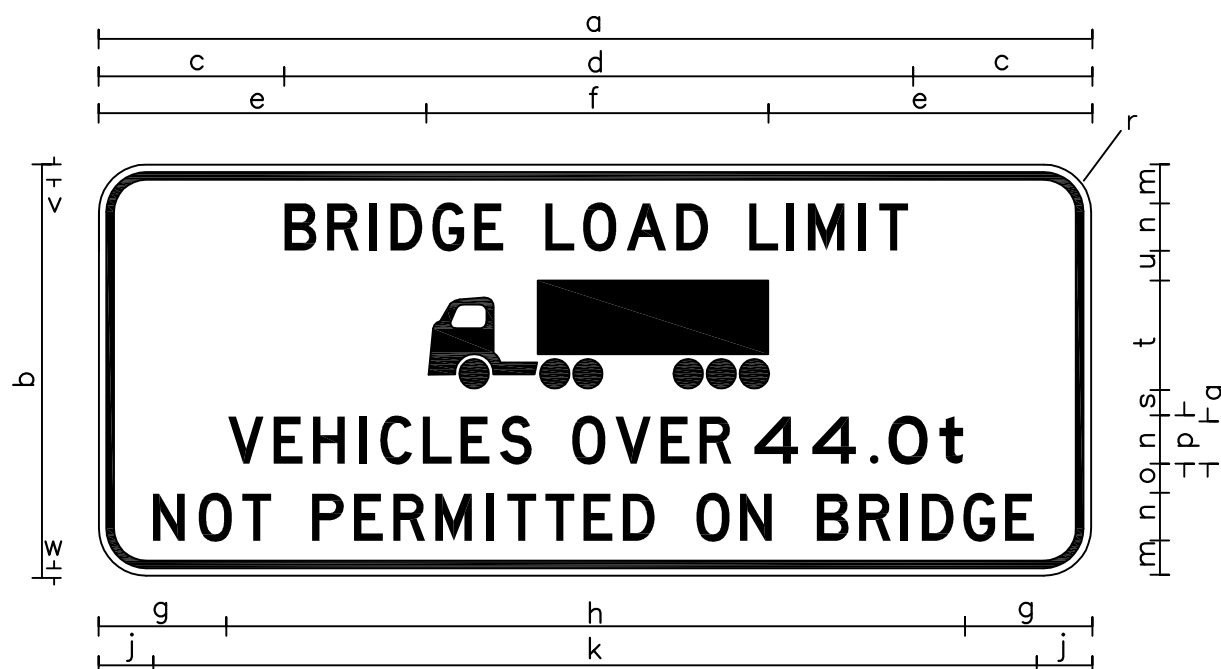

Black legend and border on Cl.1 White reflectorised ground.

	a	b	c	d	e	f	g	h	j	k	m
G9-369A	2100	870	388	1324	690	720	269	1562	114	1872	80
G9-369B	3360	1390	618	2124	1100	1160	430	2500	180	3000	120

n	o	p	q	r	s	t	u	v	w
100DM	60	100EM	90ME	100	60	230	60	32	16
160DM	80	160EM	140ME	175	110	370	110	48	24

SCALE 1:16

TITLE

GUIDE SIGN

G9-369

Drawn: VC 19.06.12

CHKD: FR 20.06.12



Transport
Roads & Maritime
Services

GUIDANCE AND DELINEATION UNIT
27-31 ARGYLE ST, PARRAMATTA 2150

H:\SIGNS\TTT\DRAWINGS\LOT\GUIDE \ G9-369.DWG

Revision: 1