


G9-372

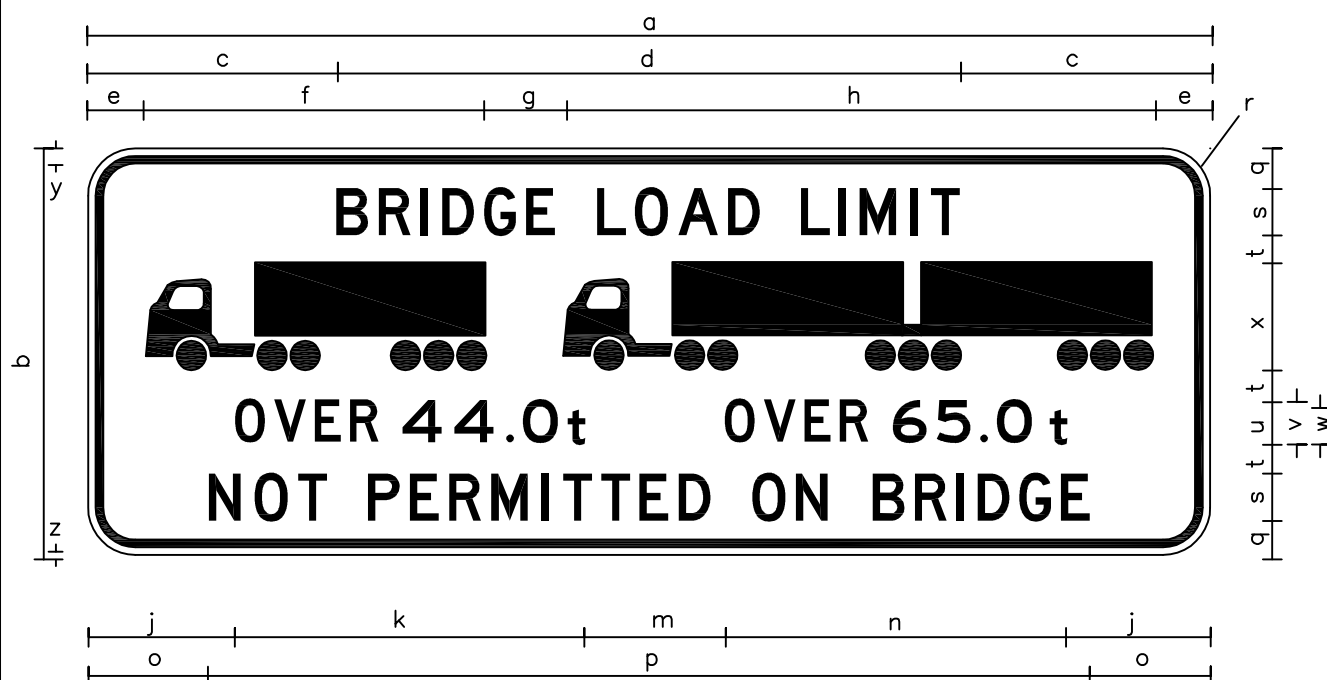

Black legend and border on Cl.1 white reflectorised ground.

	a	b	c	d	e	f	g	h	j	k	m	n
G9-372-A	2375	860	525	1324	120	721	172	1242	330	723	292	700
G9-372-B	3800	1380	838	2124	180	1160	282	1998	528	1144	490	1110

o	p	q	s	t	r	u	v	w	x	y	z
252	1871	80	100DM	60	100	90DM	90EM	75EM	230	32	16
400	3000	110	160DM	110	175	140DM	140EM	120ME	370	48	24

SCALE 1:16

TITLE

GUIDE SIGN
G9-372

Drawn: VC 19.06.12

CHKD: FR 20.06.12



GUIDANCE AND DELINEATION UNIT
27-31 ARGYLE ST, PARRAMATTA 2150

H:\SIGNS\TTT\DRAWINGS\PLOT\GUIDE \ G9-372.DWG

Revision: 1