
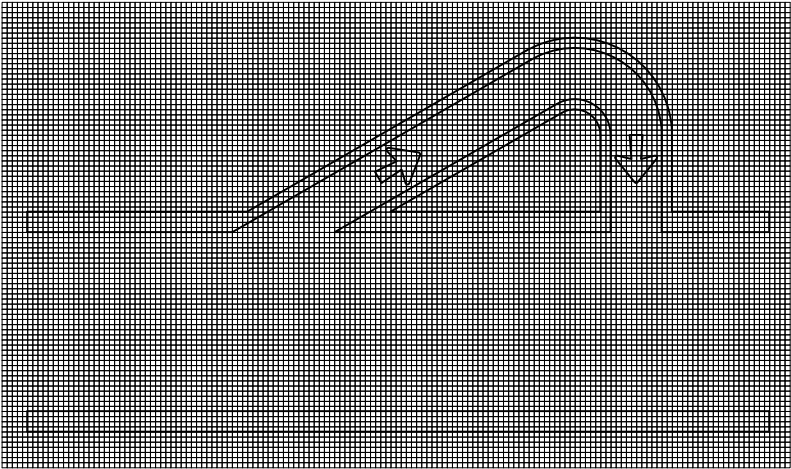


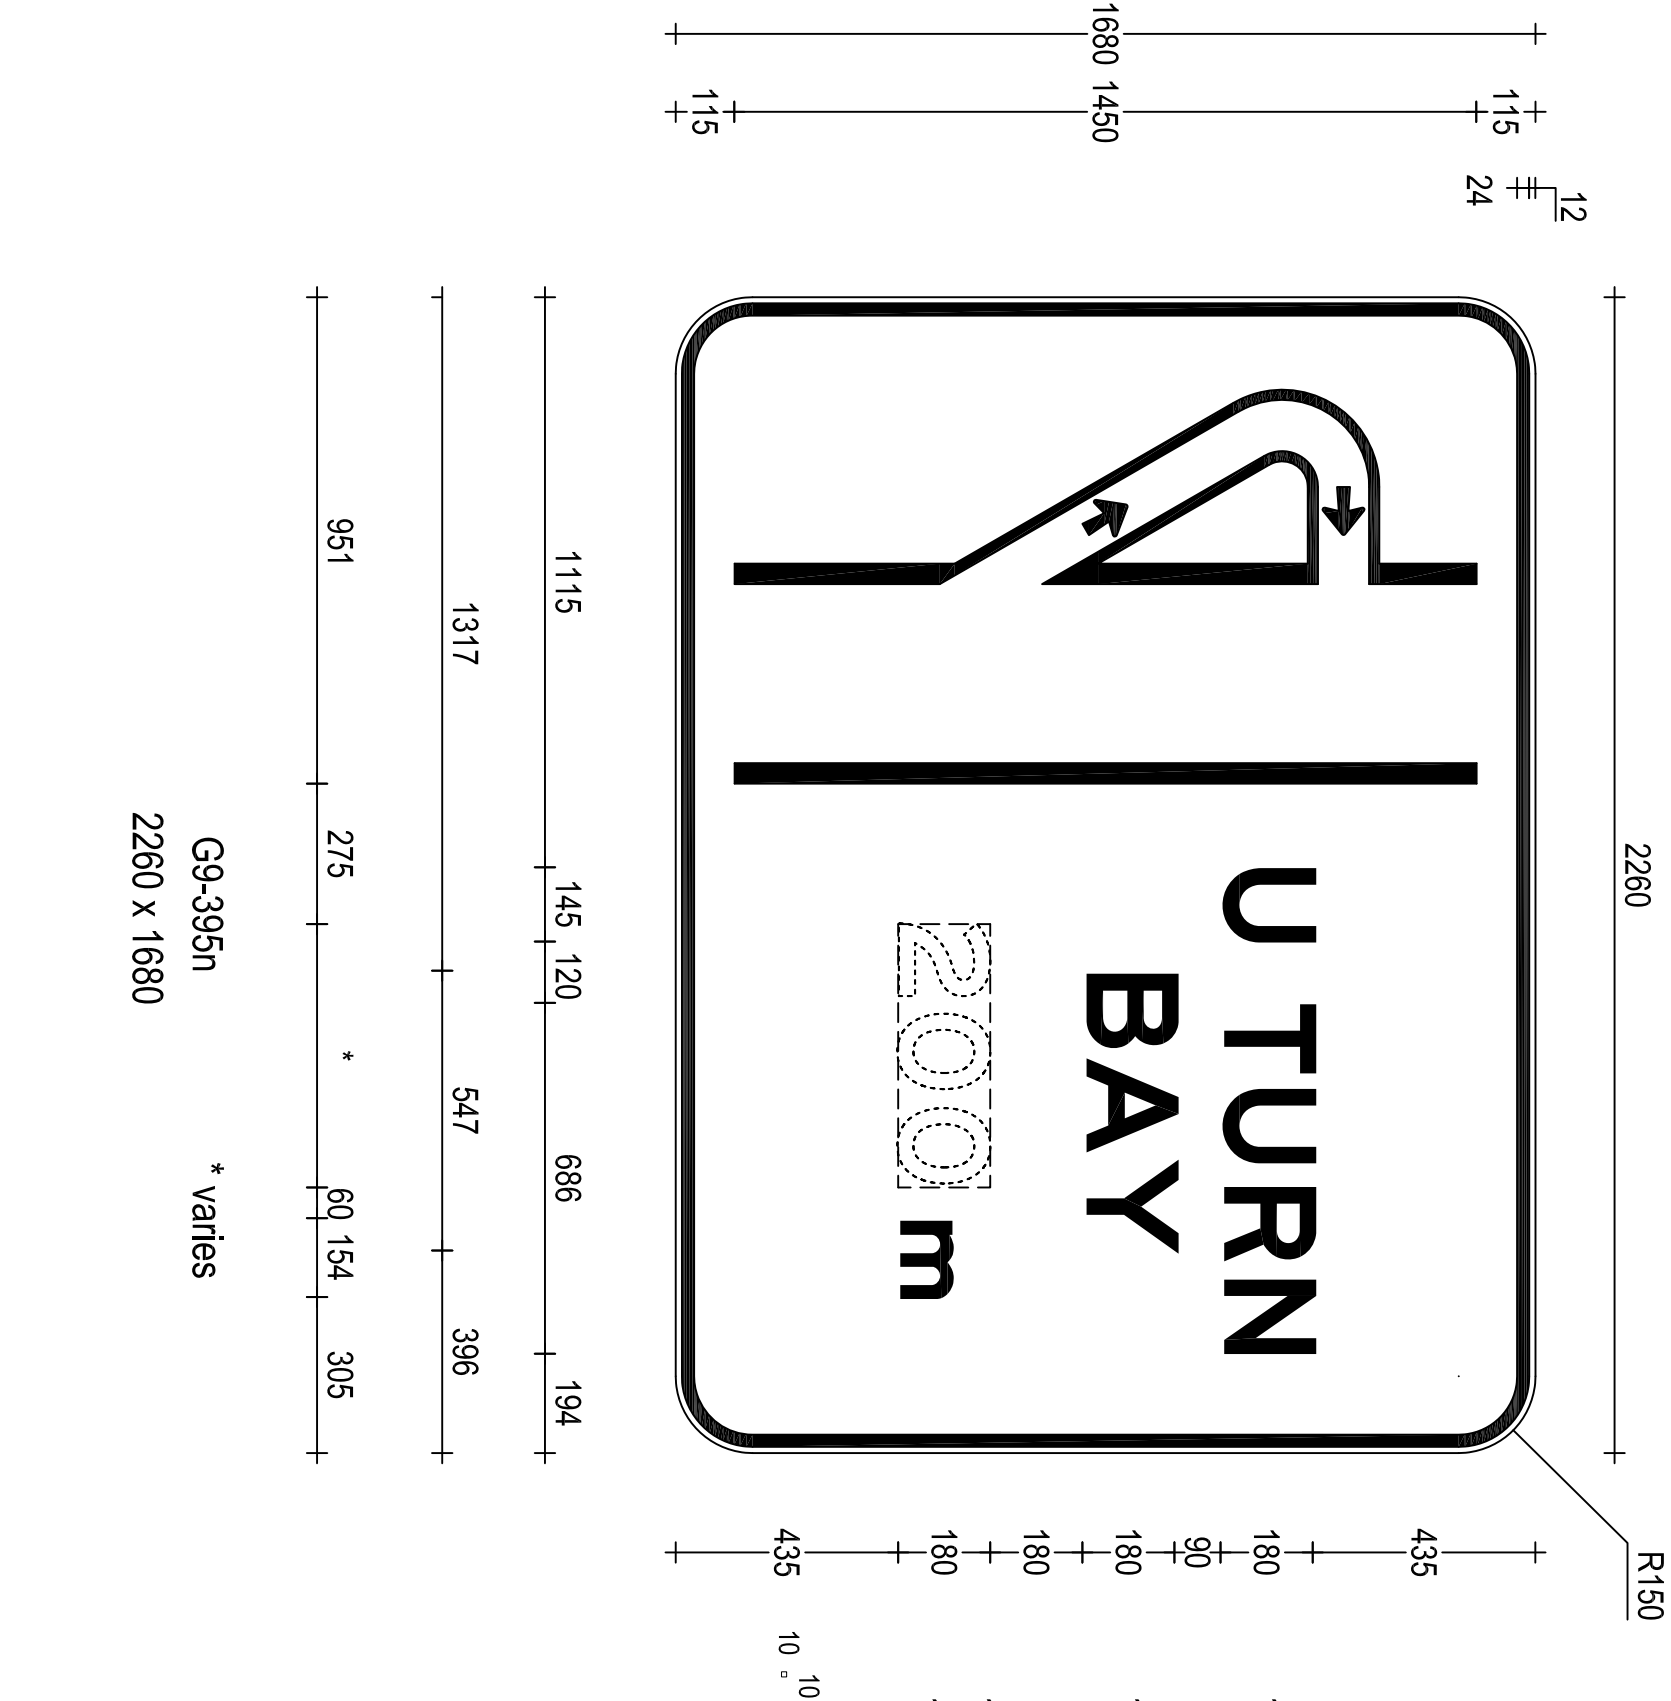

ACCEPTED FOR CONSTRUCTION

THIS DRAWING MAY BE PREPARED IN COLOUR AND MAY BE INCOMPLETE IF COPIED

0	5	10	15	20	25	30	35	40	45	50mm ON A3 SIZE ORIGINAL
OR CODE		Scan to Check Document Version	REV	DATE	AMENDMENT / REVISION DESCRIPTION		APPROVAL		DRAWING FILE LOCATION / NAME: H:\SIGN\TTP\DRAWINGS\PLOT\GUIDE\G9-395N.DWG	
			01	23-03-18	AS Forms & material classification revised		P. Oliver		MATERIALS: ALUMINIUM SIGN BLACK LEGEND SYMBOL AND BORDER ON AS1906.1 CL.400 WHITE REFLECTORISED GROUND	
ALL DIMENSIONS ARE IN MILLIMETRES UNLESS OTHERWISE SPECIFIED								SIGN TO BE MANUFACTURED IN ACCORDANCE WITH RMS QA SPECIFICATION 3400		
		DESIGNED		NAME: M. Davies DATE: 24-3-21		VERIFIED		NAME: P. Oliver TITLE: Manager Guidance & Delineation DATE: 24-03-21		
		REVIEWED		NAME: J. Rozos DATE: 24-03-21						
		PREPARED BY		NSW GOVERNMENT Transport Roads & Maritime Services						
				GUIDANCE AND DELINEATION UNIT ADVANCED TECHNICAL SERVICES INFRASTRUCTURE AND PLACE						
		GUIDE SIGN G9-395N U TURN BAY ()m (SYMBOLIC)								A3
		SCALE: 1:15		EDMS No. XXXXXXXXXX		SHEET No. 1		ISSUE 01		
								SHEET 1 OF 1		