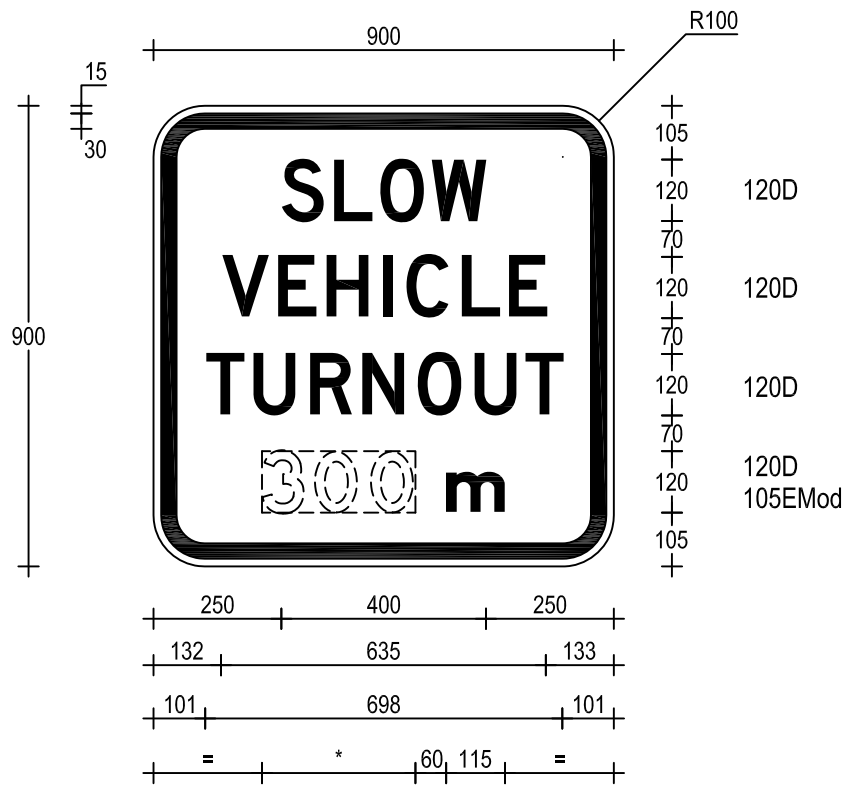

G9-50(A)
900 x 900

*varies

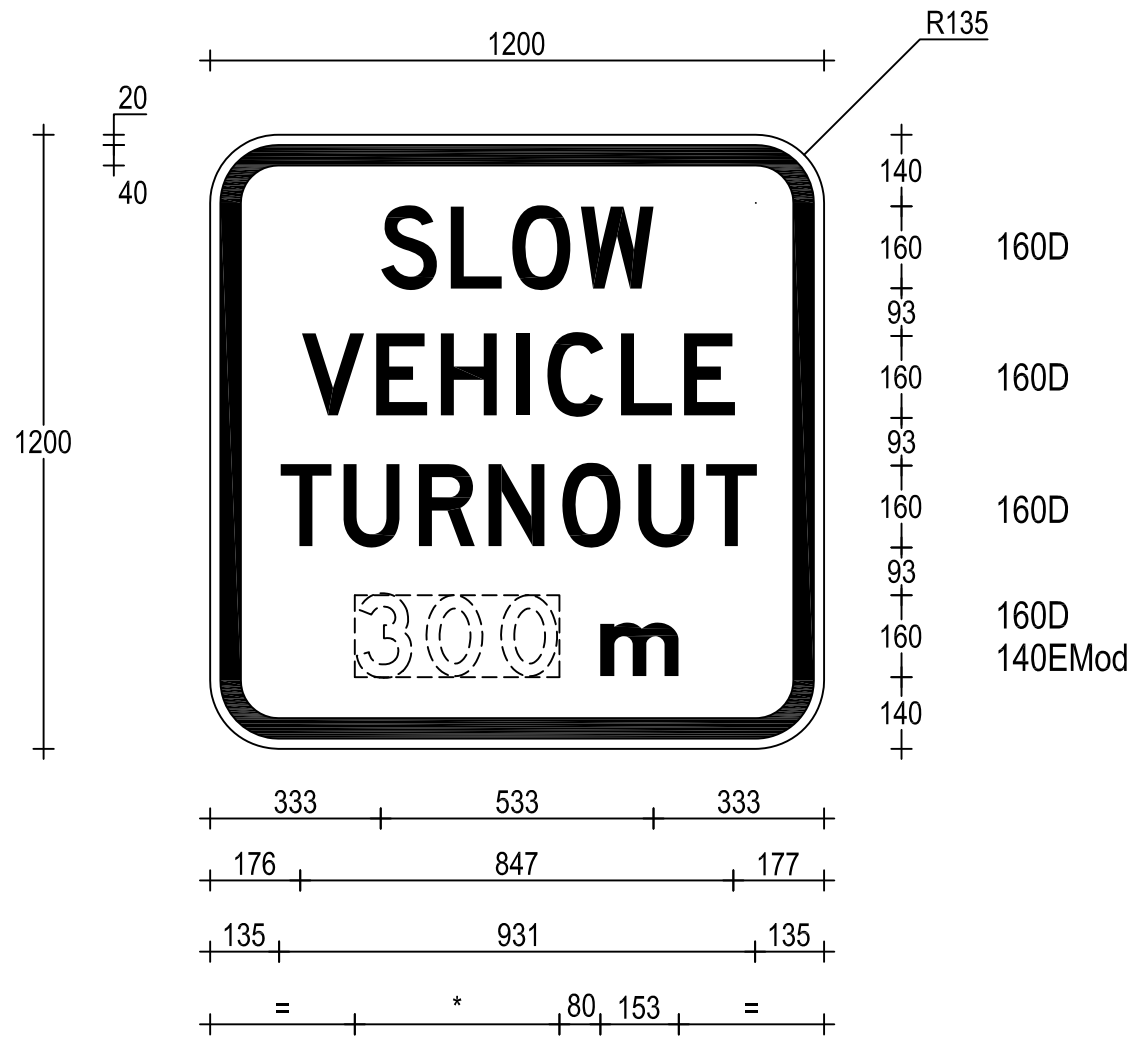

G9-50(B)
1200 x 1200

*varies

ACCEPTED FOR CONSTRUCTION

QR CODE	Scan to Check Document Version	REV	DATE	AMENDMENT / REVISION DESCRIPTION	APPROVAL
		01	23-08-18	AS Fonts & material classification revised	P.Oliver

DRAWING FILE LOCATION / NAME: H:\SIGNS\TTT\DRAWINGS\PLOT\GUIDE\G9-50.DWG

MATERIALS: ALUMINIUM SIGN
BLACK LEGEND AND BORDER
ON AS1906.1 CL.400 WHITE REFLECTORISED GROUND

ALL DIMENSIONS ARE IN MILLIMETRES UNLESS OTHERWISE SPECIFIED

SIGN TO BE MANUFACTURED IN ACCORDANCE WITH RMS QA SPECIFICATION 3400

DESIGNED
NAME M.Davies
DATE 24-3-21

REVIEWED
NAME J.Rozos
DATE 24-03-21

VERIFIED
NAME P.Oliver
TITLE Manager Guidance & Delineation
DATE 24-03-21

Transport Roads & Maritime Services
NSW GOVERNMENT

PREPARED BY
GUIDANCE AND DELINEATION UNIT
ADVANCED TECHNICAL SERVICES
INFRASTRUCTURE AND PLACE

A3

GUIDE SIGN
G9-50
SLOW VEHICLE TURNOUT (x)m

SHEET 1 OF 1

SCALE: 1:15	EDMS No. XXXXXXXXXX	SHEET No. 1	ISSUE 01

THIS DRAWING MAY BE PREPARED IN COLOUR AND MAY BE INCOMPLETE IF COPIED
50mm ON A3 SIZE ORIGINAL

© Roads and Maritime Services