



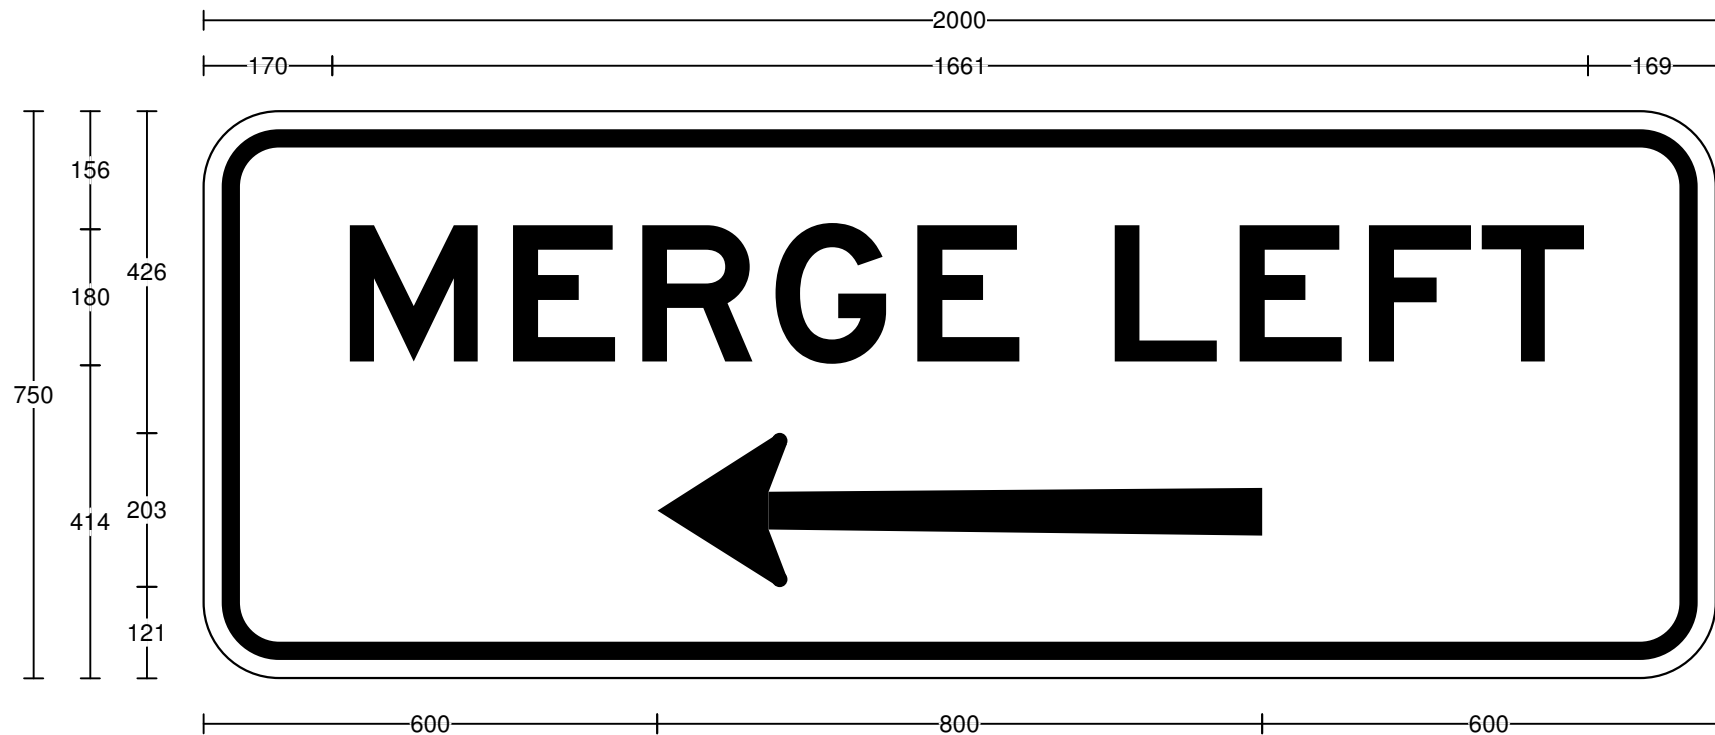

<u>Legend</u>	<u>Font Type</u>	<u>Font Size</u>
MERGE LEFT	FHWA Series E2000EX	180

Specifications:
BACKLIT SIGN
Black lgd
White grd

Size:	750 x 2000	Date:	30/9/19
Area:	1.5 sq.m	Scale:	1:10
Border:	24 x 24	Drawn:	RozosJ
Cnr Rad:	100	Checked:	
Patch CR:	NA	File:	G9--73-1n(L)
 Transport Roads & Maritime Services		Path:	H:\Signs\Standard_Signs & Symbols\Tunnel Signs\New Tunnel Signs
Prepared using TraSICAD Product of QMR		Guidance & Delineation Team Traffic Engineering Services Technical & Project Services 99 Phillip St Parramatta NSW 2150	G9-73-1n(L)

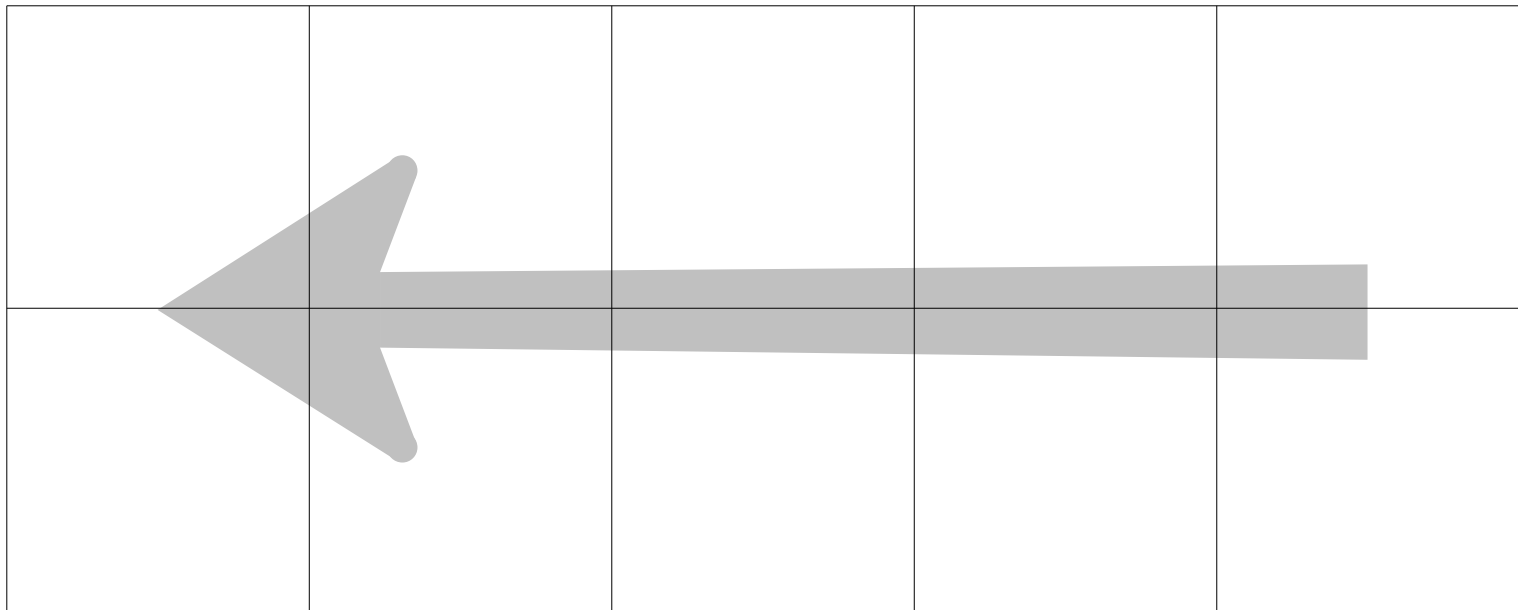

200mm Grid.

Details of Sign Face Symbols

Size:	750 x 2000	Date:	30/9/19
Area:	1.5 sq.m		
Border:	24 x 24	Drawn:	RozosJ
Cnr Rad:	100	Checked:	
		File:	G9--73-1n(L)
 Transport Roads & Maritime Services		Path:	H:\Signs\Standard_Signs & Symbols\Tunnel Signs\New Tunnel Signs
		Guidance & Delineation Team Traffic Engineering Services Technical & Project Services 99 Phillip St Parramatta NSW 2150	
Prepared using TraSICAD Product of QMR		G9-73-1n(L)	