



OR CODE		Scan to Check Document Version		REV	DATE	AMENDMENT / REVISION DESCRIPTION		APPROVAL		DRAWING FILE LOCATION / NAME: H:\SIGN\TTP\DRAWINGS\PLOT\GUIDE\G9-87-1.DWG	
		01		23-03-18		AS Forms & material classification revised		P. Oliver		MATERIALS: ALUMINIUM SIGN BLACK SYMBOL, ANNULUS & SLASH ON AS1906.1 CL.400 WHITE REFLECTORISED GROUND	
ALL DIMENSIONS ARE IN MILLIMETRES UNLESS OTHERWISE SPECIFIED											
DESIGNED		SIGNED		NAME		M. Davies		DATE		31-07-19	
REVIEWED		SIGNED		NAME		J. Rozos		DATE		31-07-19	
VERIFIED		SIGNED		NAME		P. Oliver		TITLE		Manager, Guidance & Delineation	
PREPARED BY		GUIDANCE AND DELINEATION UNIT		TRAFFIC ENGINEERING SERVICES		TECHNICAL AND PROJECT SERVICES		NSW GOVERNMENT		Transport Roads & Maritime Services	
SCALE: 1:15		EDMS No.		XXXXXXXXXX		SHEET No.		1		ISSUE 01	
SHEET 1 OF 1		A3									

ACCEPTED FOR CONSTRUCTION

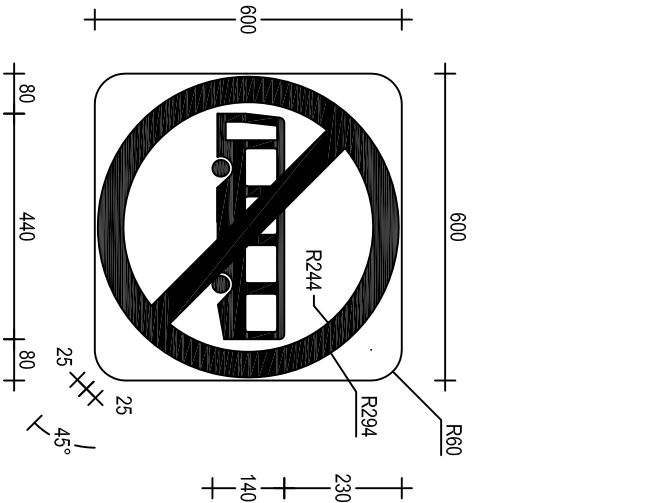


G9-87-1(A)
600 x 600

Symbol Detail

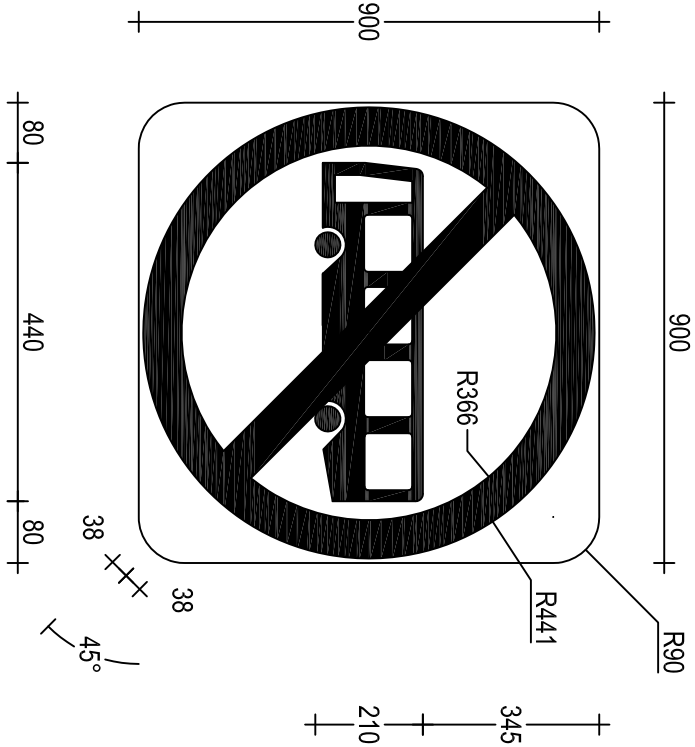

G9-87-1(B)
900 x 900

Symbol Detail

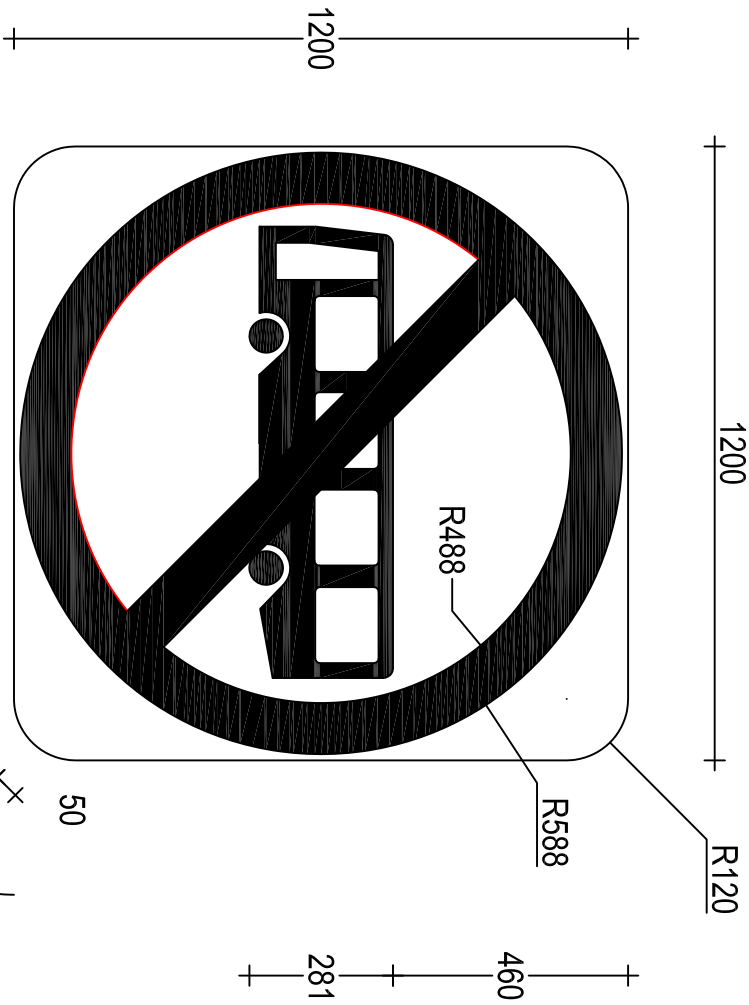

G9-87-1(C)
1200 x 1200

Symbol Detail