
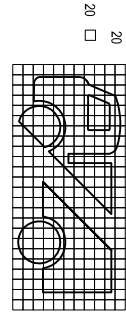
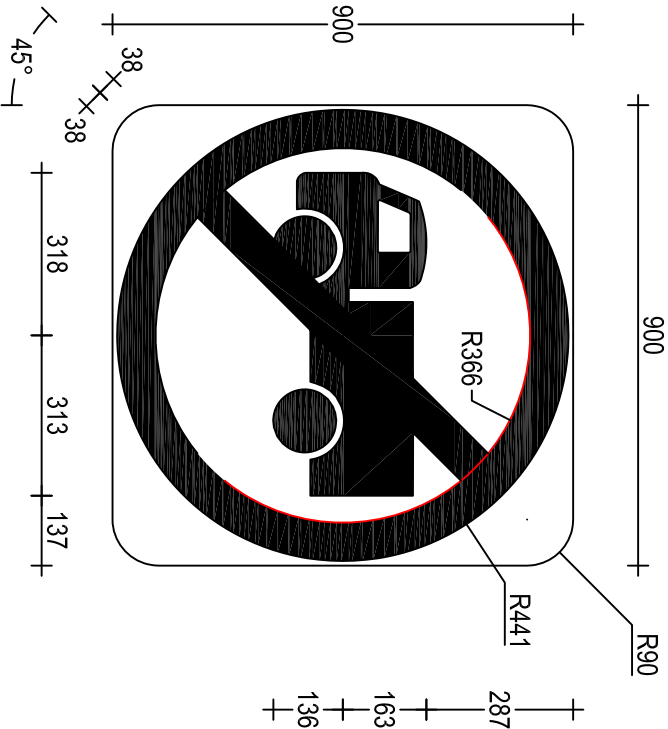



50mm ON A3 SIZE ORIGINAL

OR CODE Scan to Check Document Version		REV 01	DATE 23-03-18	AMENDMENT / REVISION DESCRIPTION AS Forms & material classification revised	APPROVAL P.Oliver	DRAWING FILE LOCATION / NAME: H:\SIGN\T\T\DRAWINGS\PLOT\GUIDE\G9-87-2.DWG
MATERIALS: ALUMINIUM SIGN BLACK SYMBOL, ANNULUS & SLASH ON AS1906.1 CL.400 WHITE REFLECTORISED GROUND						DESIGNED SIGNED NAME M.Davies DATE 31-07-19 REVIEWED SIGNED NAME J.Rozos DATE 31-07-19
SIGN TO BE MANUFACTURED IN ACCORDANCE WITH RMS QA SPECIFICATION 3400						VERIFIED SIGNED NAME P.Oliver DATE 31-07-19 TITLE Manager Guidance & Delineation
ALL DIMENSIONS ARE IN MILLIMETRES UNLESS OTHERWISE SPECIFIED						 Transport Roads & Maritime Services PREPARED BY GUIDANCE AND DELINEATION UNIT TRAFFIC ENGINEERING SERVICES TECHNICAL AND PROJECT SERVICES
GUIDE SIGN G9-87-2 ADVANCED TRUCKS PROHIBITED SHEET 1 OF 1						EDMS No. XXXXXXXXXX SHEET No. 1 ISSUE 01
SCALE: 1:15						A3
© Roads and Maritime Services						


ACCEPTED FOR CONSTRUCTION

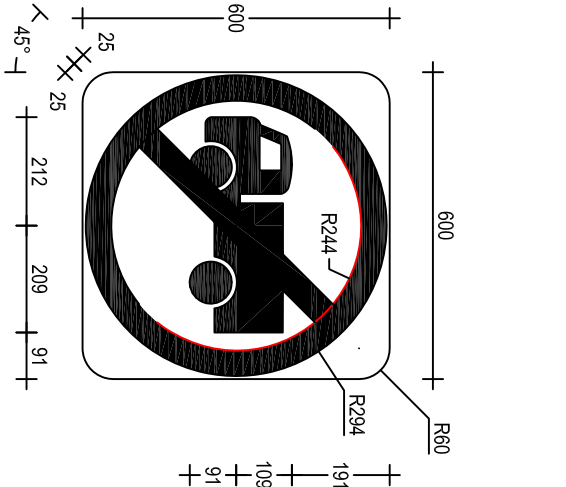


G9-87-2(B)
900 x 900

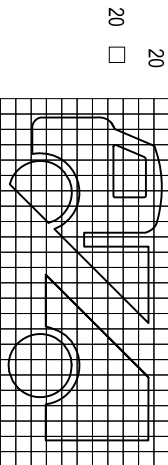

Symbol Detail

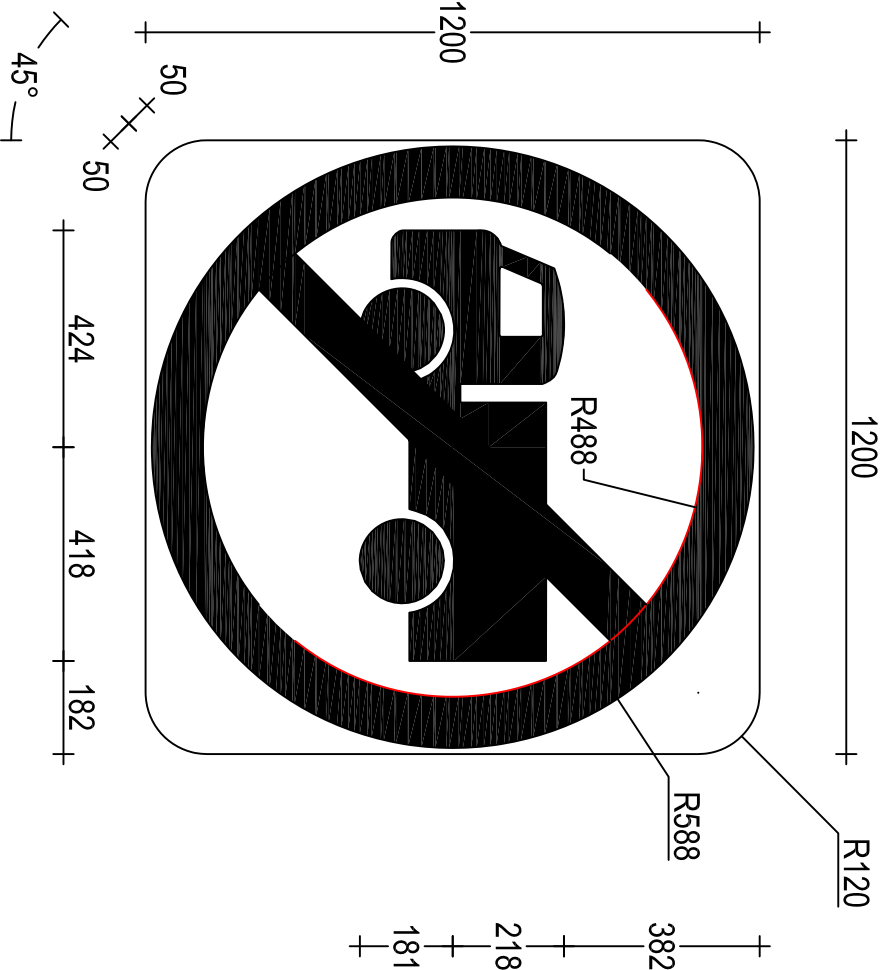

G9-87-2(C)
1200 x 1200

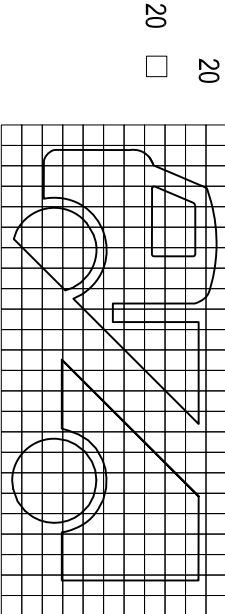

Symbol Detail