



05101520253035404550mm ON A3 SIZE ORIGINAL

QR CODE	Scan to Check Document Version	REV	DATE	AMENDMENT / REVISION DESCRIPTION	APPROVAL	DRAWING FILE LOCATION / NAME: H:\SIGNS\TTT\DRAWINGS\PI\OTREGULAT\R2-15.DWG
		01	23-08-18	AS Fonts & material classification revised	P Oliver	
ALL DIMENSIONS ARE IN MILLIMETRES UNLESS OTHERWISE SPECIFIED						
SIGN TO BE MANUFACTURED IN ACCORDANCE WITH RMS QA SPECIFICATION 3400						
MATERIALS: ALUMINIUM SIGN BLACK LEGEND AND BORDER ON AS1906.1 CL.400 WHITE REFLECTORISED GROUND						
DESIGNED						
SIGNED 						
NAME: M. Davies						
DATE: 31-07-19						
REVIEWED						
SIGNED 						
NAME: J. Rozdos						
DATE: 31-07-19						
VERIFIED						
SIGNED 						
NAME: P. Oliver						
TITLE: Manager, Guidance & Delineation						
DATE: 31-07-19						
 Transport Roads & Maritime Services						
NSW GOVERNMENT						
PREPARED BY						
GUIDANCE AND DELINEATION UNIT						
TRAFFIC ENGINEERING SERVICES						
TECHNICAL AND PROJECT SERVICES						
REGULATORY SIGN						
R2-15						
U TURN PERMITTED						
SHEET 1 OF 1						
SCALE: 1:10				EDMS No.	XXXXXXXXXX	A
				SHEET No.	1	
				ISS	0	

ACCEPTED FOR CONSTRUCTION

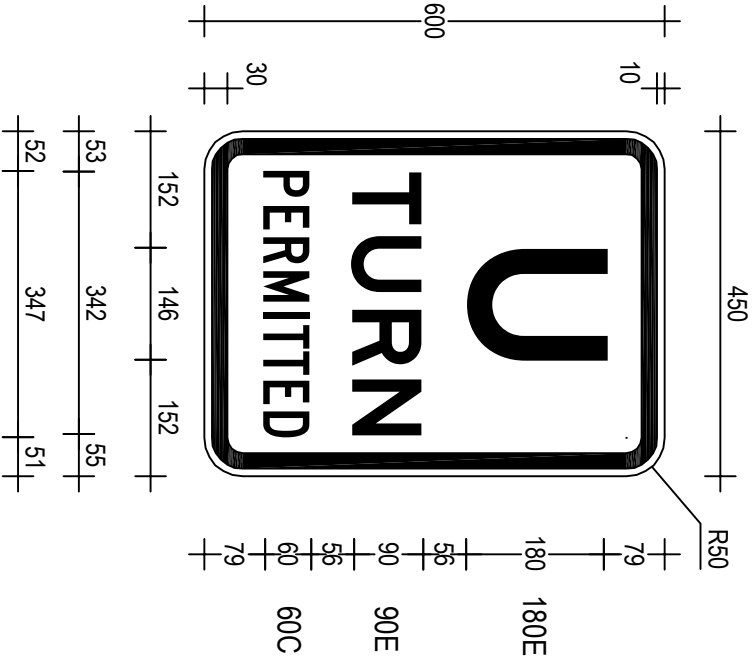

R2-15(A)
450 x 600

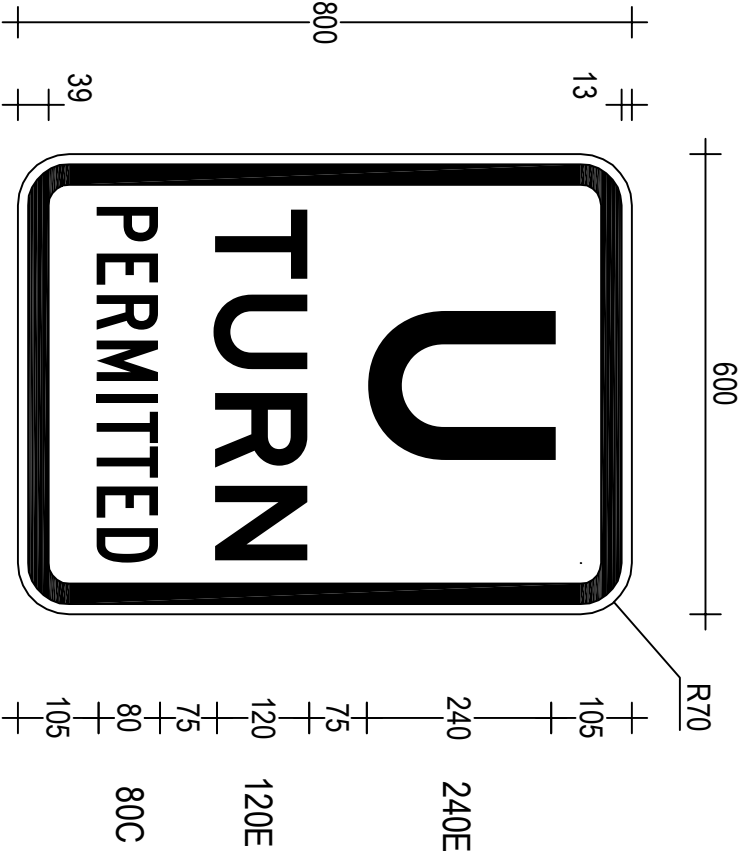

R2-15(B)
600 x 800